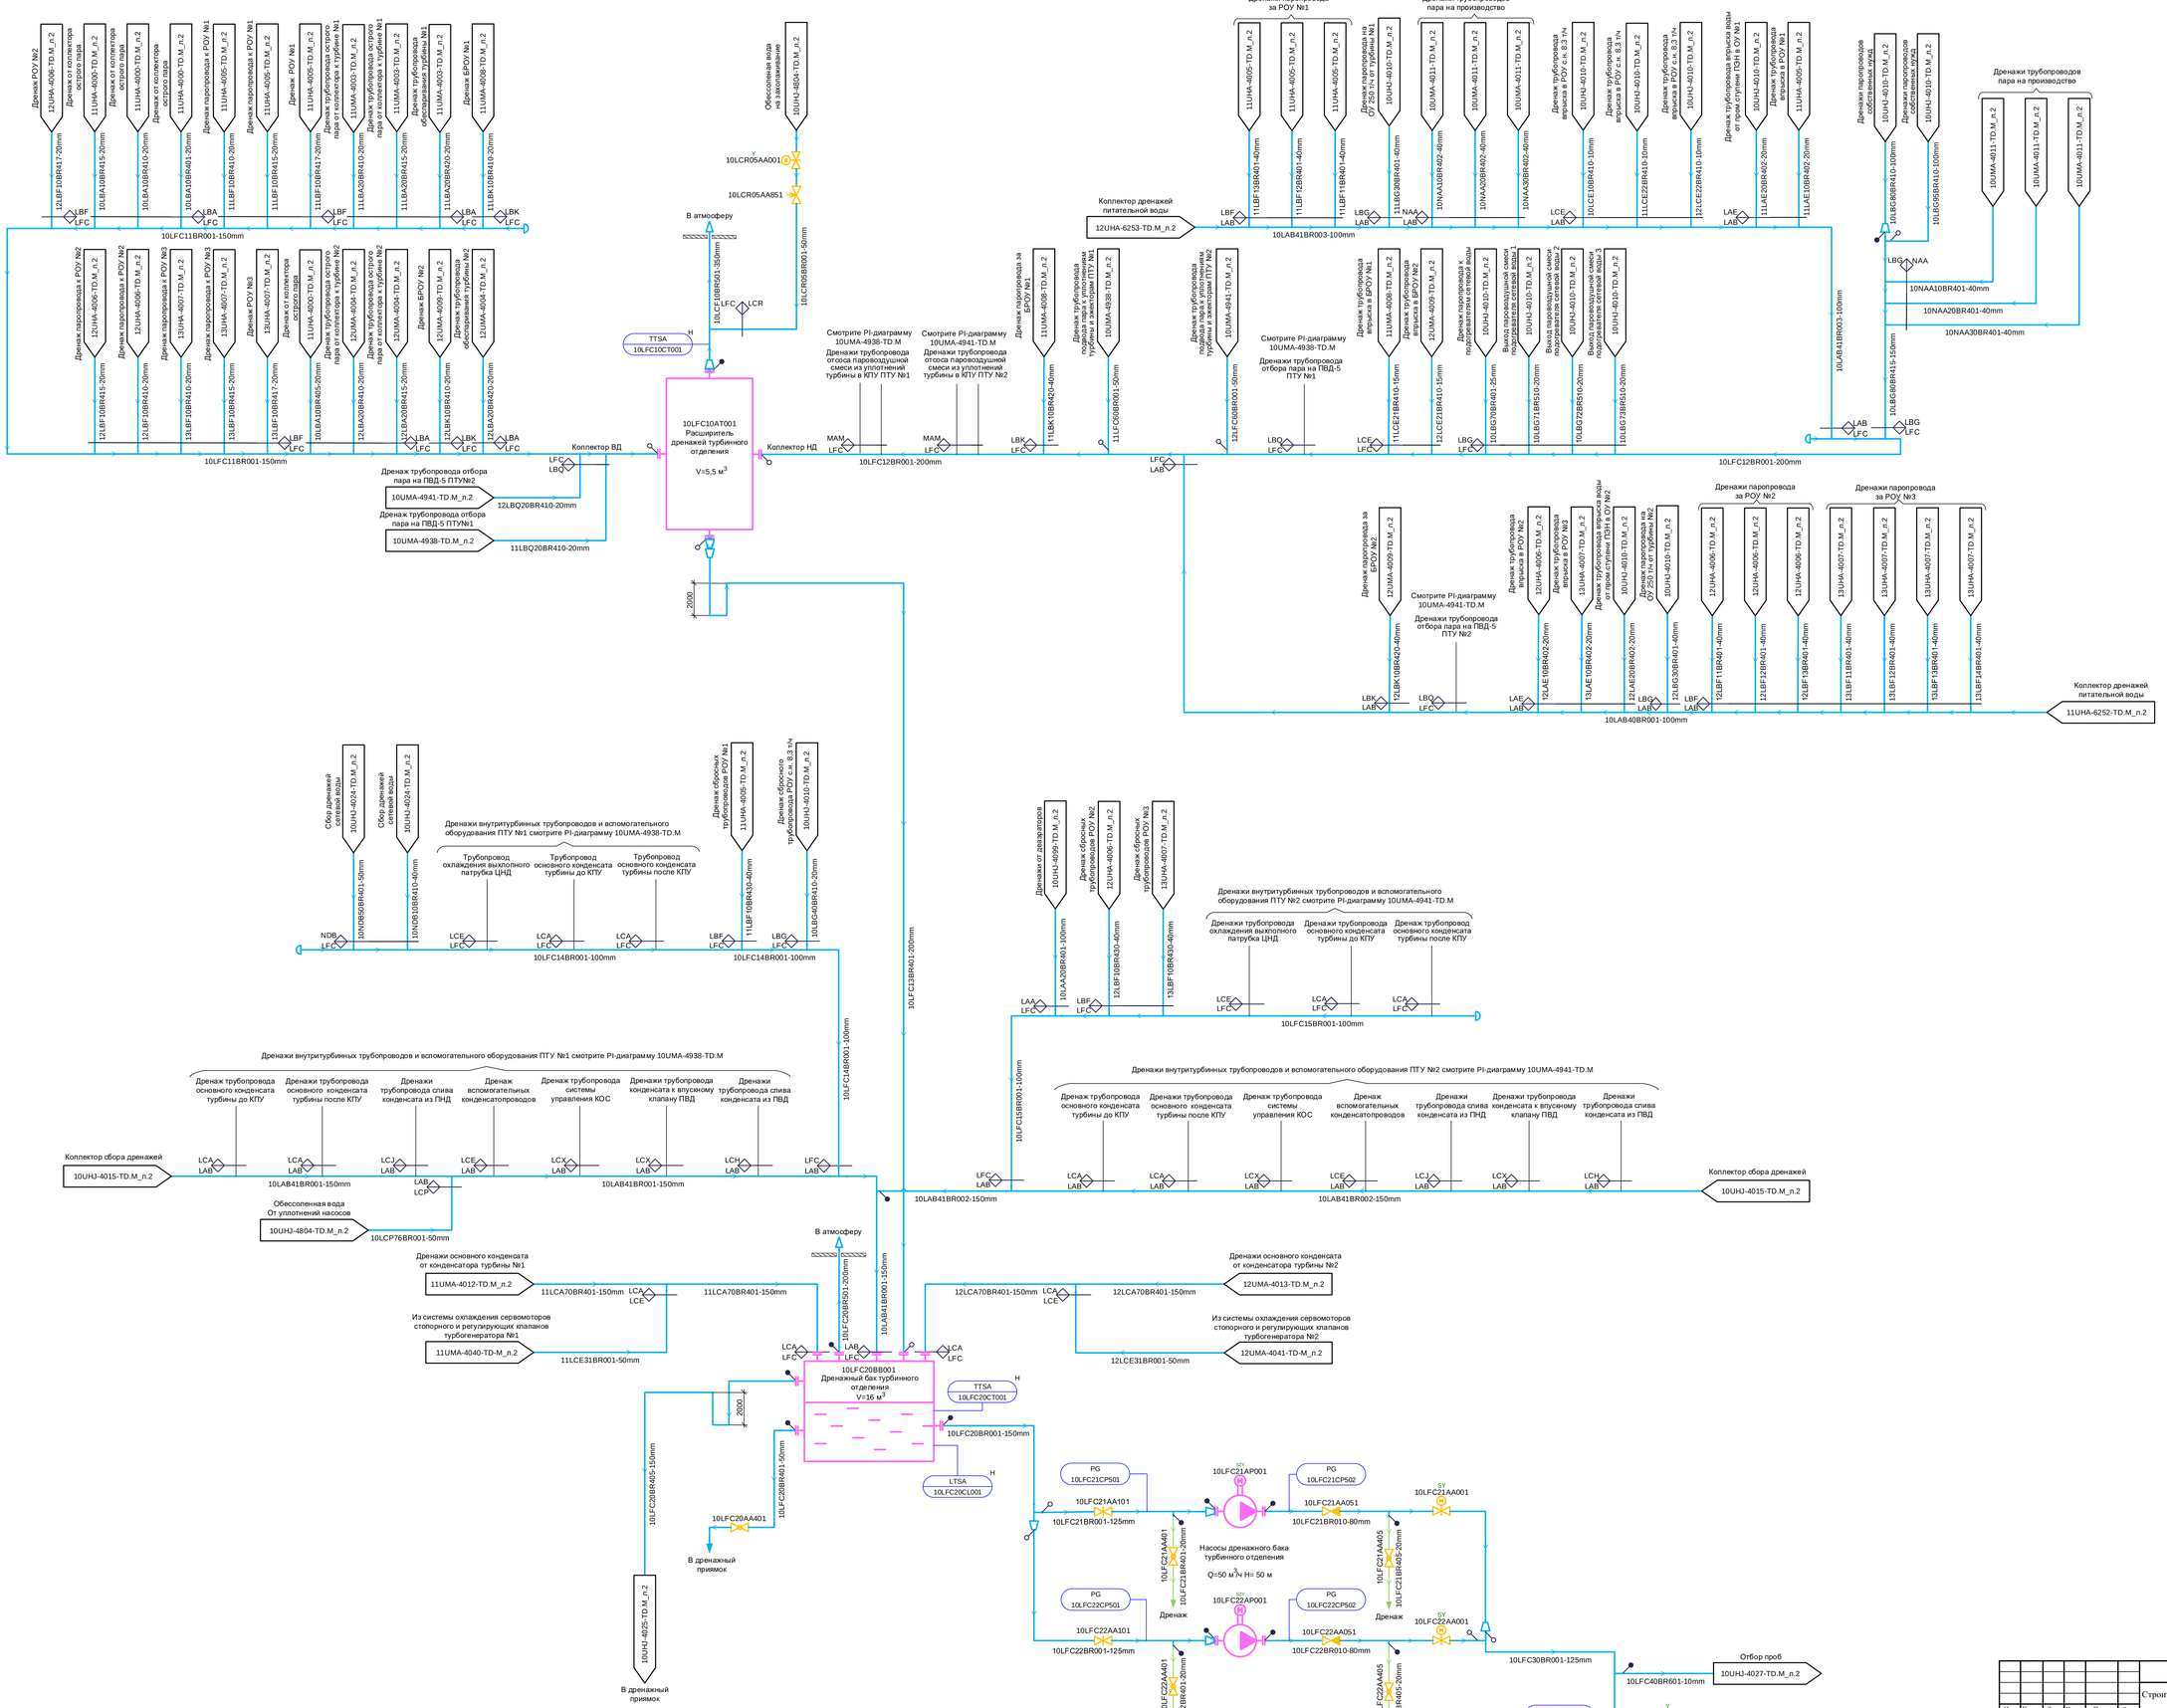

Изм.	Кол.уч.	Лист	№ док.	Подп.	Дата	141N4 – 10UMA – 4031 – TD.M
Разработал	Калинкина					Амурская ТЭС. Обеспечение нужд Амурского ГПЗ. Строительство основного технологического комплекса объектов Амурской ТЭС (2 ПГУ-800МВт). Этап 1. Амурская ТЭС (ПСУ-2х80 МВт)"
Проверил	Майорова					Паротурбинное отделение. PI-диаграмма трубопроводов дренажей турбинного отделения
Н. контр.	Гриднина					PI-диаграмма трубопроводов дренажей турбинного отделения. Система LFC

Стадия	Лист	Листов
Р	2	

АКЦИОНЕРНОЕ ОБЩЕСТВО «ТЕХНОПРОМЭКСПОРТ СТРОЙ»

Согласовано

Взам. инв. №

Подпись и дата

Инв. № подл.

ОАО"СУ

Соболева

Формат А0