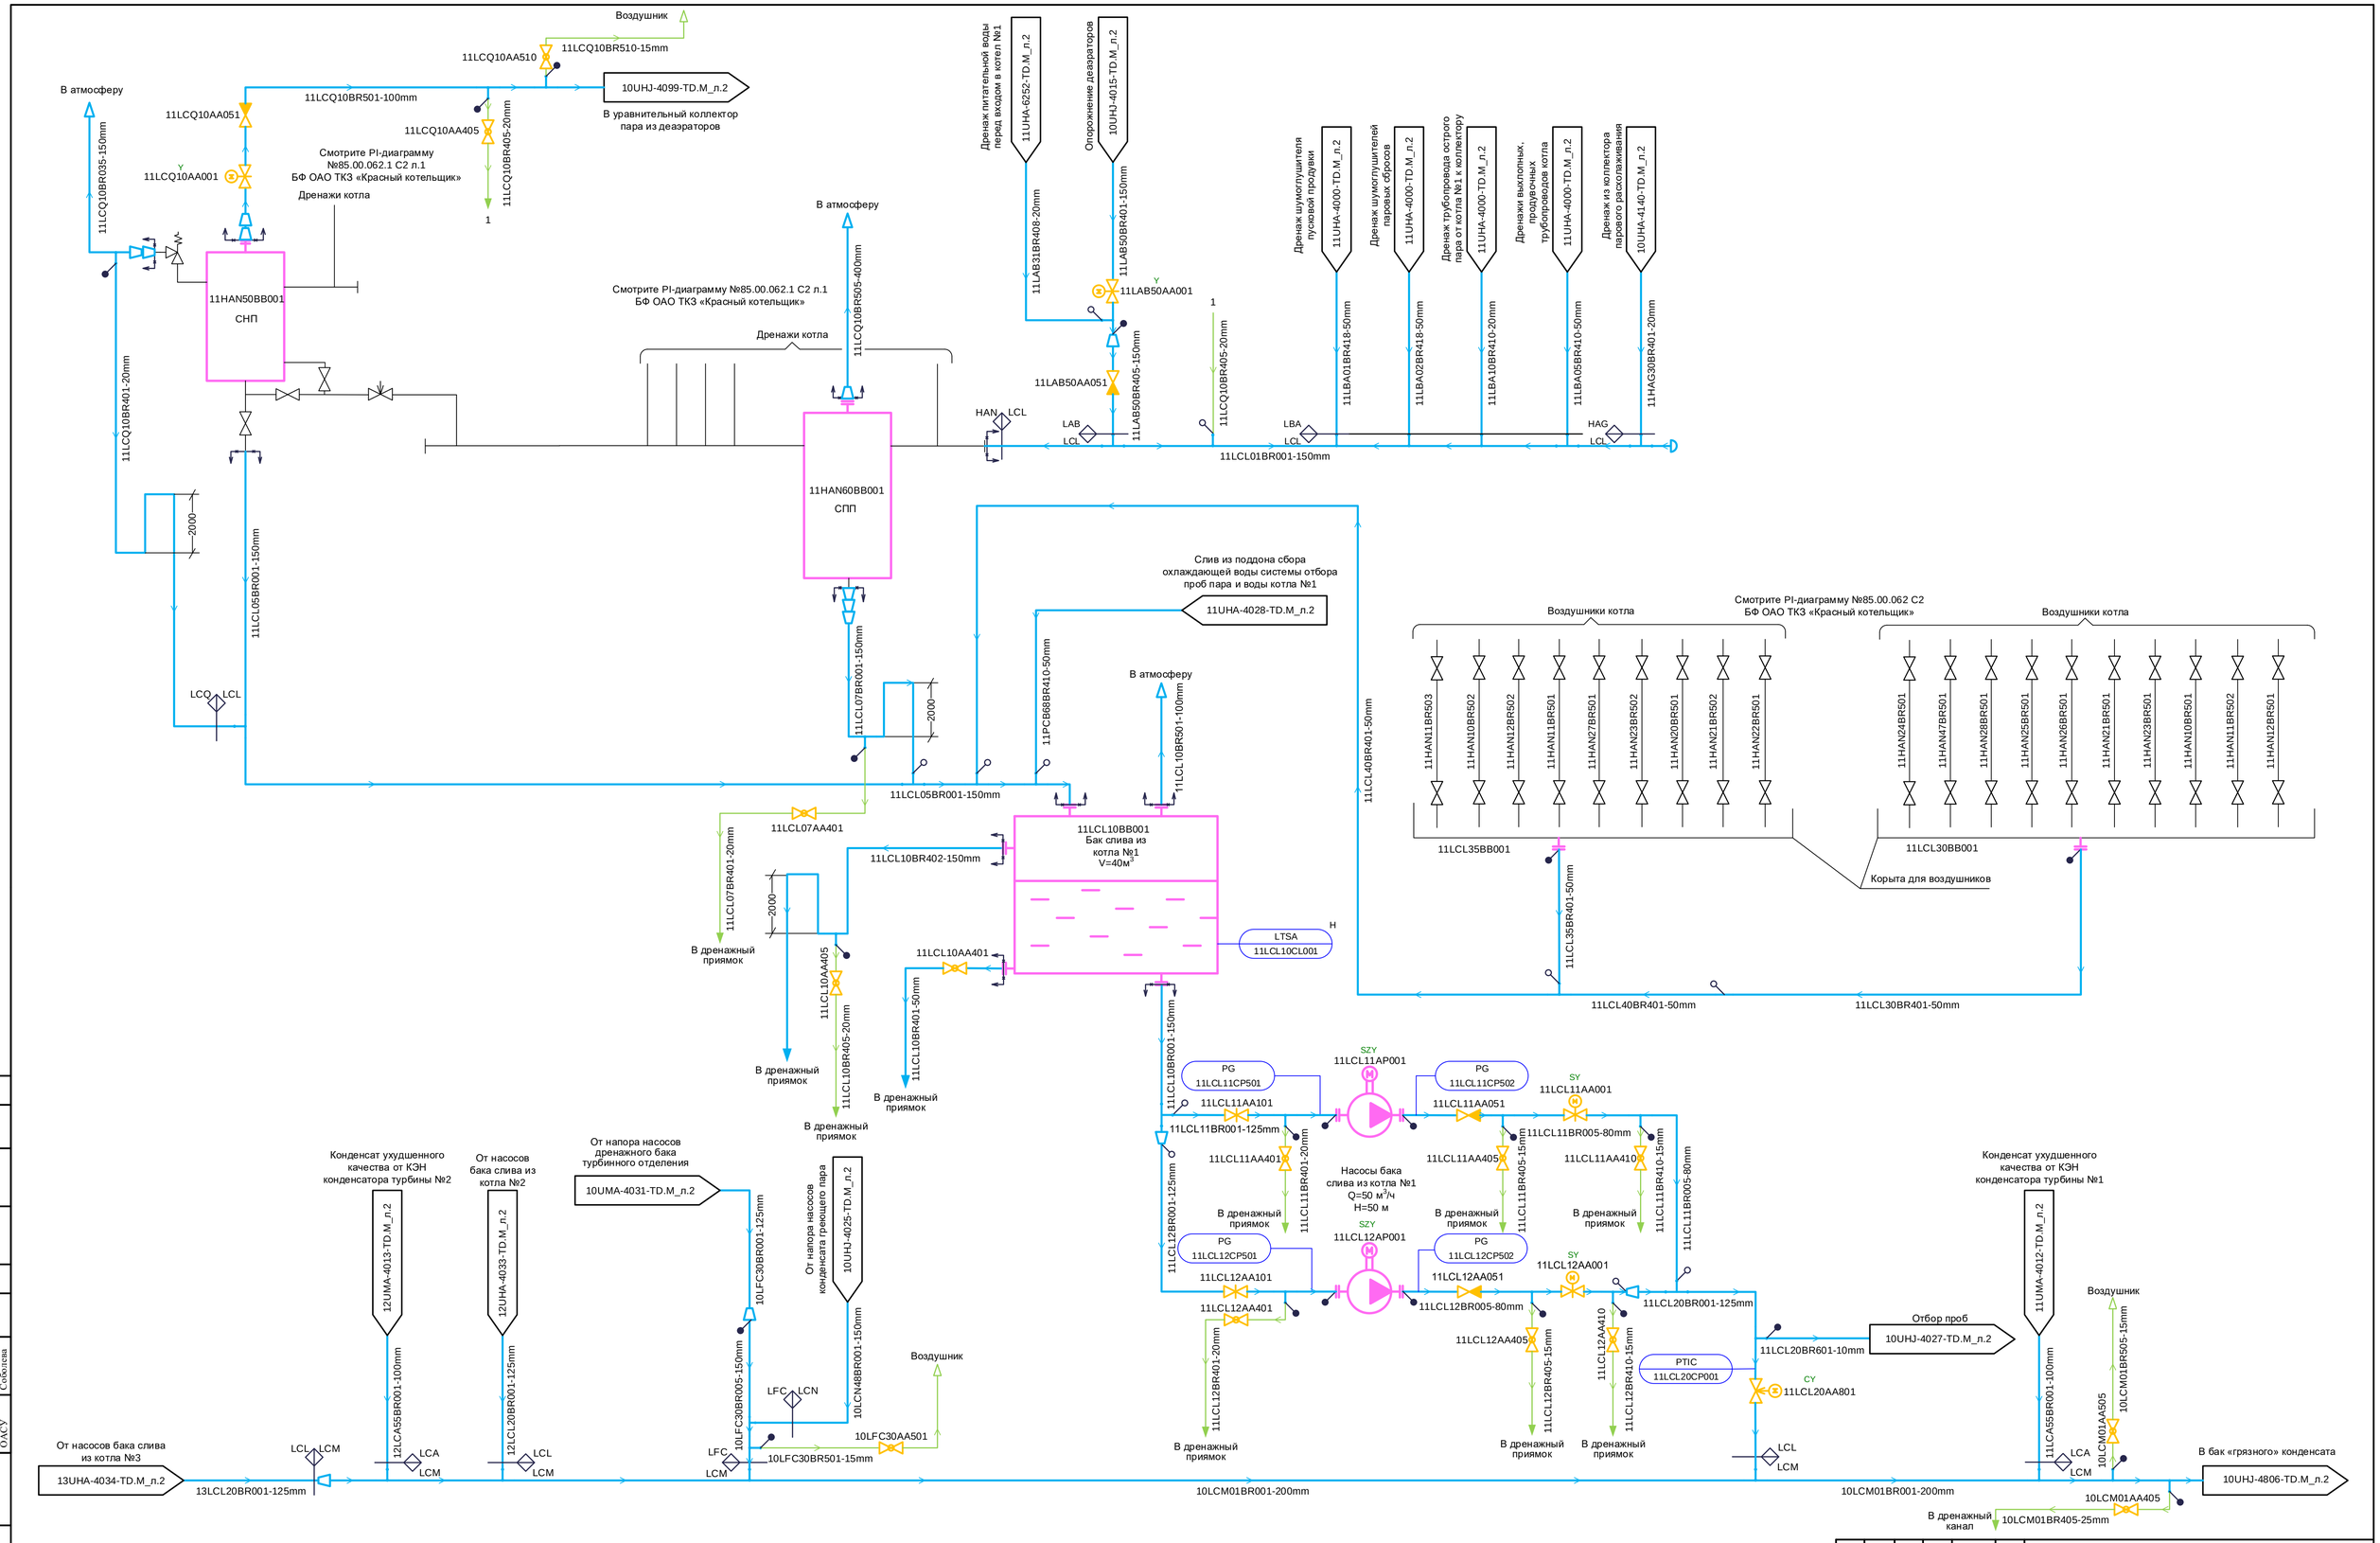

1	—	Зам.	1501-23			
Изм.	Кол.уч	Лист	№ док.	Подп.	Дата	

141N4 – 11UHA – 4032 – TD.M

Амурская ТЭС. Обеспечение нужд Амурского ГПЗ. Строительство основного технологического комплекса объектов Амурской ТЭС (2 ПСУх80МВт). Этап 1."Амурская ТЭС (ПСУ-2х80 МВт)"

Разработал	Брылева	
Проверил	Майорова	
Н. контр.	Черемушкина	

Главный корпус. PI-диаграмма дренажей, воздушников и вспомогательных трубопроводов котла №1.

PI-диаграмма дренажей, воздушников и вспомогательных трубопроводов котла №1. Системы LCL, LCQ.

Стадия	Лист	Листов
Р	2	

АКЦИОНЕРНОЕ ОБЩЕСТВО ИНСТИТУТ ТЕПЛОЭЛЕКТРОПРОЕКТ г. МОСКВА

Согласовано: ОАСУ Соболева

Взам. инв. №

Подпись и дата

Инв. № подл.

Формат А1