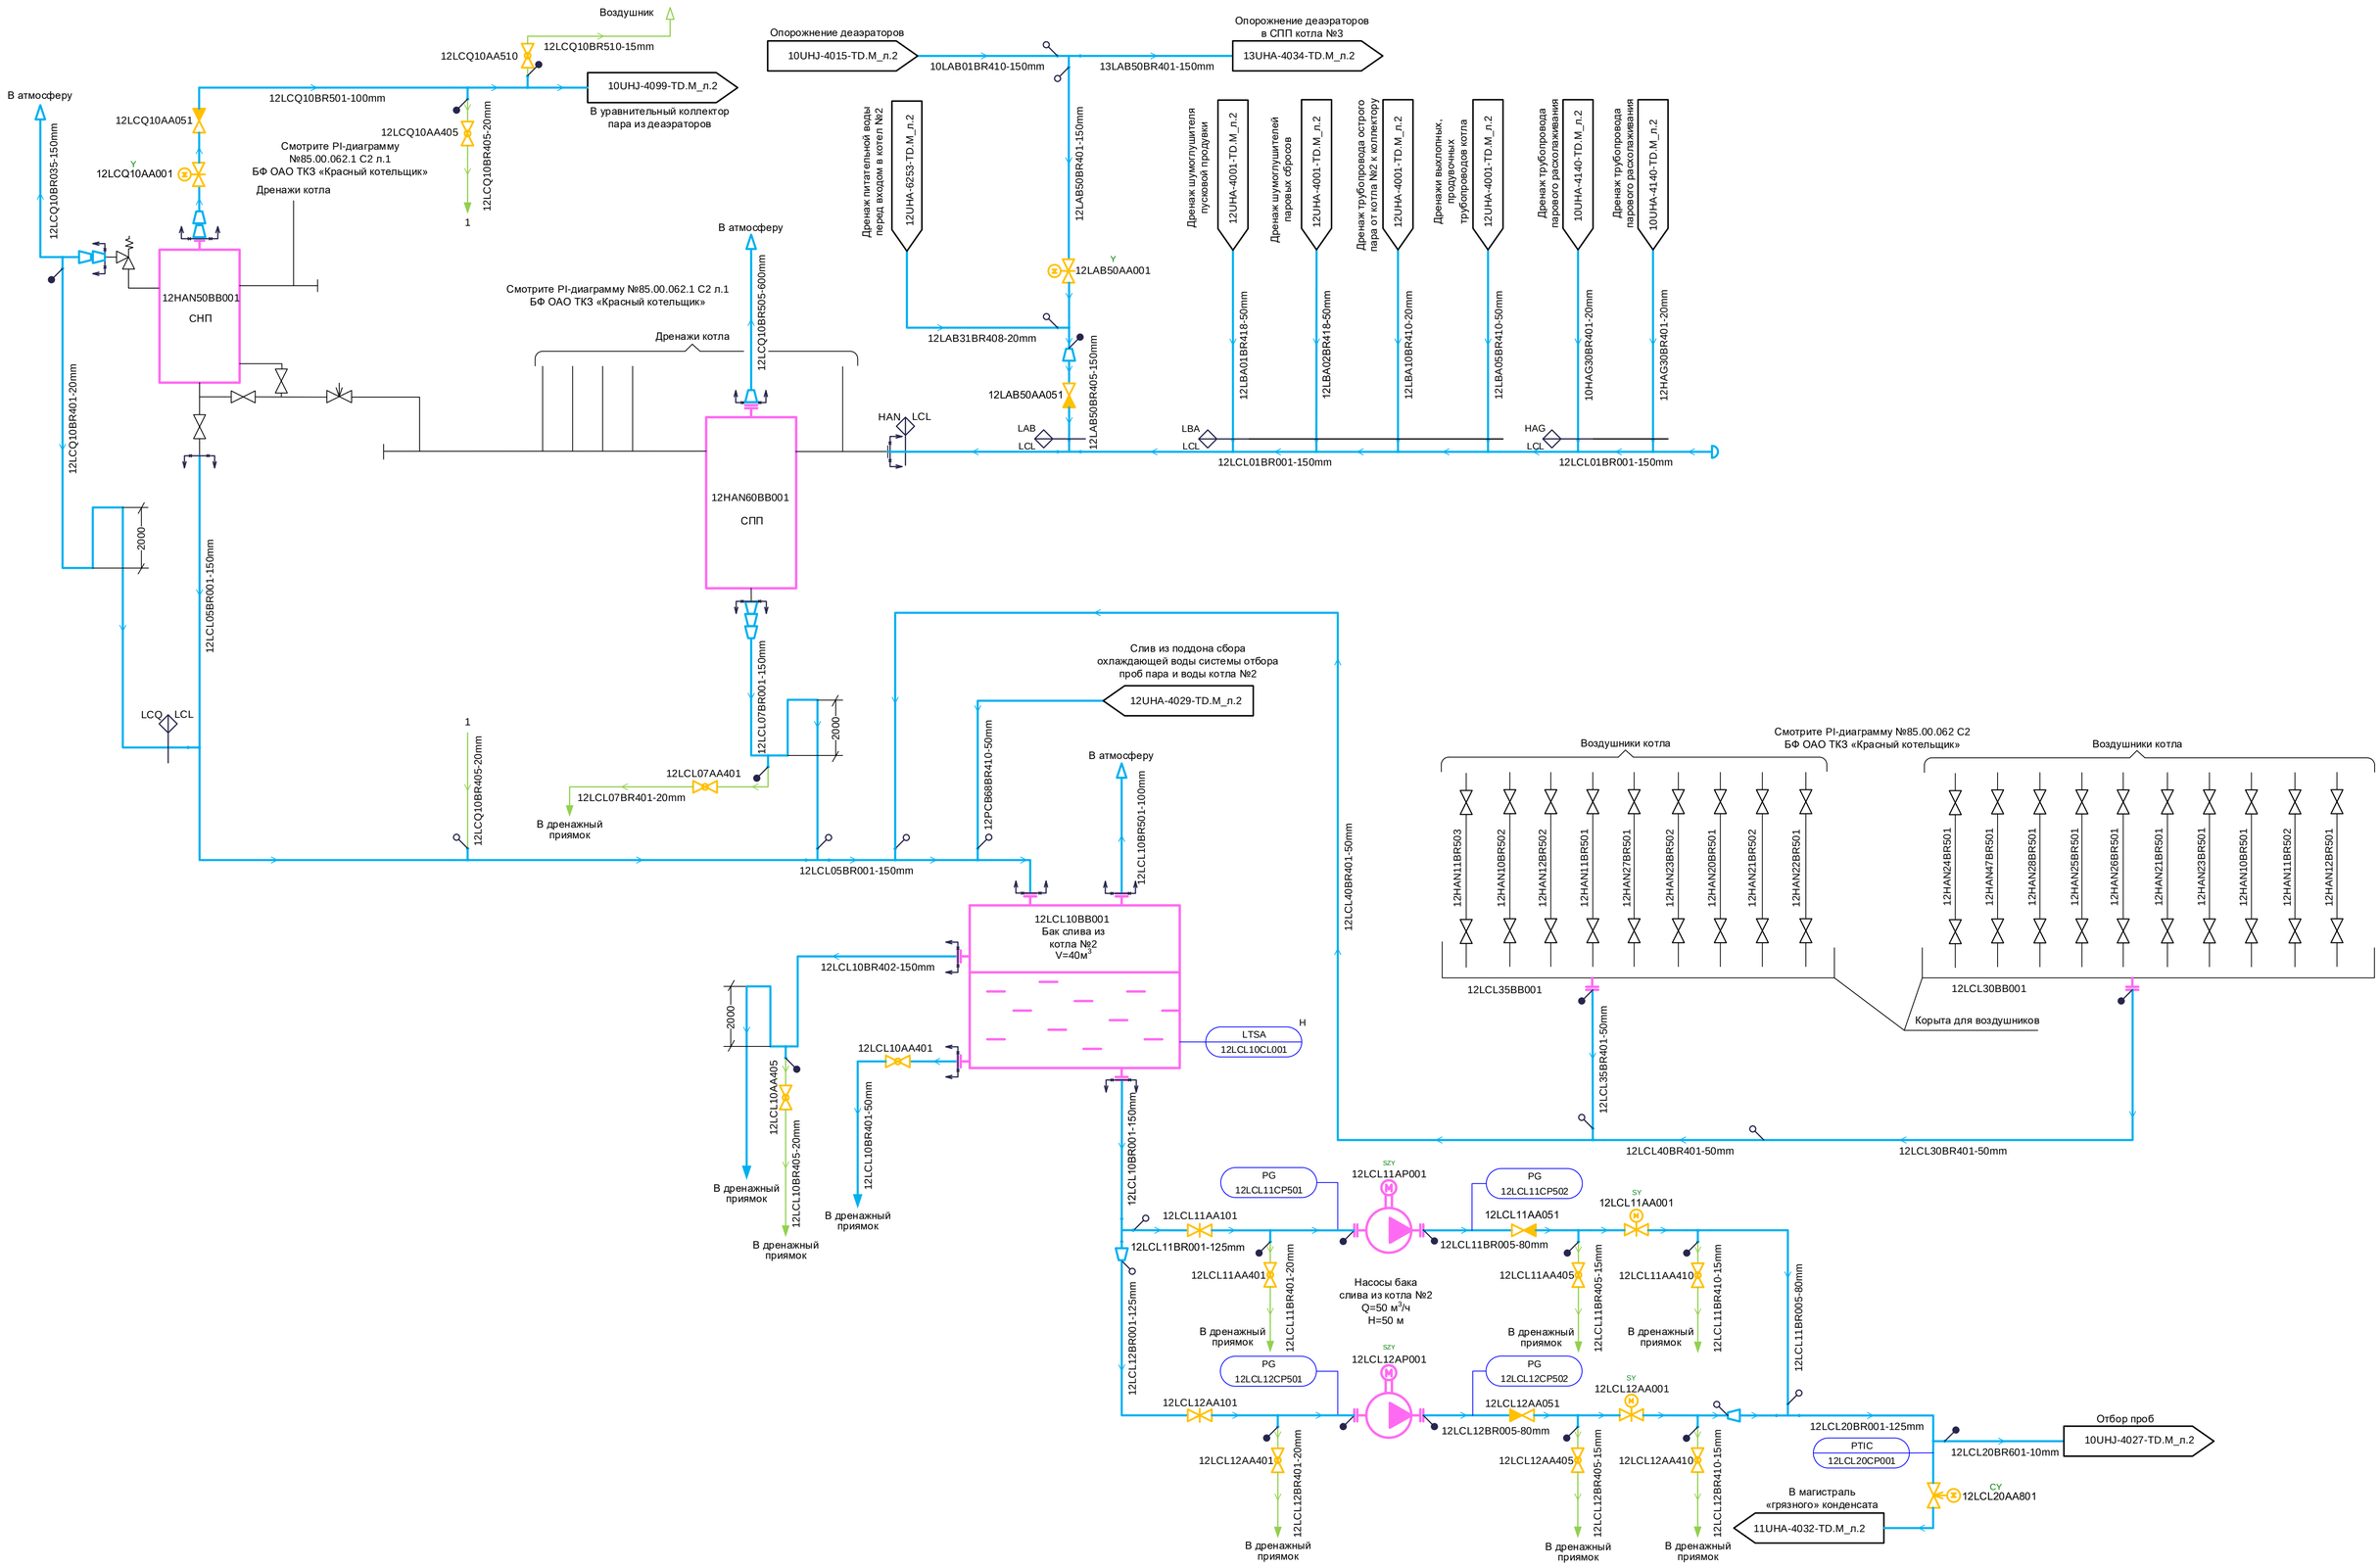

Изм.	Кол.уч	Лист	№ док.	Подп.	Дата	141N4 – 12UHA – 4033 – TD.M
						Амурская ТЭС. Обеспечение нужд Амурского ГПЗ. Строительство основного технологического комплекса объектов Амурской ТЭС (2 ПСУ х80МВт). Этап 1."Амурская ТЭС (ПСУ-2х80 МВт)"
Разработал		Брылева				Главный корпус. PI-диаграмма дренажей, воздушников и вспомогательных трубопроводов котла №2.
Проверил		Калинкина				Стадия: Р; Лист: 2; Листов:
Н. контр.		Гридчина				PI-диаграмма дренажей, воздушников и вспомогательных трубопроводов котла №2. Системы LCL, LCQ.

АКЦИОНЕРНОЕ ОБЩЕСТВО «ВТИ» ТЕПЛОЭЛЕКТРОПРОЕКТ г. МОСКВА

Согласовано: ОАСУ, Соболева

Взам. инв. №

Подпись и дата

Инв. № подл.

Формат А1