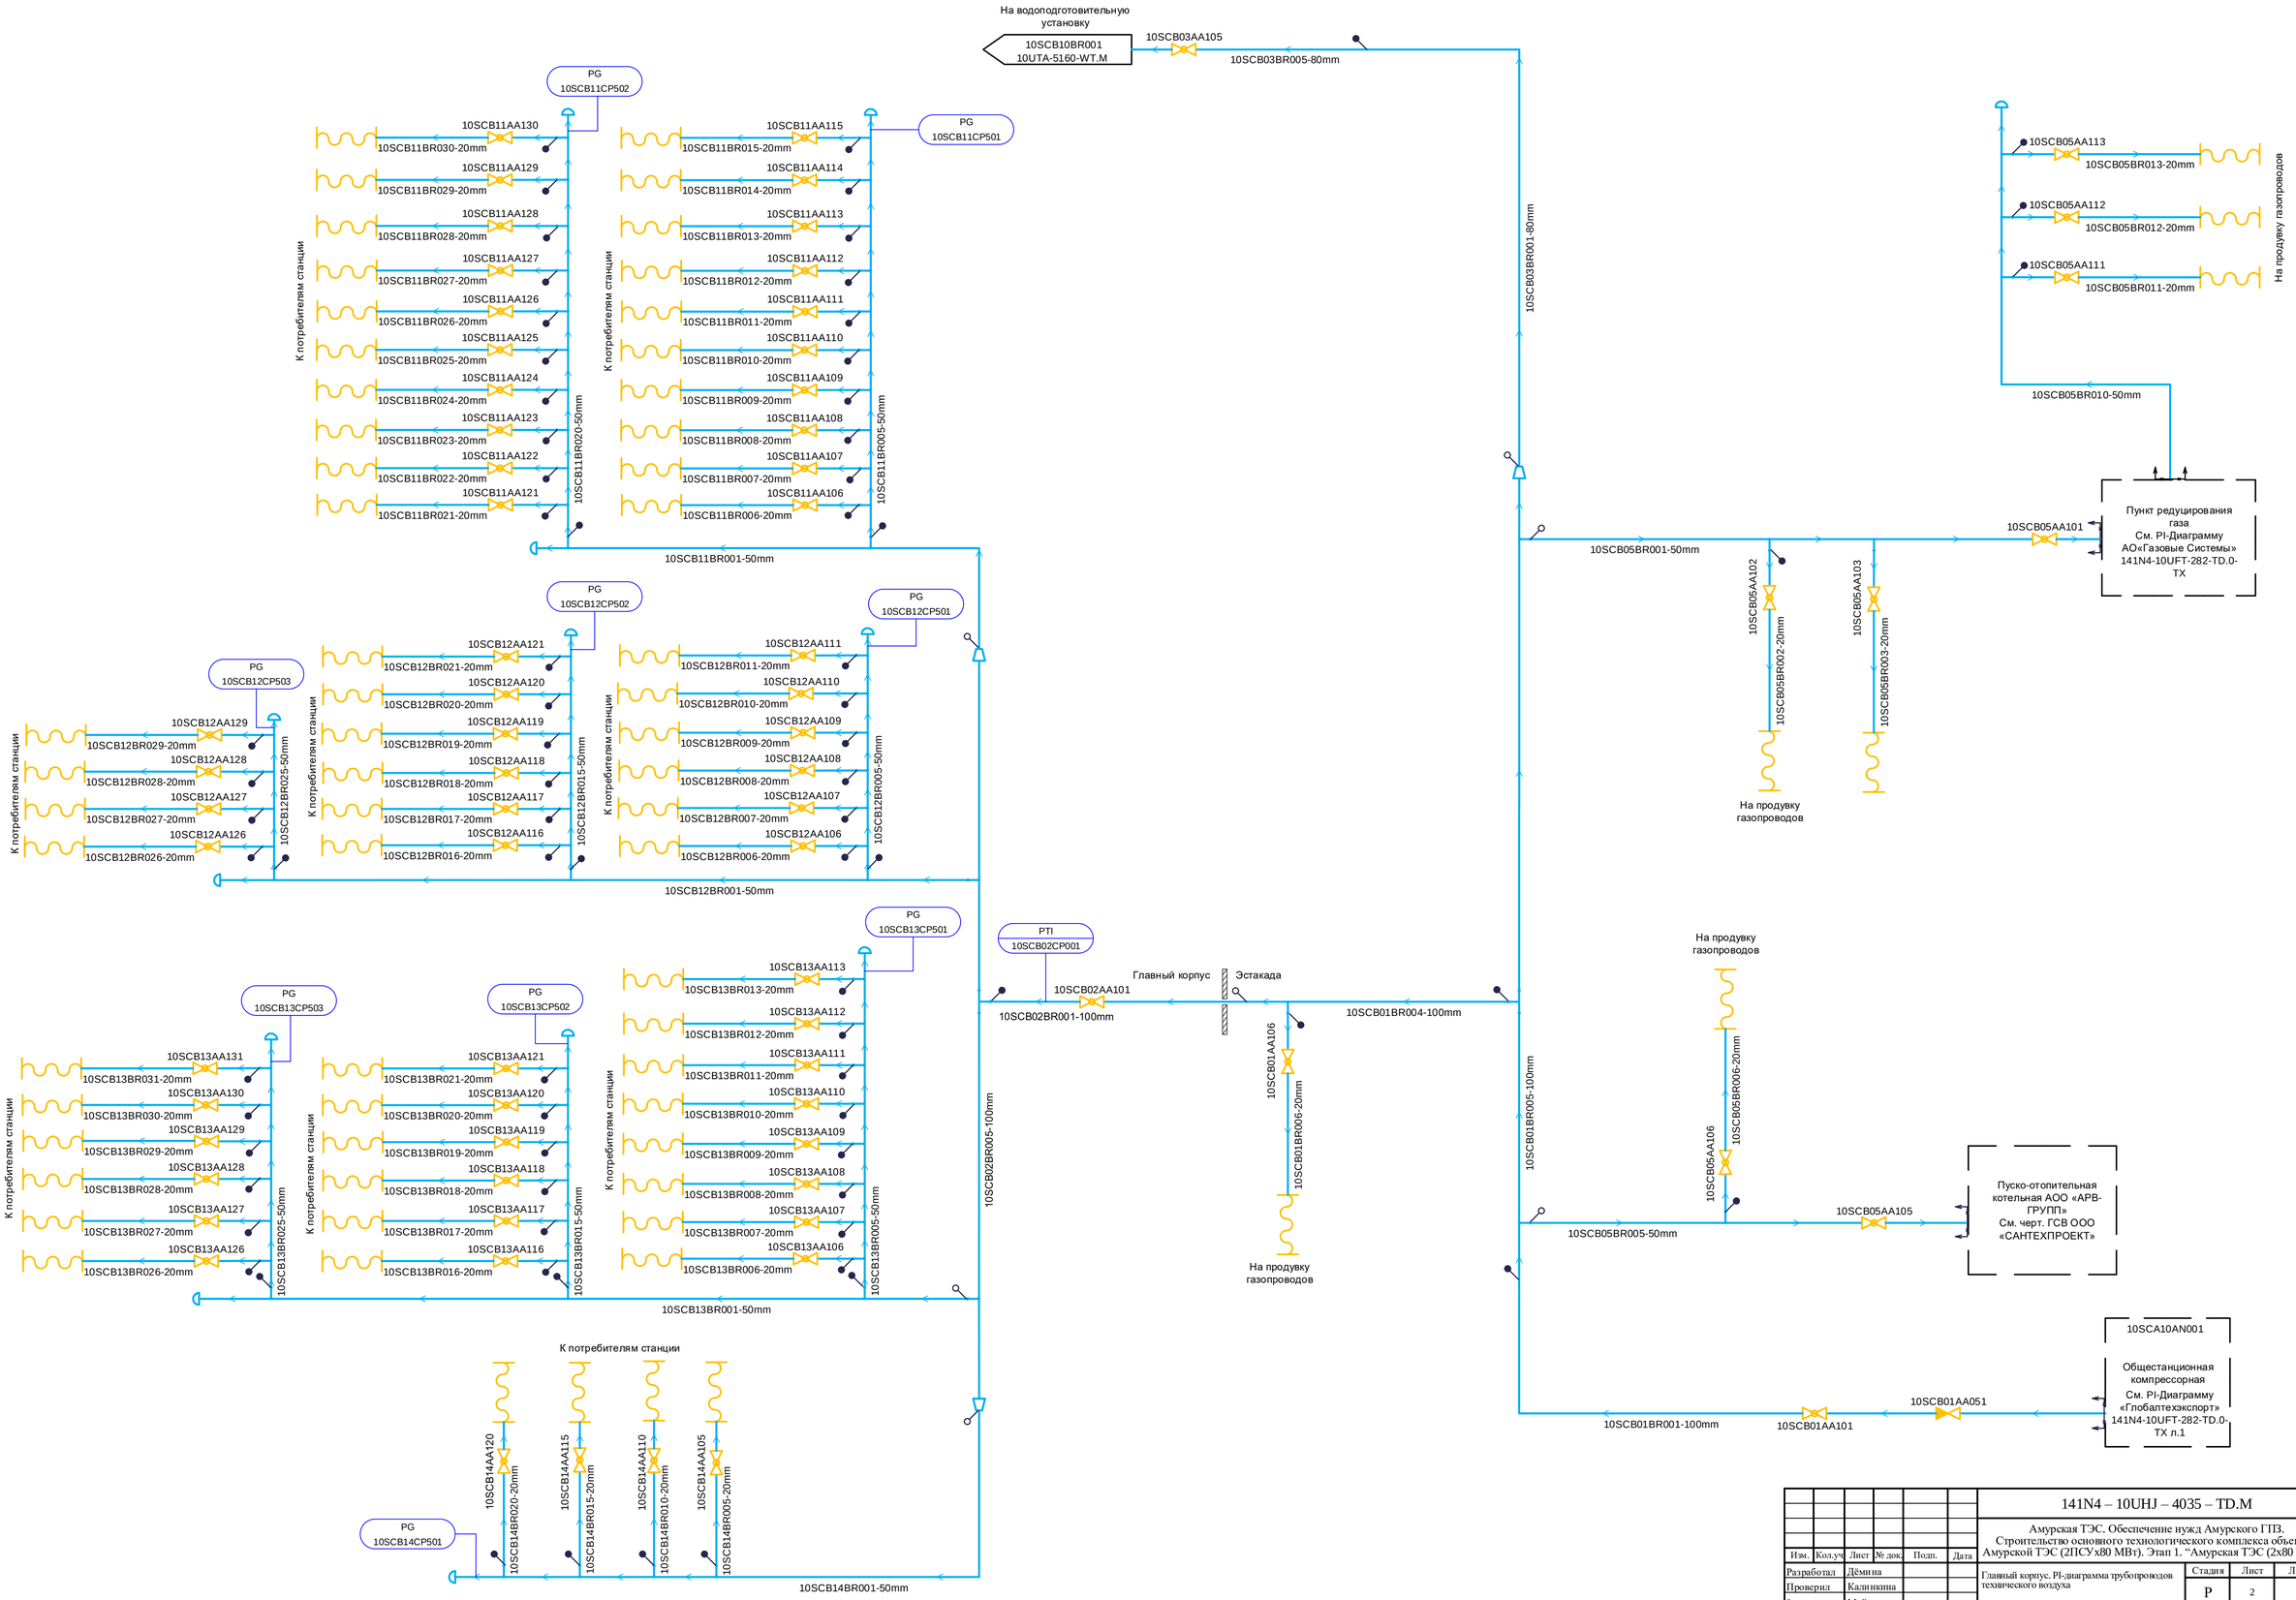

Изм.	Кол.уч	Лист	№ док.	Подп.	Дата	141N4 – 10UHJ – 4035 – TD.M
Разработал		Дёмина				Амурская ТЭС. Обеспечение нужд Амурского ГПЗ. Строительство основного технологического комплекса объектов Амурской ТЭС (2ПГУ×80 МВт). Этап 1. "Амурская ТЭС (2×80 МВт)".
Проверил		Калинкина				Главный корпус. PI-диаграмма трубопроводов технического воздуха
Зам.нач.отд.		Майорова				Стадия: Р; Лист: 2; Листов:
Н. контр.		Астраханцев				PI-диаграмма трубопроводов технического воздуха. Система SCB
						АКЦИОНЕРНОЕ ОБЩЕСТВО ИНСТИТУТ ТЕПЛОЭЛЕКТРОПРОЕКТ г. МОСКВА

Согласовано
ОАСУ
Соболева
Взам. инв. №
Подпись и дата
Инв. № подл.

Формат А1