См. черт. 22.003138
Барнаульский филиал
ОАО ТКЗ «Красный котельщик»
Схема газопровода

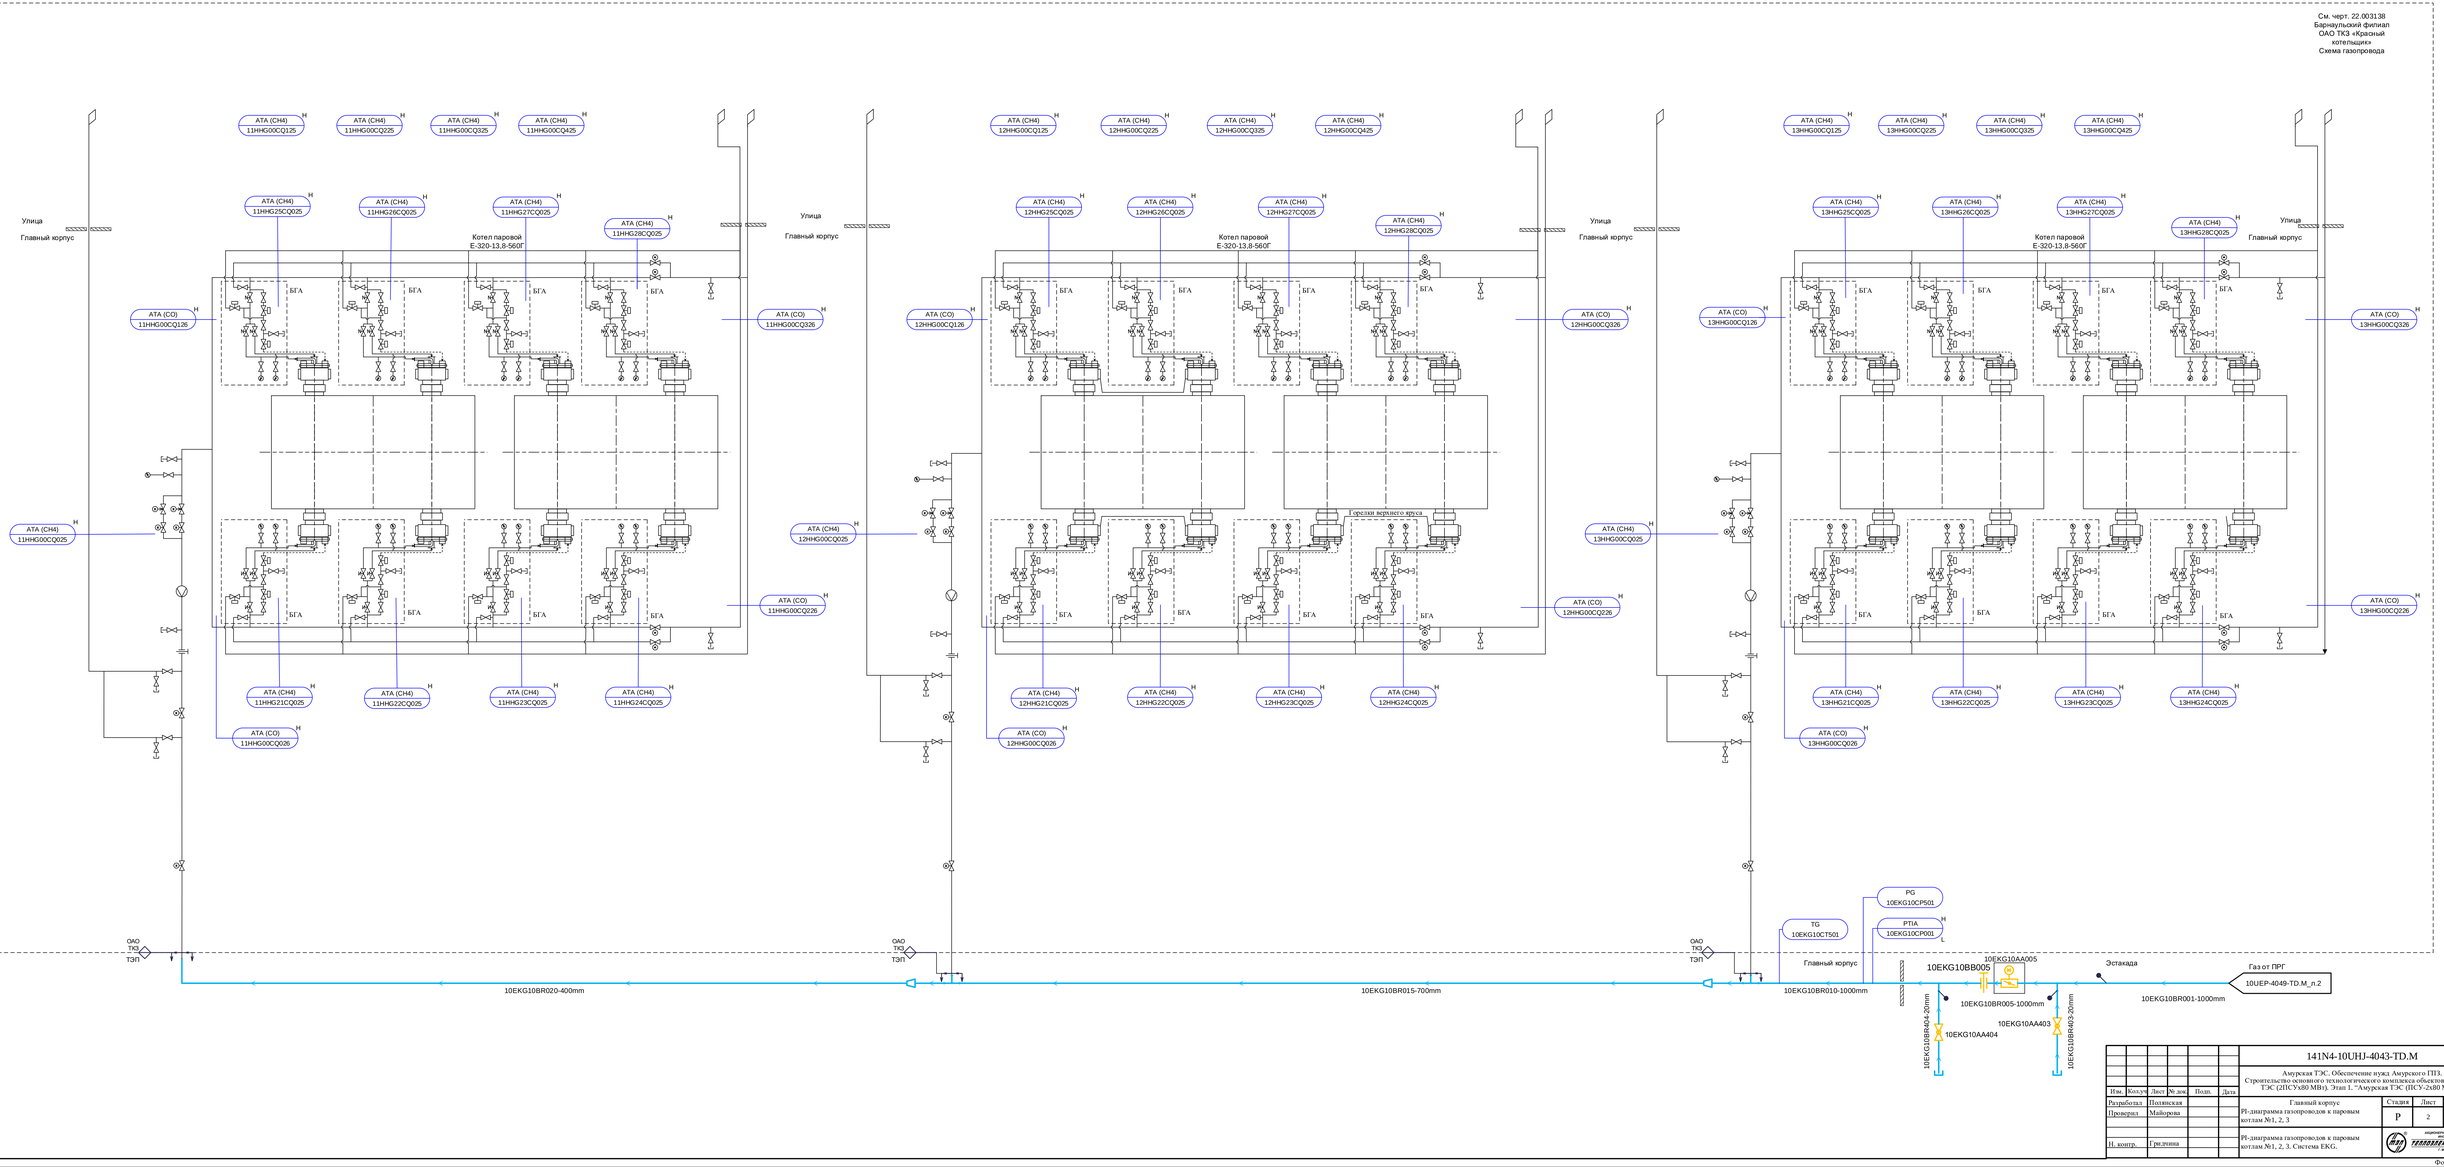

							141N4-10UHJ-4043-TD.M		
							Амурская ТЭС. Обеспечение нужд Амурского ГПЗ. Строительство основного технологического комплекса объектов Амурской ТЭС (2ПСУх80 МВт). Этап 1. "Амурская ТЭС (ПСУ-2х80 МВт)".		
Изм.	Кол.уч.	Лист	№ док.	Подп.	Дата				
Разработал	Полянская					Главный корпус	Стадия	Лист	Листов
Проверил	Майорова					PT-диаграмма газопроводов к паровым котлам №1, 2, 3	Р	2	
Н. контр.	Грядунова					PT-диаграмма газопроводов к паровым котлам №1, 2, 3. Система EKG.	ОАО "ВТИ"		

Согласовано

ОАОУ

Взам. инв. №

Подпись и дата

Инв. № подл.

Формат А2х3