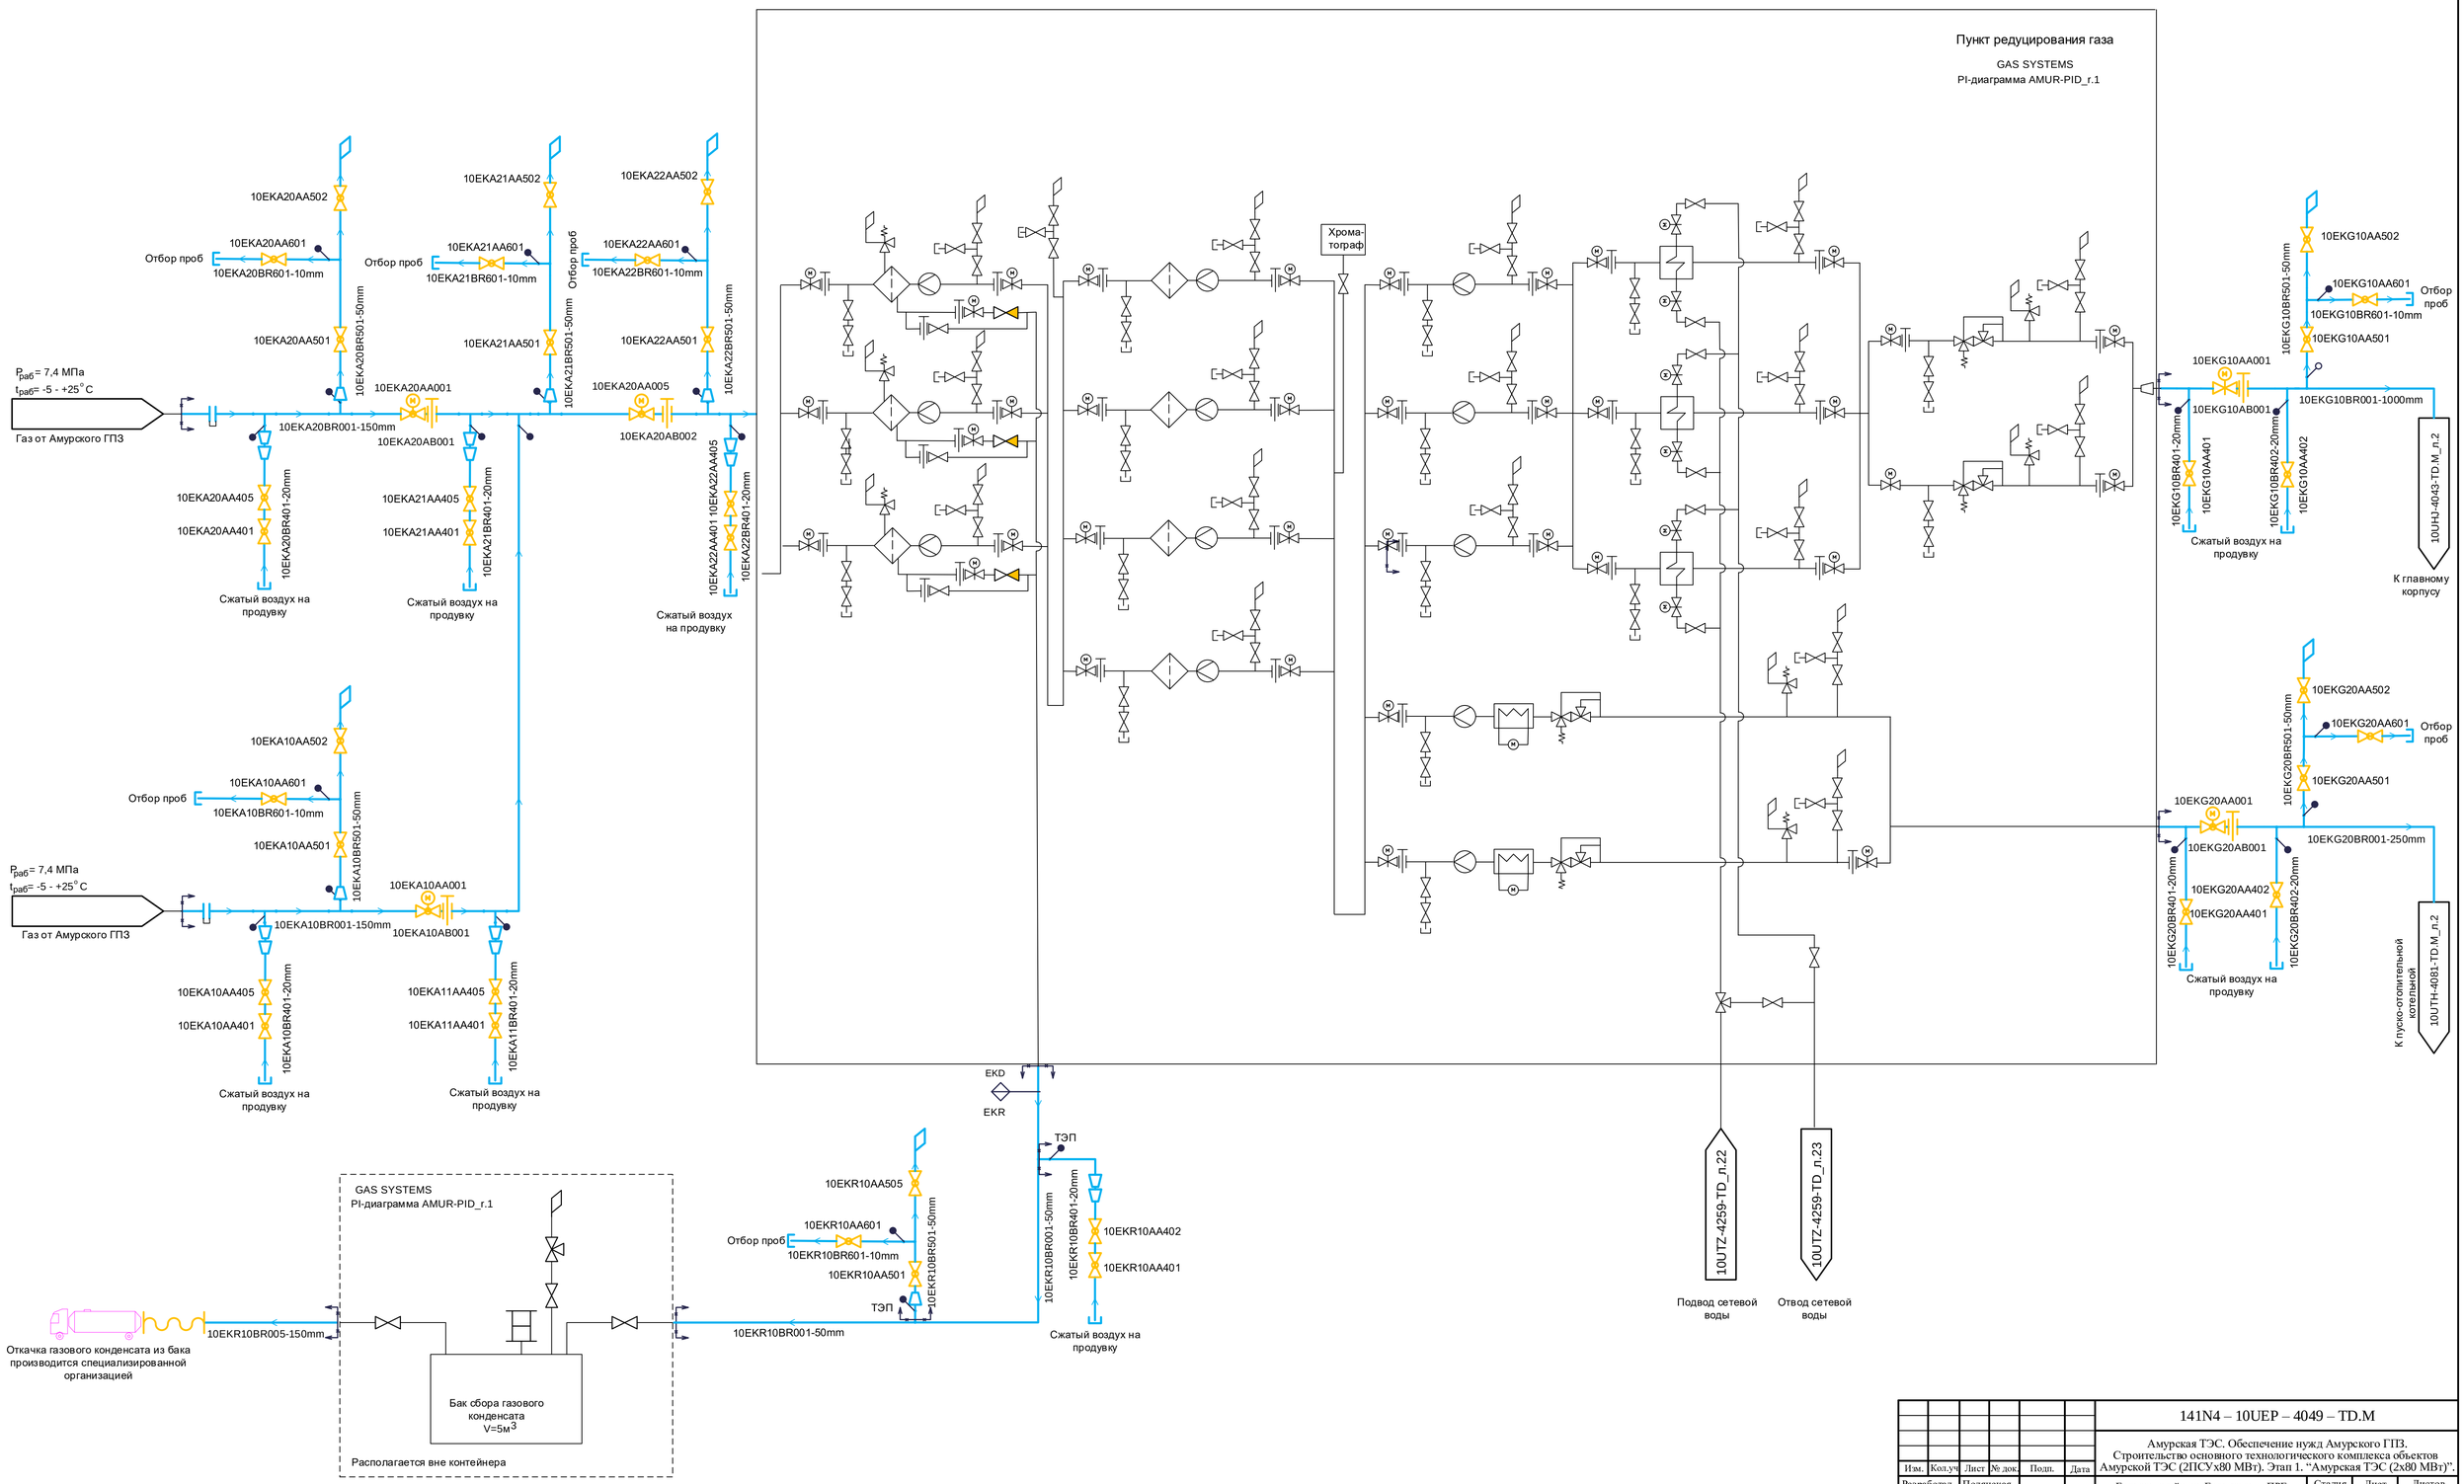

						141N4 – 10UEP – 4049 – TD.M		
Изм.	Кол.уч	Лист	№ док.	Подп.	Дата	Амурская ТЭС. Обеспечение нужд Амурского ГПЗ. Строительство основного технологического комплекса объектов Амурской ТЭС (2ПСУх80 МВт). Этап 1. "Амурская ТЭС (2х80 МВт)".		
Разработал		Полянская				Газовое хозяйство. Газопроводы ПРГ	Стадия	Лист	Листов
Проверил		Майорова				PI-диаграмма газопроводов газового хозяйства	Р	2	
Н. контр.		Гридчина				PI-диаграмма газопроводов газового хозяйства. Система EKA, EKG, EKR	АКЦИОНЕРНОЕ ОБЩЕСТВО ИНСТИТУТ ТЕПЛОЭЛЕКТРОПРОЕКТ г. МОСКВА		

Согласовано

Взам. инв. №

Подпись и дата

Инв. № подл.

Формат А1