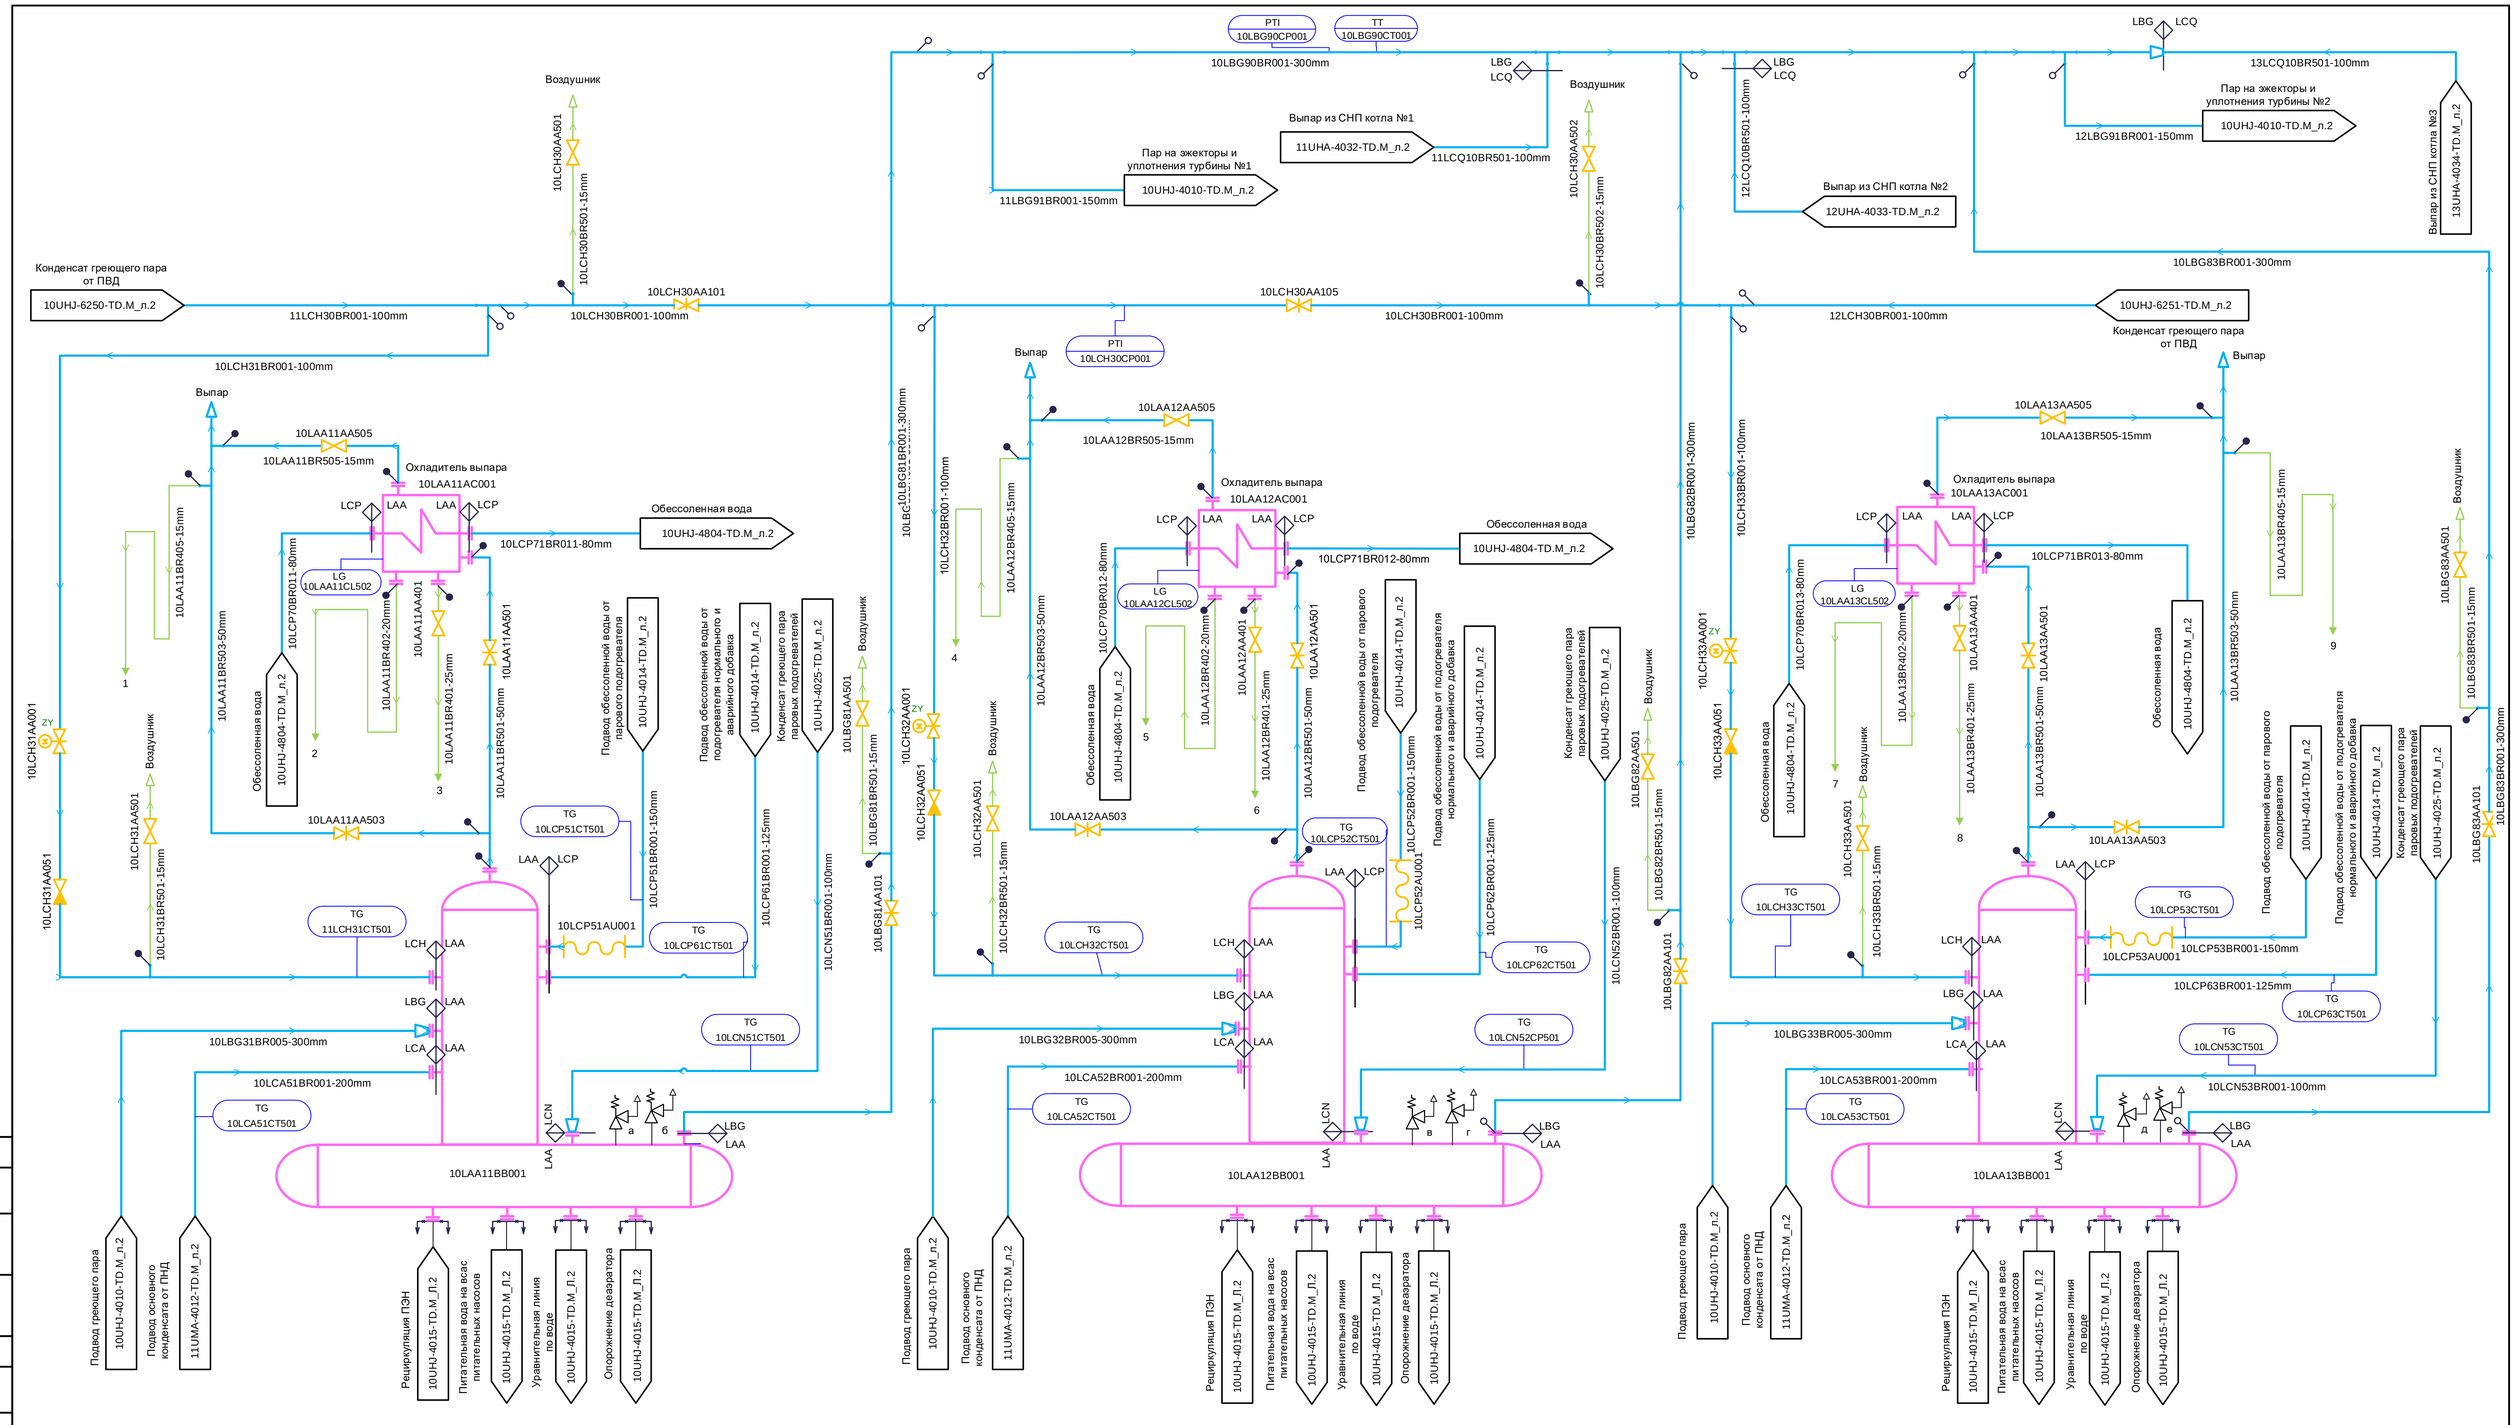

1	-	Зам.	1172-20		12.20	
Изм.	Кол.уч	Лист	№ док.	Подп.	Дата	
Разработал		Дёмина				
Проверил		Калинкина				
Зам.нач.отд.		Майорова				
Н. контр.		Астраханцев				

141N4 – 10UHJ – 4099 – TD.M

Амурская ТЭС. Обеспечение нужд Амурского ГПЗ.
Строительство основного технологического комплекса объектов Амурской ТЭС (2ПСУ×80 МВт). Этап 1. "Амурская ТЭС (ПСУ-2×80 МВт)".

Главный корпус. PI-диаграмма трубопроводов обвязки деаэраторов.

Стадия	Лист	Листов
Р	2	

PI-диаграмма трубопроводов обвязки деаэраторов. Система LBG, LAA, LCA, LAB, LCP, LCN.

АКЦИОНЕРНОЕ ОБЩЕСТВО ВНИПИЭТ ТЕПЛОЭЛЕКТРОПРОЕКТ Г. МОСКВА

Согласовано
ОАСУ Собкина
Взам. инв. №
Подпись и дата
Инв. № подл.

Формат А1