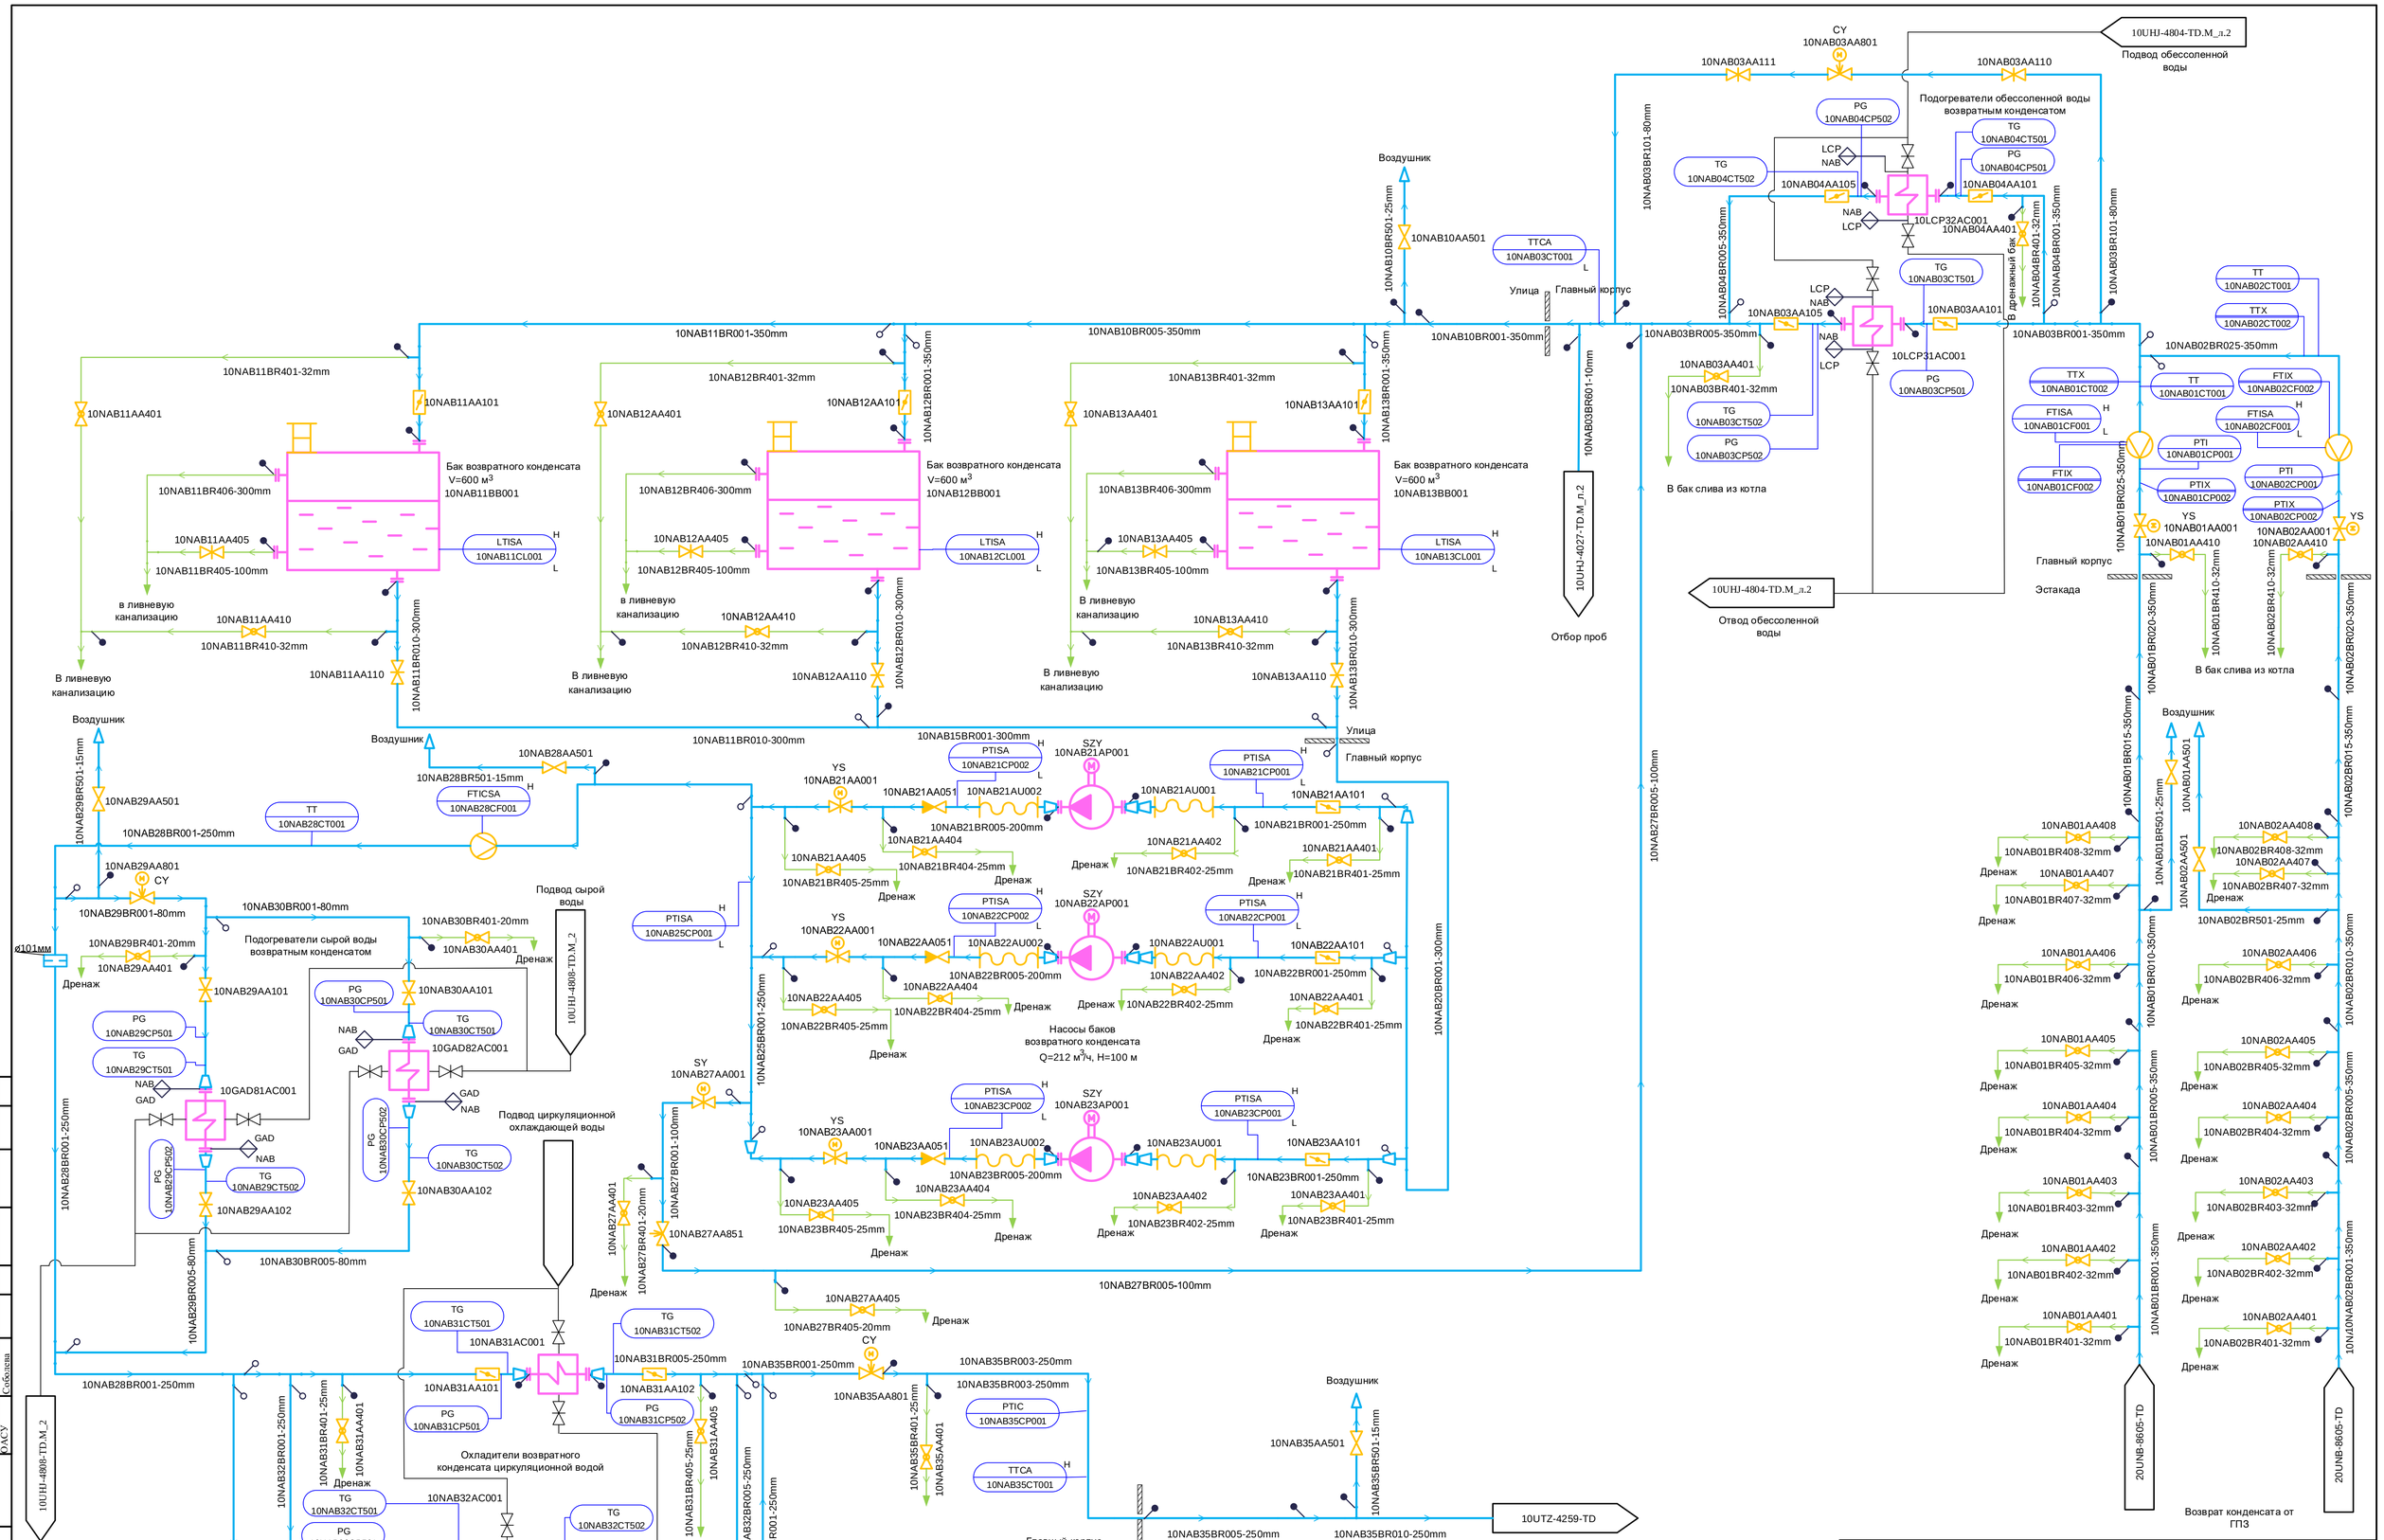

1	-	Зам	1102-19			
Изм.	Кол.уч	Лист	№ док.	Подп.	Дата	

141N4-10UHJ-4802-TD.M

Амурская ТЭС. Обеспечение нужд Амурского ГПЗ. Строительство основного технологического комплекса объектов Амурской ТЭС (2ПСУх80 МВт). Этап 1. "Амурская ТЭС (2х80 МВт)".

Разработал	Полянская	
Проверил	Калинкина	
Зам.нач.отд.	Майорова	
Н. контр.	Гридчина	

Главный корпус.
PI-диаграмма трубопроводов возвратного конденсата

PI-диаграмма трубопроводов возвратного конденсата. Система NAB

Стадия	Лист	Листов
Р	2	

АКЦИОНЕРНОЕ ОБЩЕСТВО ИНСТИТУТ ТЕПЛОЭЛЕКТРОПРОЕКТ г. МОСКВА

Согласовано
ОАСУ
Собулова

Взам. инв. №
Подпись и дата
Инв. № подл.

Формат А1