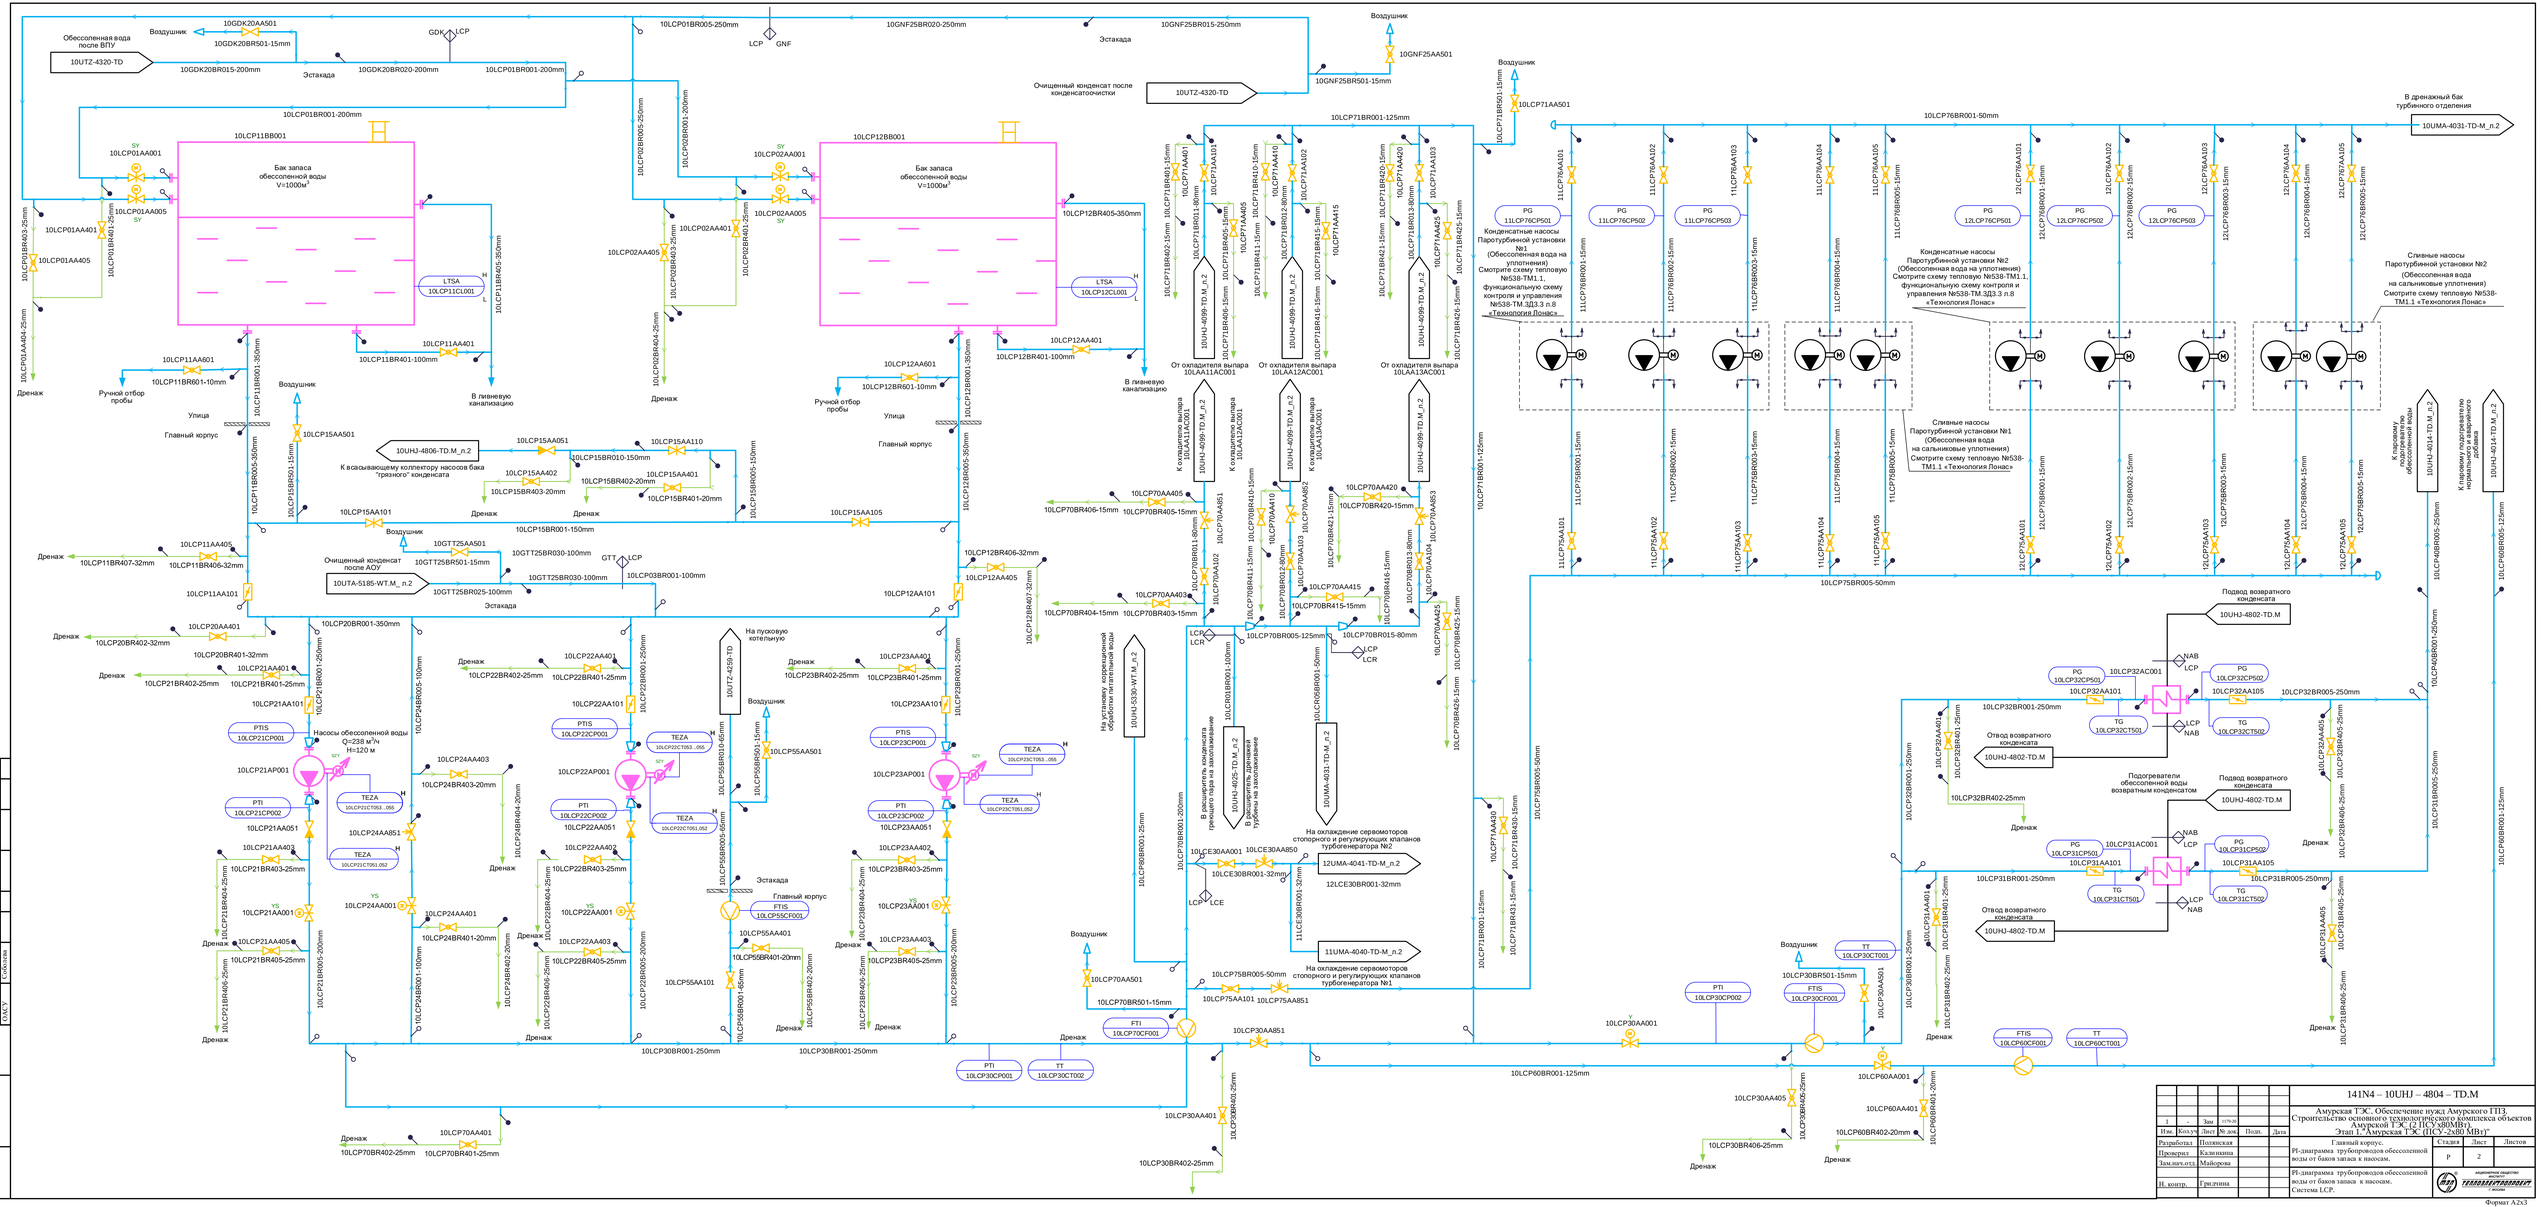
Обессоленная вода после ВПУ
10UTZ-4320-TD
Воздушник
10GDK20AA501
10GDK20BR501-15mm
10GDK20BR015-200mm
Эстакада
10GDK20BR020-200mm
10LCP01BR001-200mm
10LCP01BR001-200mm
10LCP01BR005-350mm
10LCP02BR001-200mm
10LCP02BR005-350mm
10LCP01BR005-350mm
10LCP11BB001
Бак запаса обессоленной воды V=1000м³
10LCP12BB001
Бак запаса обессоленной воды V=1000м³
10LCP12BR405-350mm
10LCP11BR405-350mm
LTSA 10LCP11CL001
LTSA 10LCP12CL001
10LCP11AA401
10LCP11BR401-100mm
10LCP12AA401
10LCP12BR401-100mm
10LCP11AA601
10LCP11BR601-10mm
10LCP12AA601
10LCP12BR601-10mm
Ручной отбор пробы
Дренаж
Улица
Главный корпус
В ливневую канализацию
10UHJ-4806-TD.M_n.2
К всасывающему коллектору насосов бака "грязного" конденсата
10LCP15AA051
10LCP15AA110
10LCP15BR010-150mm
10LCP15BR402-20mm
10LCP15AA401
10LCP15BR401-20mm
10LCP15BR403-20mm
10LCP15AA501
10LCP15AA101
10LCP15BR001-150mm
10LCP15BR005-150mm
10LCP15AA105
10LCP11AA405
10LCP11BR406-32mm
10LCP11BR407-32mm
Очищенный конденсат после АОУ
10UTA-5185-WT.M_ n.2
10GTT25AA501
10GTT25BR030-100mm
10GTT25BR501-15mm
10GTT25BR025-100mm
10LCP03BR001-100mm
10LCP12BR406-32mm
10LCP12AA405
10LCP12AA101
10LCP20BR001-350mm
10LCP20AA401
10LCP20BR402-32mm
10LCP20BR401-32mm
10LCP21AA401
10LCP21BR402-25mm
10LCP21BR401-25mm
10LCP21AA101
10LCP21BR001-250mm
10LCP22AA401
10LCP22BR402-25mm
10LCP22BR401-25mm
10LCP22AA101
10LCP22BR001-250mm
10LCP23AA401
10LCP23BR402-25mm
10LCP23BR401-25mm
10LCP23AA101
10LCP23BR001-250mm
10LCP24BR005-100mm
10LCP24AA403
10LCP24BR403-20mm
10LCP24BR404-20mm
10LCP24AA851
10LCP24AP001
10LCP21AP001
PTIS 10LCP21CP001
Насосы обессоленной воды Q=238 м³/ч H=120 м
PTI 10LCP21CP002
TEZA 10LCP21CT053...056
TEZA 10LCP21CT051,052
10LCP21AA051
10LCP21AA403
10LCP21BR403-25mm
10LCP21AA001
10LCP21AA405
10LCP21BR405-25mm
10LCP21BR404-25mm
10LCP21BR406-25mm
10LCP21BR005-200mm
10LCP24AA001
10LCP24AA401
10LCP24BR401-20mm
10LCP24BR402-20mm
10LCP24BR001-100mm
10LCP22AP001
PTI 10LCP22CP002
10LCP22AA051
10LCP22AA402
10LCP22BR403-25mm
10LCP22AA001
10LCP22AA403
10LCP22BR405-25mm
10LCP22BR404-25mm
10LCP22BR406-25mm
10LCP22BR005-200mm
10LCP55BR010-65mm
10LCP55BR501-15mm
10UTZ-4259-TD
На пусковую котельную
10LCP55AA501
Эстакада
Главный корпус
FTIS 10LCP55CF001
10LCP55AA401
10LCP55BR401-20mm
10LCP55BR402-20mm
10LCP55AA101
10LCP58BR001-65mm
10LCP58BR402-20mm
10LCP23AP001
PTI 10LCP23CP002
10LCP23AA051
10LCP23AA402
10LCP23BR403-25mm
10LCP23AA001
10LCP23AA403
10LCP23BR405-25mm
10LCP23BR404-25mm
10LCP23BR406-25mm
10LCP23BR005-200mm
10LCP30BR001-250mm
10LCP30BR001-250mm
PTI 10LCP30CP001
TT 10LCP30CT002
10LCP70AA401
10LCP70BR402-25mm
10LCP70BR401-25mm
10LCP02AA001
10LCP02AA005
10LCP02AA401
10LCP02AA405
10LCP02BR401-25mm
10LCP02BR403-25mm
10LCP02BR404-25mm
10LCP12AA601
10LCP12BR601-10mm
10LCP12BR001-350mm
10LCP12BR005-350mm
10LCP12AA101
10LCP12BR407-32mm
10LCP12BR407-32mm
10LCP01BR005-250mm
10LCP01BR005-250mm
10LCP01BR001-250mm
10LCP01AA001
10LCP01AA005
10LCP01AA401
10LCP01AA405
10LCP01BR402-25mm
10LCP01BR401-25mm
10LCP01BR403-25mm
10LCP01AA404-25mm
10LCP01BR404-25mm
10LCP01BR406-25mm
10LCP01BR005-250mm
10LCP01BR001-125mm
10LCP71BR001-125mm
10LCP71BR501-15mm
10LCP71AA501
10LCP71BR401-15mm
10LCP71AA401
10LCP71BR011-80mm
10LCP71AA101
10LCP71BR405-15mm
10LCP71AA405
10LCP71BR411-15mm
10LCP71AA411
10LCP71BR012-80mm
10LCP71AA102
10LCP71BR410-15mm
10LCP71AA410
10LCP71BR416-15mm
10LCP71AA416
10LCP71BR415-15mm
10LCP71AA415
10LCP71BR421-15mm
10LCP71AA421
10LCP71BR013-80mm
10LCP71AA103
10LCP71BR425-15mm
10LCP71AA425
10UHJ-4099-TD.M_n.2
От охладителя выпара 10LAA11AC001
От охладителя выпара 10LAA12AC001
От охладителя выпара 10LAA13AC001
К охладителю выпара 10LAA11AC001
К охладителю выпара 10LAA12AC001
К охладителю выпара 10LAA13AC001
10LCP70AA405
10LCP70BR405-15mm
10LCP70BR406-15mm
10LCP70BR011-80mm
10LCP70AA851
10LCP70AA102
10LCP70BR411-15mm
10LCP70AA411
10LCP70BR410-15mm
10LCP70AA410
10LCP70AA852
10LCP70AA103
10LCP70BR012-80mm
10LCP70BR421-15mm
10LCP70AA420
10LCP70BR420-15mm
10LCP70AA853
10LCP70AA104
10LCP70BR013-80mm
10LCP70BR416-15mm
10LCP70AA415
10LCP70BR415-15mm
10LCP70AA425
10LCP70BR425-15mm
10LCP70BR426-15mm
10LCP70AA403
10LCP70BR403-15mm
10LCP70BR404-15mm
10LCP70BR005-125mm
10LCP70BR015-80mm
LCP LCR
LCP LCE
10LCE30AA001
10LCE30AA850
10LCE30BR001-32mm
12LCE30BR001-32mm
11LCE30BR001-32mm
10LCP70BR001-200mm
10LCP70BR001-125mm
10LCP70BR501-15mm
10LCP70AA501
10LCP70CF001
FTI 10LCP70CF001
10UHJ-5130-WT.M_n.2
На отгонку кислородной обработки питательной воды
10UHJ-4025-TD.M_n.2
В расширитель дренажей турбины на теплоснабжение
10UMA-4031-TD-M_n.2
В расширитель дренажей турбины на теплоснабжение
12UMA-4041-TD-M_n.2
На охлаждение сервомоторов стопорного и регулирующих клапанов турбогенератора №2
11UMA-4040-TD-M_n.2
На охлаждение сервомоторов стопорного и регулирующих клапанов турбогенератора №1
10LCP75BR005-50mm
10LCP75AA101
10LCP75AA851
10LCP30AA851
10LCP30AA401
10LCP30BR402-25mm
10LCP30BR401-25mm
10LCP71BR601-125mm
10LCP71BR601-15mm
10LCP71AA501
10LCP71BR439-15mm
10LCP71AA439
10LCP71BR431-15mm
10LCP71BR003-125mm
10LCP76BR001-50mm
10LCP76AA101
10LCP76AA102
10LCP76AA103
10LCP76AA104
10LCP76AA105
10LCP76BR001-15mm
10LCP76BR002-15mm
10LCP76BR003-15mm
10LCP76BR004-15mm
10LCP76BR005-15mm
PG 11LCP76CP501
PG 11LCP76CP502
PG 11LCP76CP503
PG 12LCP76CP501
PG 12LCP76CP502
PG 12LCP76CP503
12LCP76AA101
12LCP76AA102
12LCP76AA103
12LCP76AA104
12LCP76AA105
12LCP76BR001-15mm
12LCP76BR002-15mm
12LCP76BR003-15mm
12LCP76BR004-15mm
12LCP76BR005-15mm
Конденсатные насосы Паротурбинной установки №1 (Обессоленная вода на уплотнения) Смотрите схему тепловую №538-ТМ.1.1, функциональную схему контроля и управления №538-ТМ.ЗД3.3 л.8 «Технология Понас»
Конденсатные насосы Паротурбинной установки №2 (Обессоленная вода на уплотнения) Смотрите схему тепловую №538-ТМ.1.1, функциональную схему контроля и управления №538-ТМ.ЗД3.3 л.8 «Технология Понас»
Сливные насосы Паротурбинной установки №1 (Обессоленная вода на сальниковые уплотнения) Смотрите схему тепловую №538-ТМ.1.1 «Технология Понас»
Сливные насосы Паротурбинной установки №2 (Обессоленная вода на сальниковые уплотнения) Смотрите схему тепловую №538-ТМ.1.1 «Технология Понас»
В дренажный бак турбинного отделения
10UMA-4031-TD-M_n.2
10LCP75BR005-50mm
10LCP75AA101
10LCP75AA102
10LCP75AA103
10LCP75AA104
10LCP75AA105
12LCP75AA101
12LCP75AA102
12LCP75AA103
12LCP75AA104
12LCP75AA105
12LCP75BR001-15mm
12LCP75BR002-15mm
12LCP75BR003-15mm
12LCP75BR004-15mm
12LCP75BR005-15mm
К коллектору подогревателя обессоленной воды
10UHJ-4014-TD.M_n.2
К коллектору подогревателя нормального и аварийного дренажа
10UHJ-4014-TD-M_n.2
10LCP48BR005-250mm
10LCP60BR005-125mm
10LCP60BR001-125mm
10LCP60AA001
10LCP60AA401
10LCP60BR402-20mm
10LCP60BR401-20mm
10LCP30AA001
10LCP30AA405
10LCP30BR405-25mm
10LCP30BR406-25mm
TT 10LCP30CT001
PTI 10LCP30CP002
FTIS 10LCP30CF001
10LCP30BR501-15mm
10LCP30AA501
FTIS 10LCP60CF001
TT 10LCP60CT001
Подвод возвратного конденсата
10UHJ-4802-TD.M
PG 10LCP32CP501
10LCP32AC001
PG 10LCP32CP502
10LCP32AA105
10LCP32BR005-250mm
10LCP32AA101
TG 10LCP32CT501
TG 10LCP32CT502
10LCP32BR001-250mm
Отвод возвратного конденсата
10UHJ-4802-TD.M
10LCP32BR402-25mm
10LCP32AA401
10LCP32BR401-25mm
10LCP32BR005-250mm
10LCP32BR406-25mm
10LCP32AA405
Подогреватели обессоленной воды возвратным конденсатом
Подвод возвратного конденсата
10UHJ-4802-TD.M
PG 10LCP31CP501
10LCP31AC001
PG 10LCP31CP502
10LCP31AA101
10LCP31AA105
10LCP31BR001-250mm
10LCP31BR005-250mm
TG 10LCP31CT501
TG 10LCP31CT502
Отвод возвратного конденсата
10UHJ-4802-TD.M
10LCP31AA401
10LCP31BR401-25mm
10LCP31BR001-250mm
10LCP31BR402-25mm
10LCP31BR406-25mm
10LCP31AA405
10LCP31BR005-250mm
10LCP31BR406-25mm
Дренаж
Воздушник
Эстакада
Улица
Главный корпус
Согласовано
Взам. инв. №
Подпись и дата
Инв. № подл.
Изм. Кол.уч. Лист № док. Подп. Дата
Разработал Полянская
Проверил Калинина
Зам.нач.отд. Майорова
Н. контр. Грядунова
Главный корпус.
Стадия Лист Листов
Р 2
Р1-диаграмма трубопроводов обессоленной воды от баков запаса к насосам.
Р1-диаграмма трубопроводов обессоленной воды от баков запаса к насосам.. Система LCP.
141N4 – 10UHJ – 4804 – TD.M
Амурская ТЭС. Обеспечение нужд Амурского ГПЗ. Строительство основного технологического комплекса объектов Амурской ТЭС (2 ПСУ х180МВт). Этап 1. "Амурская ТЭС (ПСУ-2х80 МВт)"
Формат А2х3