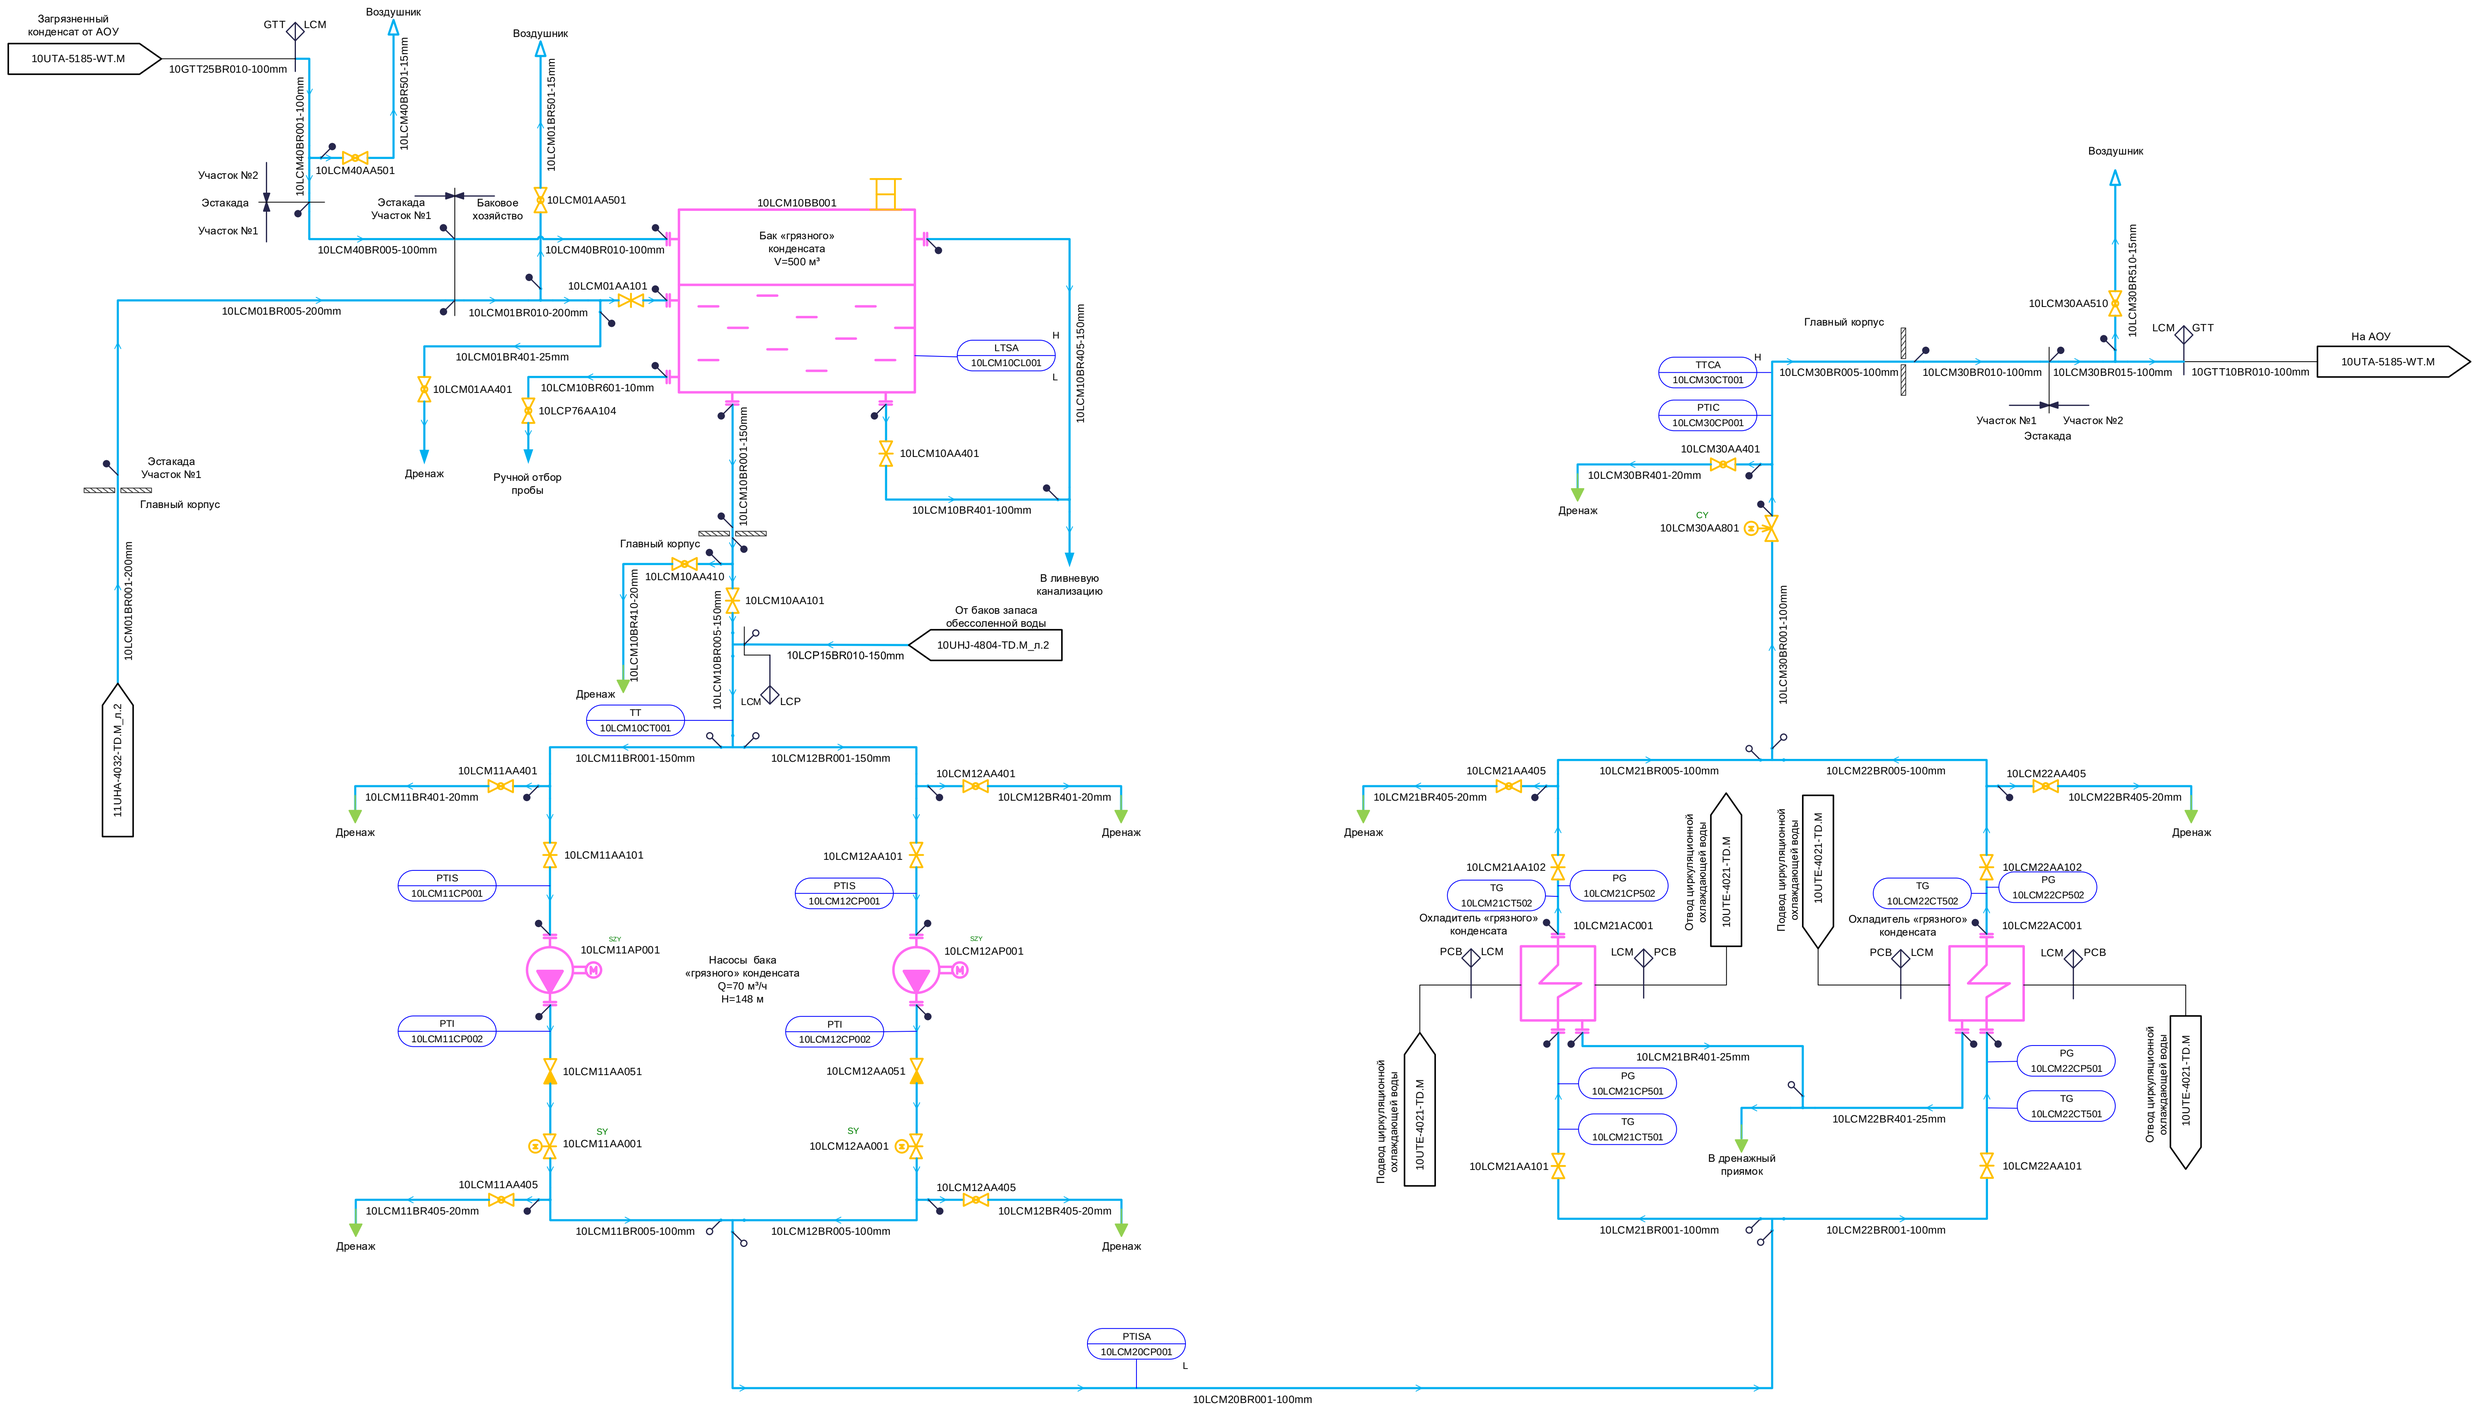

1	-	Зам	1102-19			
Изм.	Кол.уч	Лист	№ док.	Подп.	Дата	

141N4 – 10UHJ – 4806 – TD.M

Амурская ТЭС. Обеспечение нужд Амурского ГПЗ. Строительство основного технологического комплекса объектов Амурской ТЭС (2 ПСУ х80МВт). Этап 1."Амурская ТЭС (ПСУ-2х80 МВт)"

Разработал	Брылева	
Проверил	Калинкина	
Зам.нач.отд.	Майорова	
Н. контр.	Гридчина	

Главный корпус. PI-диаграмма трубопроводов «грязного» конденсата.

Стадия	Лист	Листов
Р	2	

PI-диаграмма трубопроводов «грязного» конденсата. Система LCM.

АКЦИОНЕРНОЕ ОБЩЕСТВО ИНСТИТУТ ТЕПЛОЭЛЕКТРОПРОЕКТ г. МОСКВА

Согласовано: ОАСУ Соболева

Взам. инв. №

Подпись и дата

Инв. № подл.

Формат А1