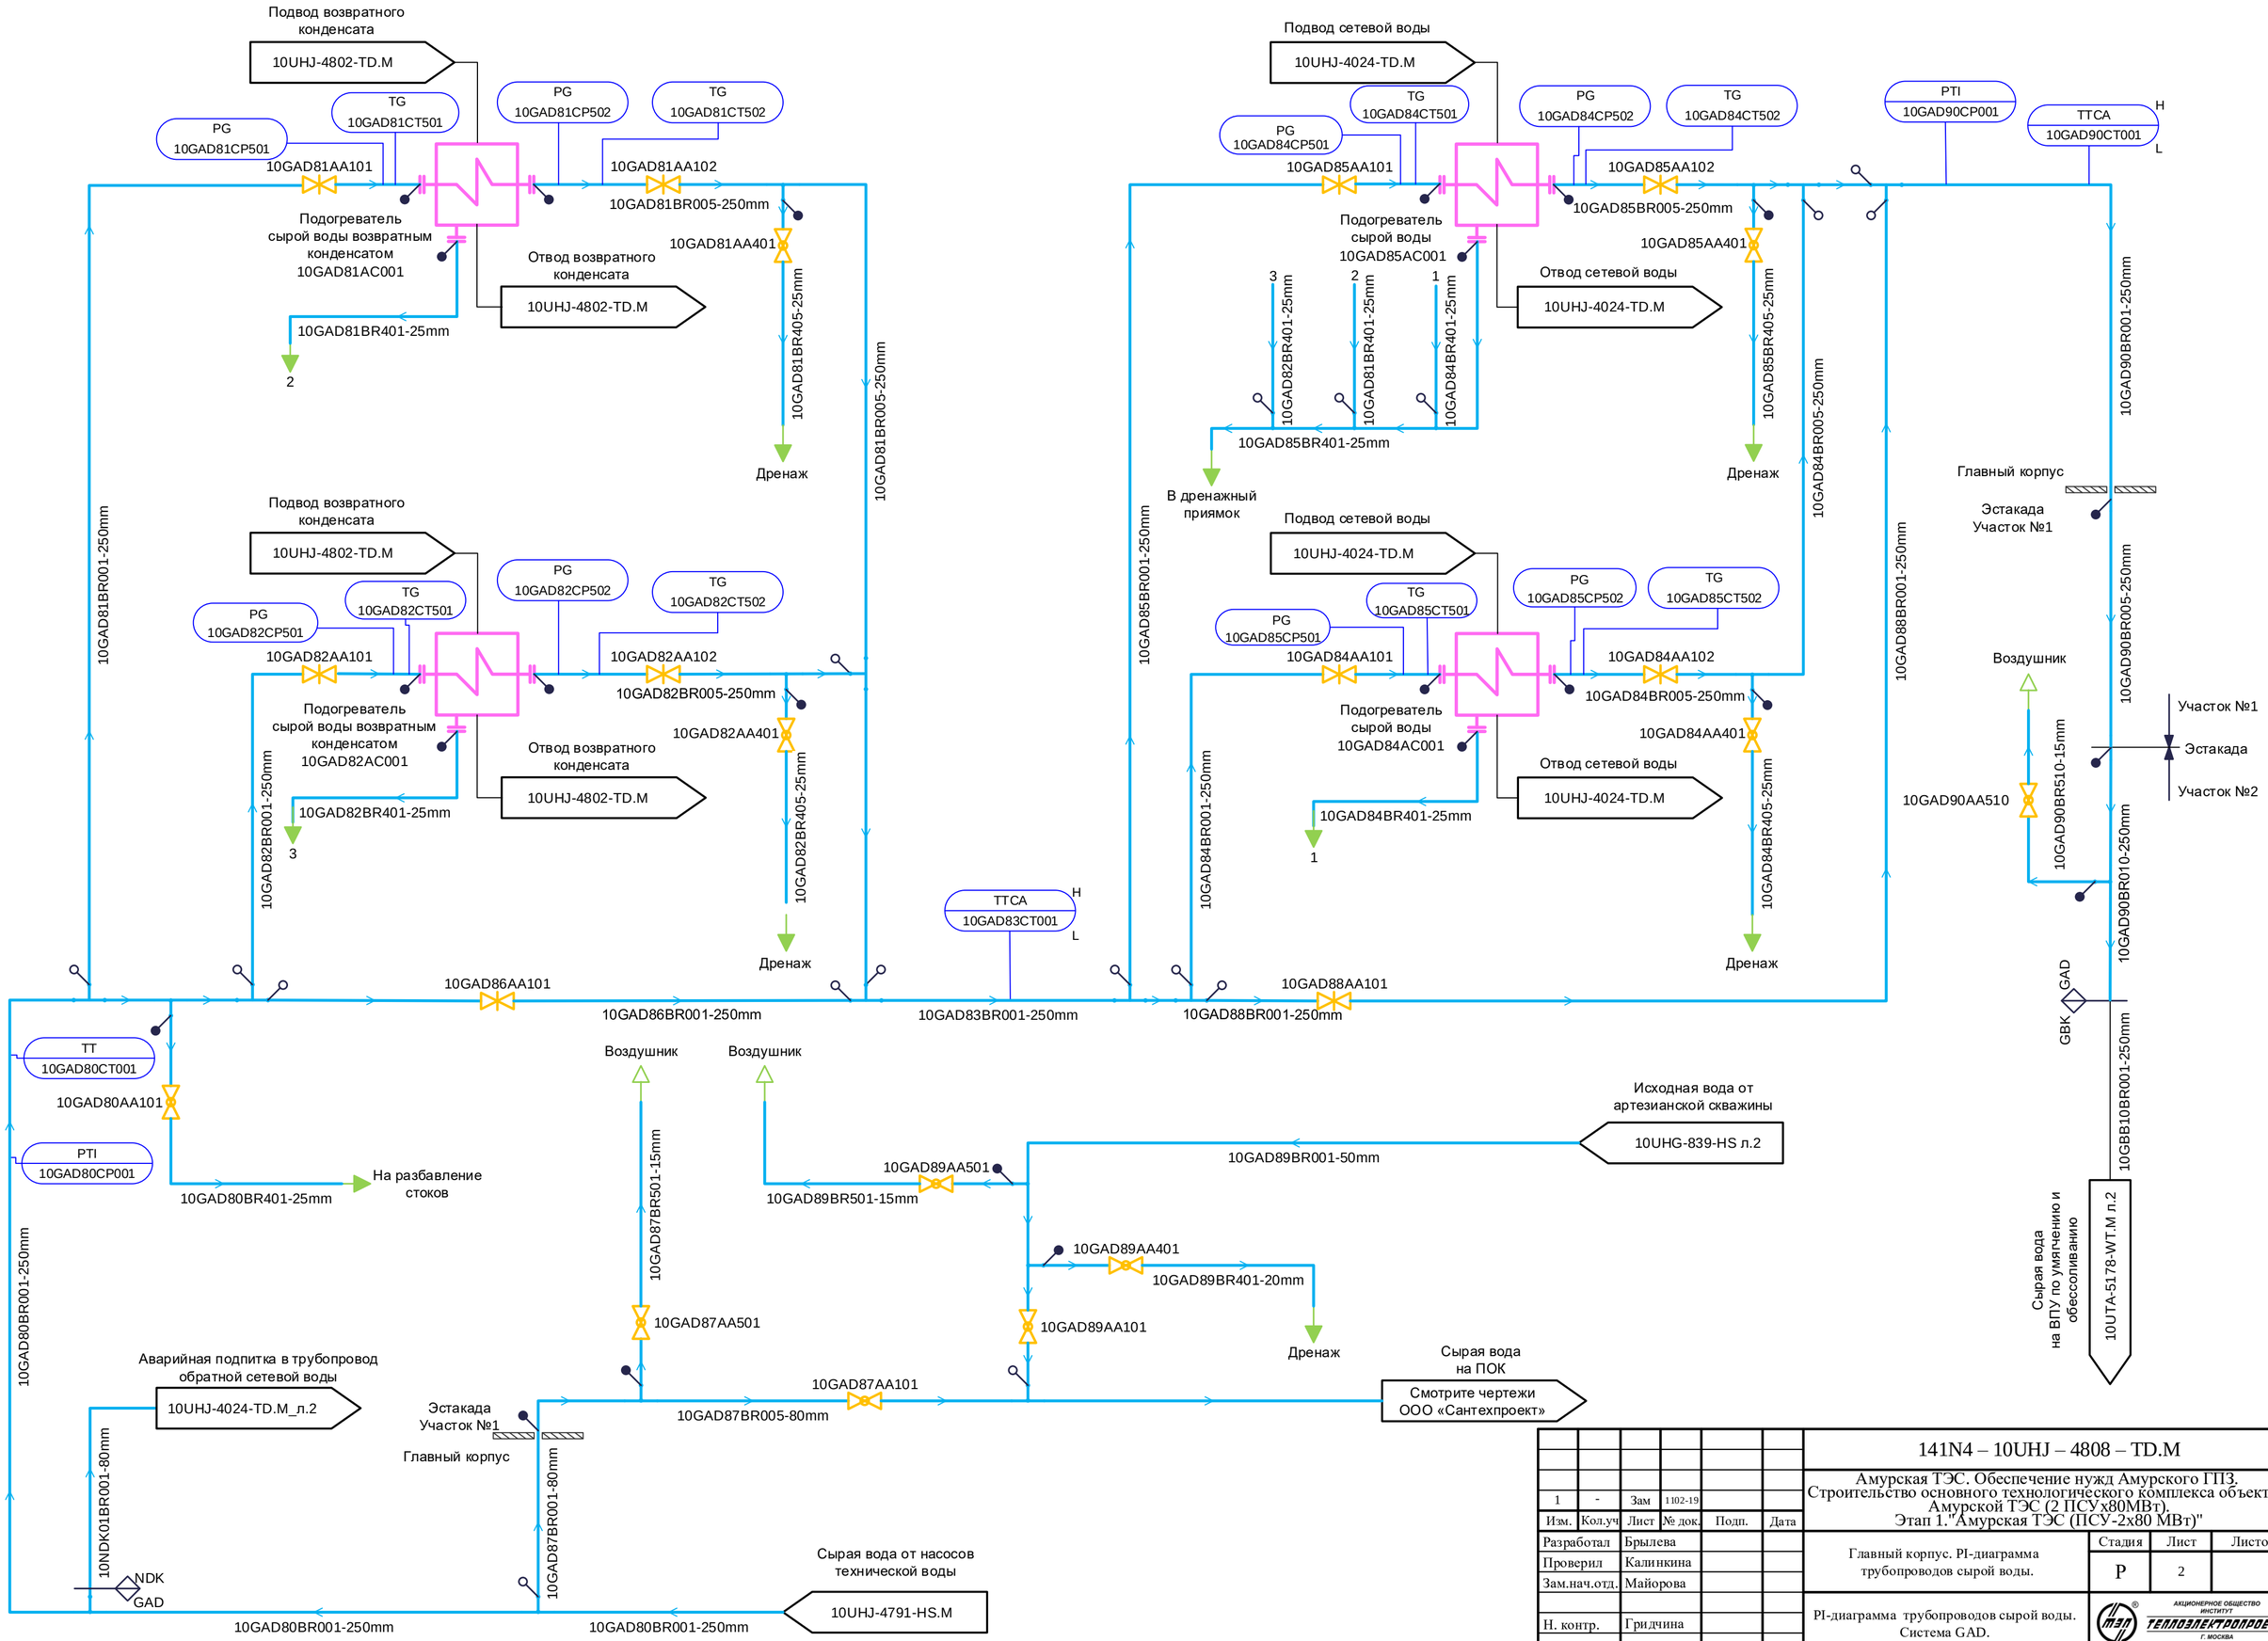

Изм.	Кол.уч	Лист	№ док.	Подп.	Дата
1	-	Зам	1102-19		

Разработал	Брылева	
Проверил	Калинкина	
Зам.нач.отд.	Майорова	
Н. контр.	Гридчина	

141N4 – 10UHJ – 4808 – TD.M

Амурская ТЭС. Обеспечение нужд Амурского ГПЗ. Строительство основного технологического комплекса объектов Амурской ТЭС (2 ПСУх80МВт). Этап 1."Амурская ТЭС (ПСУ-2х80 МВт)"

Главный корпус. PI-диаграмма трубопроводов сырой воды.

Стадия	Лист	Листов
Р	2	

PI-диаграмма трубопроводов сырой воды. Система GAD.

АКЦИОНЕРНОЕ ОБЩЕСТВО ИНСТИТУТ ТЕПЛОЭЛЕКТРОПРОЕКТ Г. МОСКВА

Согласовано

ОЛСУ Соболева

Взам. инв. №

Подпись и дата

Инв. № подл.

Формат А2