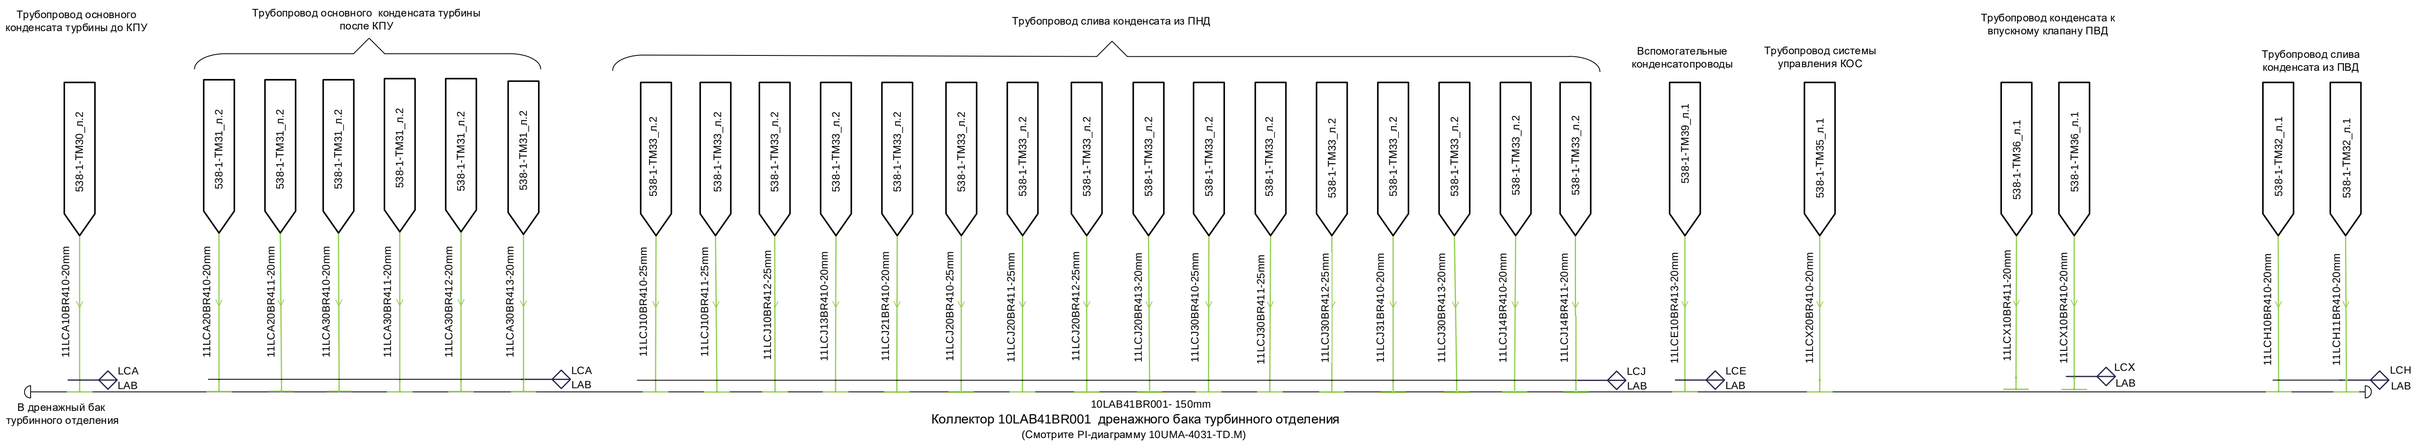

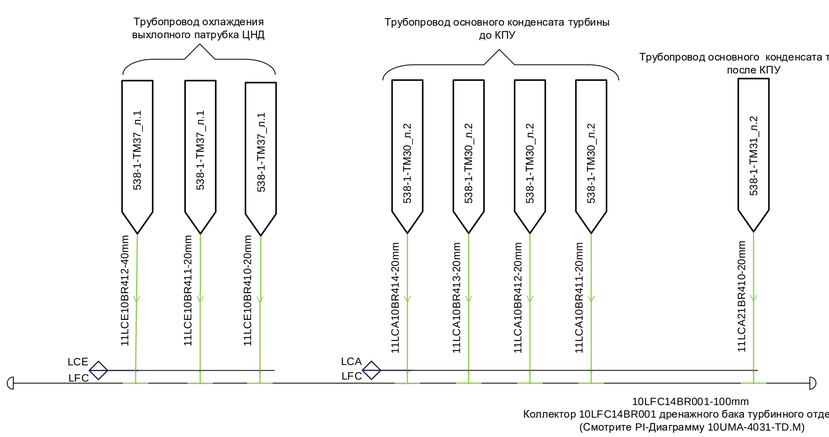

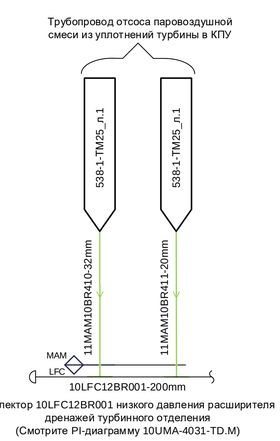

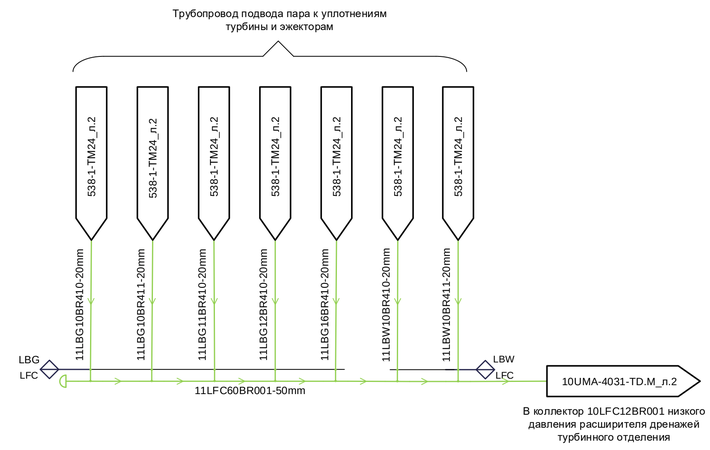

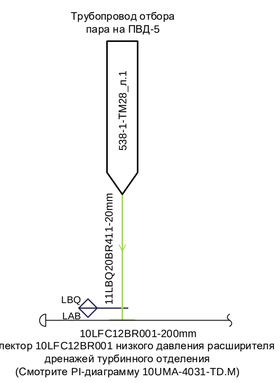

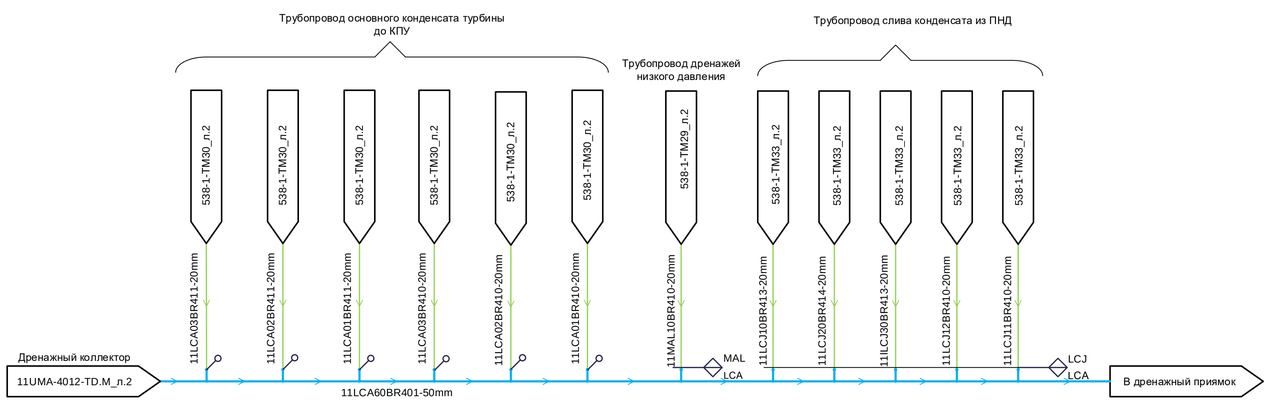

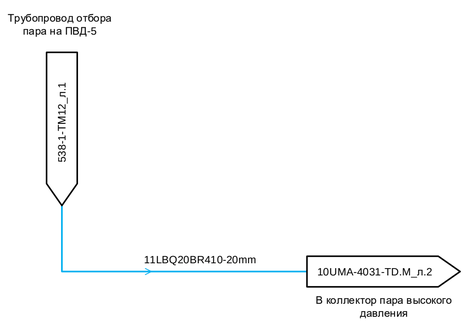

Примечание: PI-диаграмма выполнена в соответствии с рабочей документацией АО «Технология Лонас»

1	-	Зам				
Изм.	Кол.уч	Лист	№ док.	Подп.	Дата	
Разработал		Полянская				
Проверил		Калинкина				
Н. контр.		Гридчина				

141N4-10UMA-4938-TD.M

Амурская ТЭС. Обеспечение нужд Амурского ГПЗ. Строительство основного технологического комплекса объектов Амурской ТЭС (2 ПСУх80МВт). Этап 1. "Амурская ТЭС (ПСУ-2х80 МВт)"

Паротурбинное отделение. PI-диаграмма дренажей внутритурбинных трубопроводов и вспомогательного оборудования ПТУ №1

Стадия	Лист	Листов
Р	2	

PI-диаграмма дренажей внутритурбинных трубопроводов и вспомогательного оборудования ПТУ №1.Системы LB,LC,LF,MA

АКЦИОНЕРНОЕ ОБЩЕСТВО ИНСТИТУТ ТЕПЛОЭЛЕКТРОПРОЕКТ г. МОСКВА

Согласовано

ОАСУ

Взам. инв. №

Подпись и дата

Инв. № подл.

Формат А1