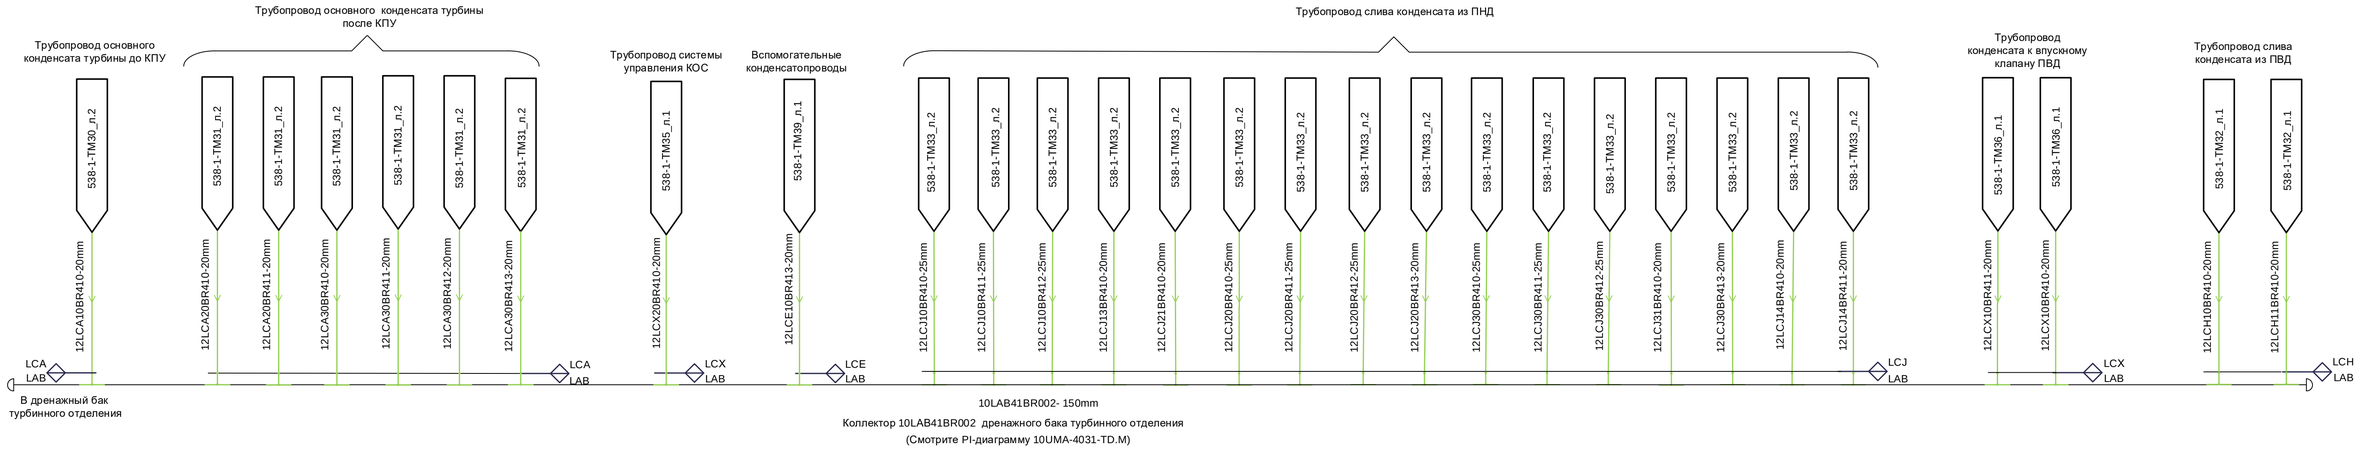

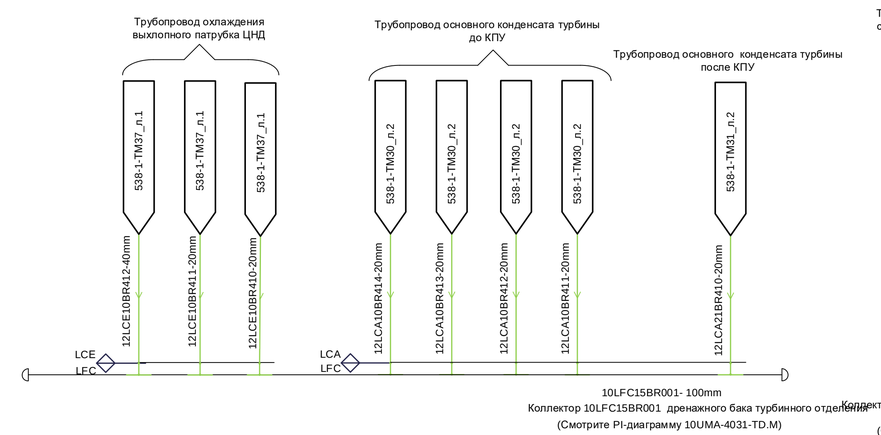

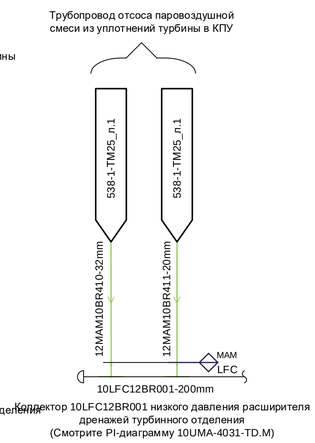

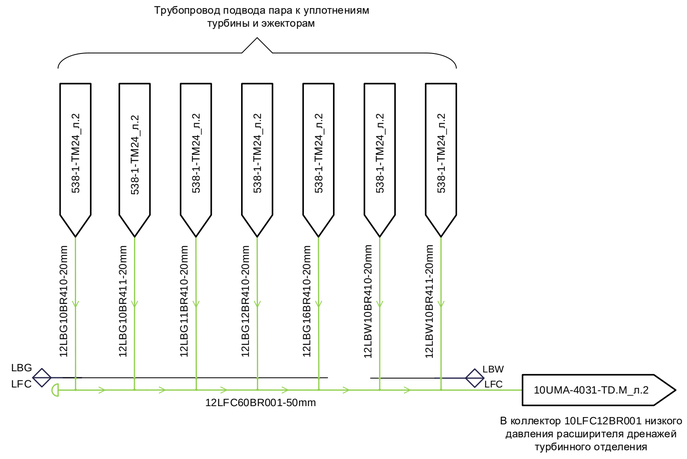

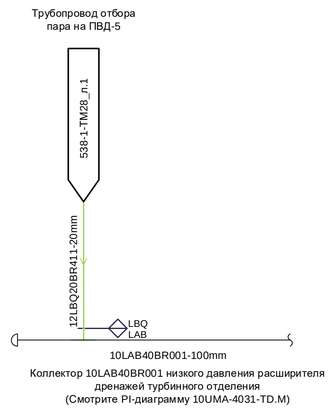

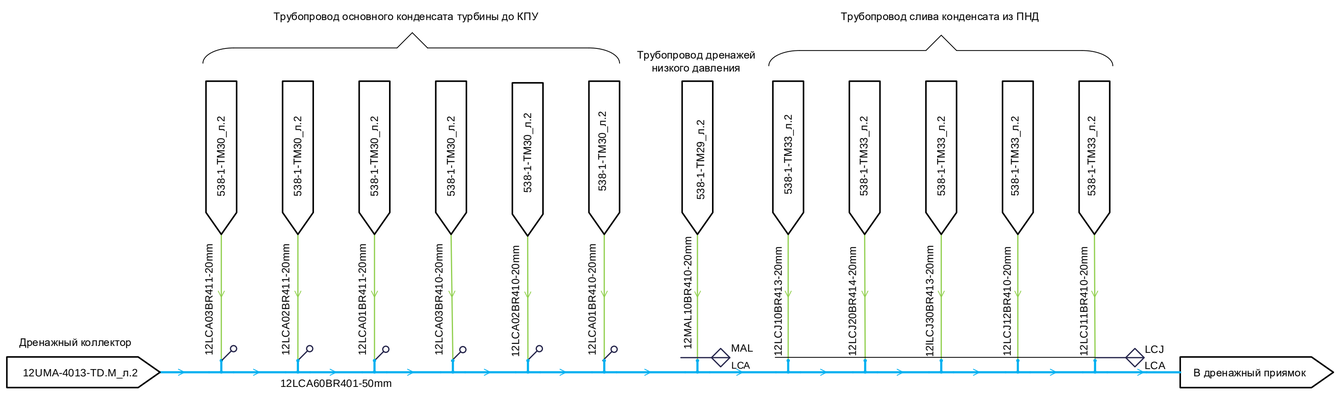

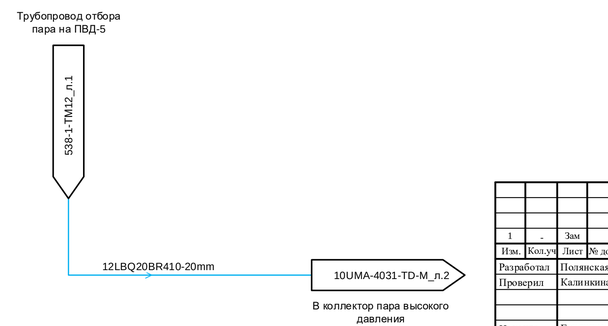

Примечание: PI-диаграмма выполнена в соответствии с рабочей документацией АО «Технология Лонас»

1	-	Зам				141N4-10UMA-4941-TD.M	
Изм.	Кол.уч	Лист	№ док.	Подп.	Дата	Амурская ТЭС. Обеспечение нужд Амурского ГПЗ. Строительство основного технологического комплекса объектов Амурской ТЭС (2 ПСУх80МВт). Этап 1. "Амурская ТЭС (ПСУ-2х80 МВт)"	
Разработал	Полянская					Паротурбинное отделение. PI-диаграмма дренажей внутритурбинных трубопроводов и вспомогательного оборудования ПТУ №2	Стадия: Р; Лист: 2; Листов:
Проверил	Калинкина						
Н. контр.	Грядчина					PI-диаграмма дренажей внутритурбинных трубопроводов и вспомогательного оборудования ПТУ №2.Системы LB,LC,LE,LF,MA	АКЦИОНЕРНОЕ ОБЩЕСТВО ИНСТИТУТ ТЕПЛОЭЛЕКТРОПРОЕКТ г. МОСКВА

Согласовано

ОАСУ

Взам. инв. №

Подпись и дата

Инв. № подл.

Формат А1