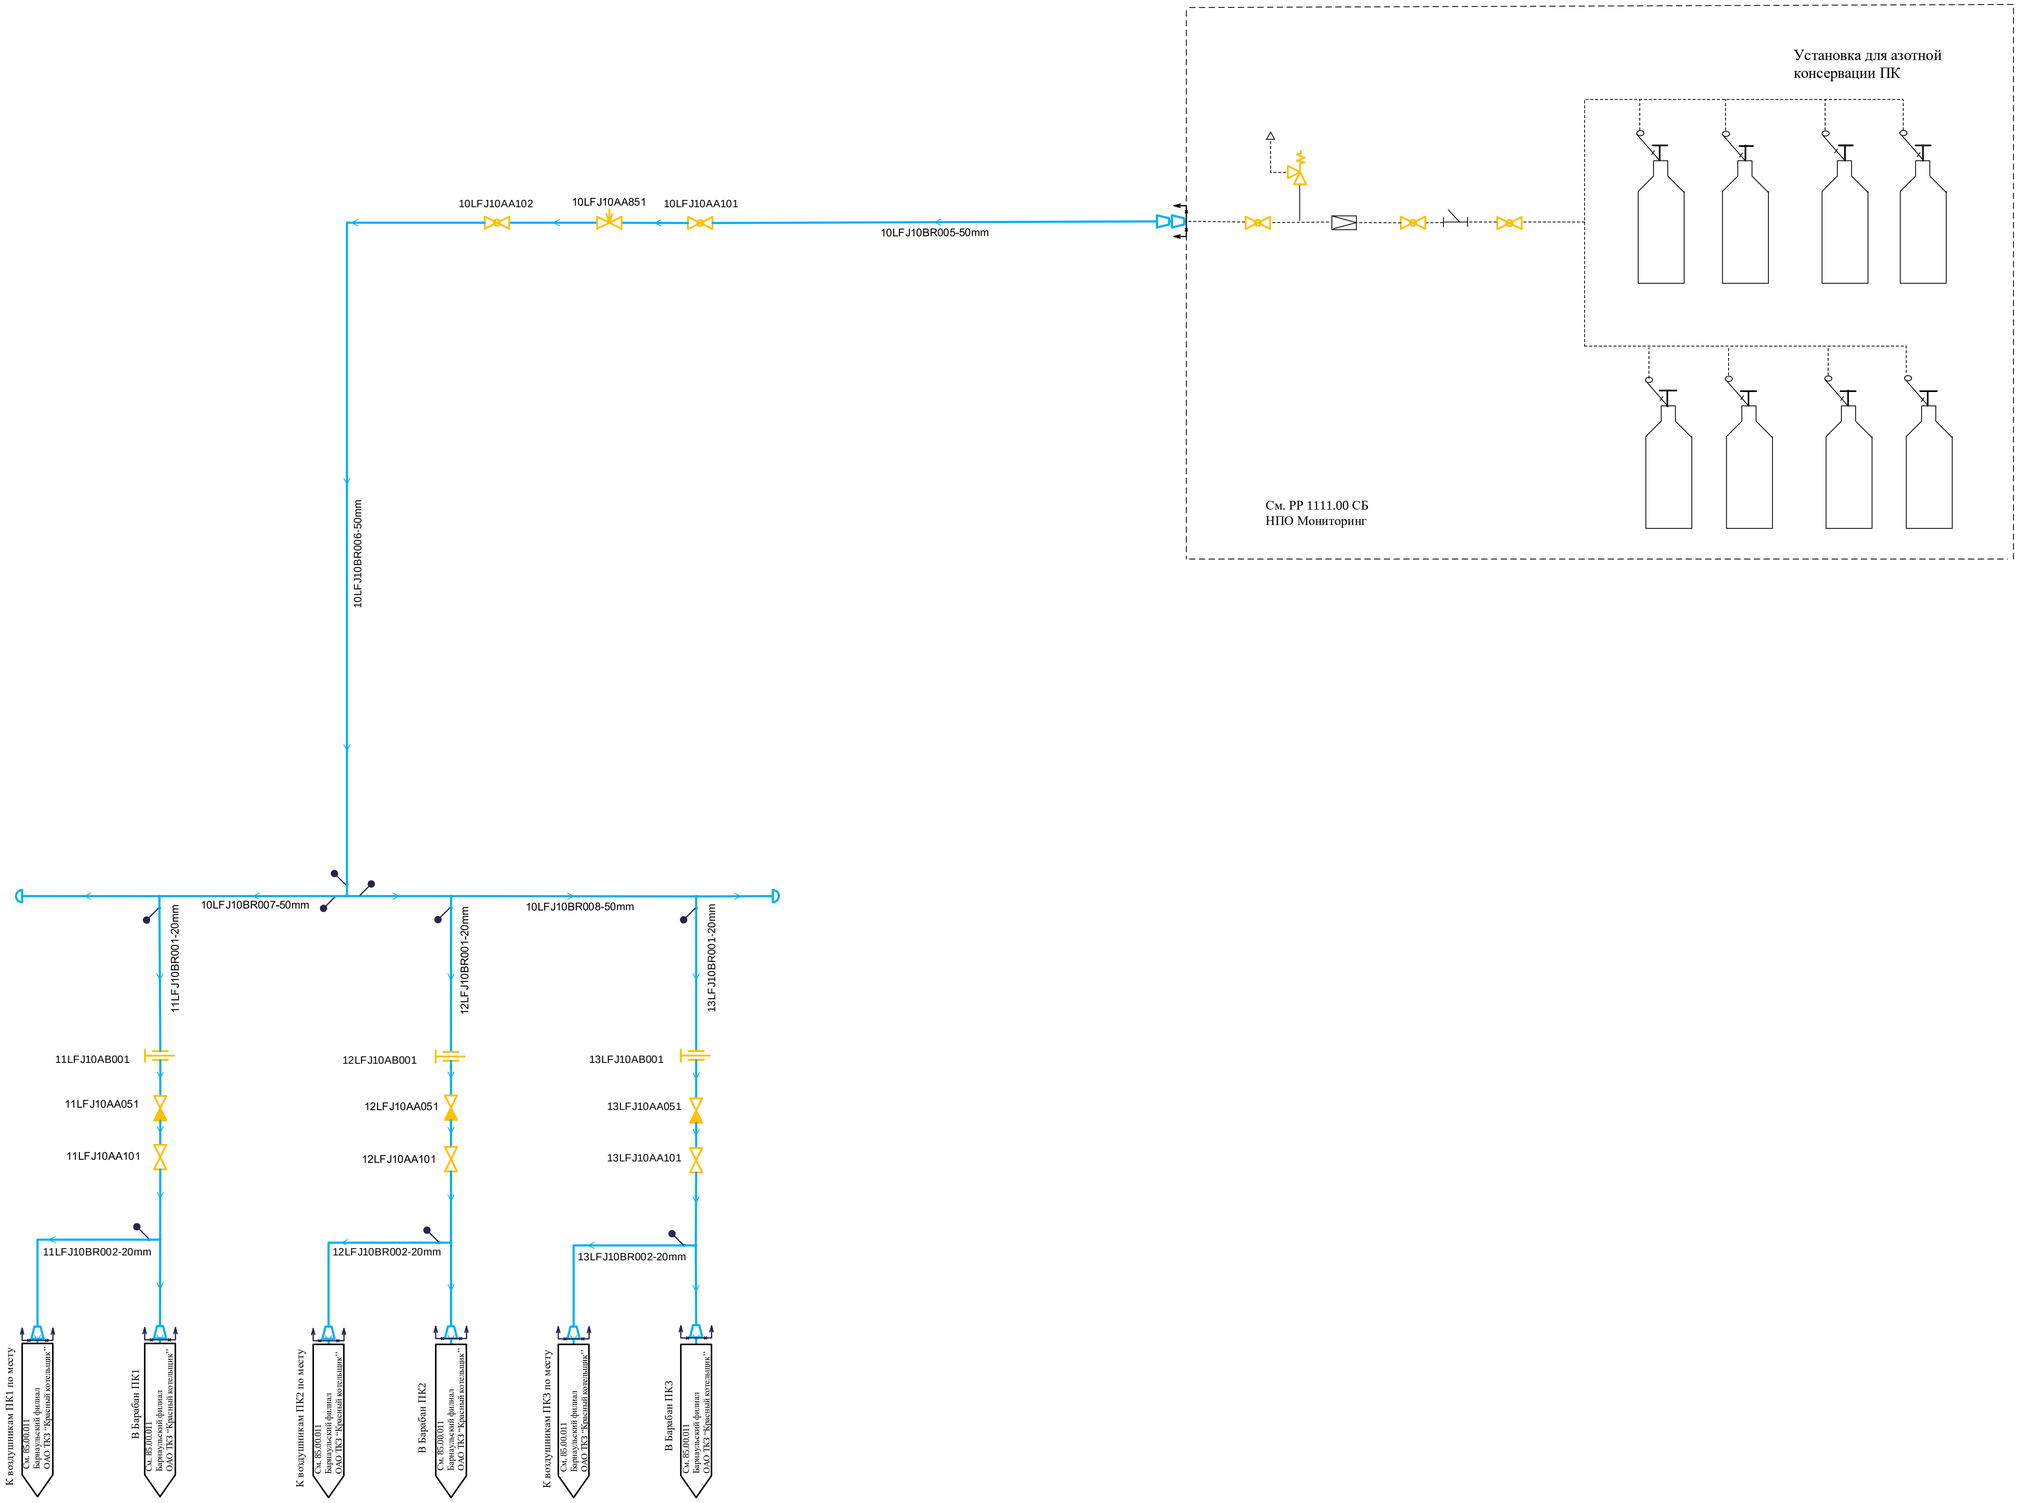

После заполнения азотом, поддерживать давление 0.035 МПа(изб)

Изм.	Кол.уч	Лист	№ док.	Подп.	Дата	141N4-10UHJ-5243-TD.M
Н.контр.		Астраханцев				Амурская ТЭС. Обеспечение нужд Амурского ГПЗ. Строительство основного технологического комплекса объектов Амурской ТЭС (2 ПСУх80МВт). Этап 1. « Амурская ТЭС (ПСУ-2х80 МВт»
						Главный корпус. PI-диаграмма системы консервации паровых котлов
						Стадия: Р; Лист: 2; Листов:
Зам.нач.		Майорова				PI-Диаграмма трубопроводов азота. Система LFJ.
Инж.2кат.		Бычкова				АКЦИОНЕРНОЕ ОБЩЕСТВО ИНСТИТУТ ТЕПЛОЭЛЕКТРОПРОЕКТ Г. МОСКВА

Согласовано
Гл.контр. Астраханцев
Зам.нач. Майорова
Инж.2кат. Бычкова

Взам. инв. №
Подпись и дата
Инв. № подл.

Формат А1