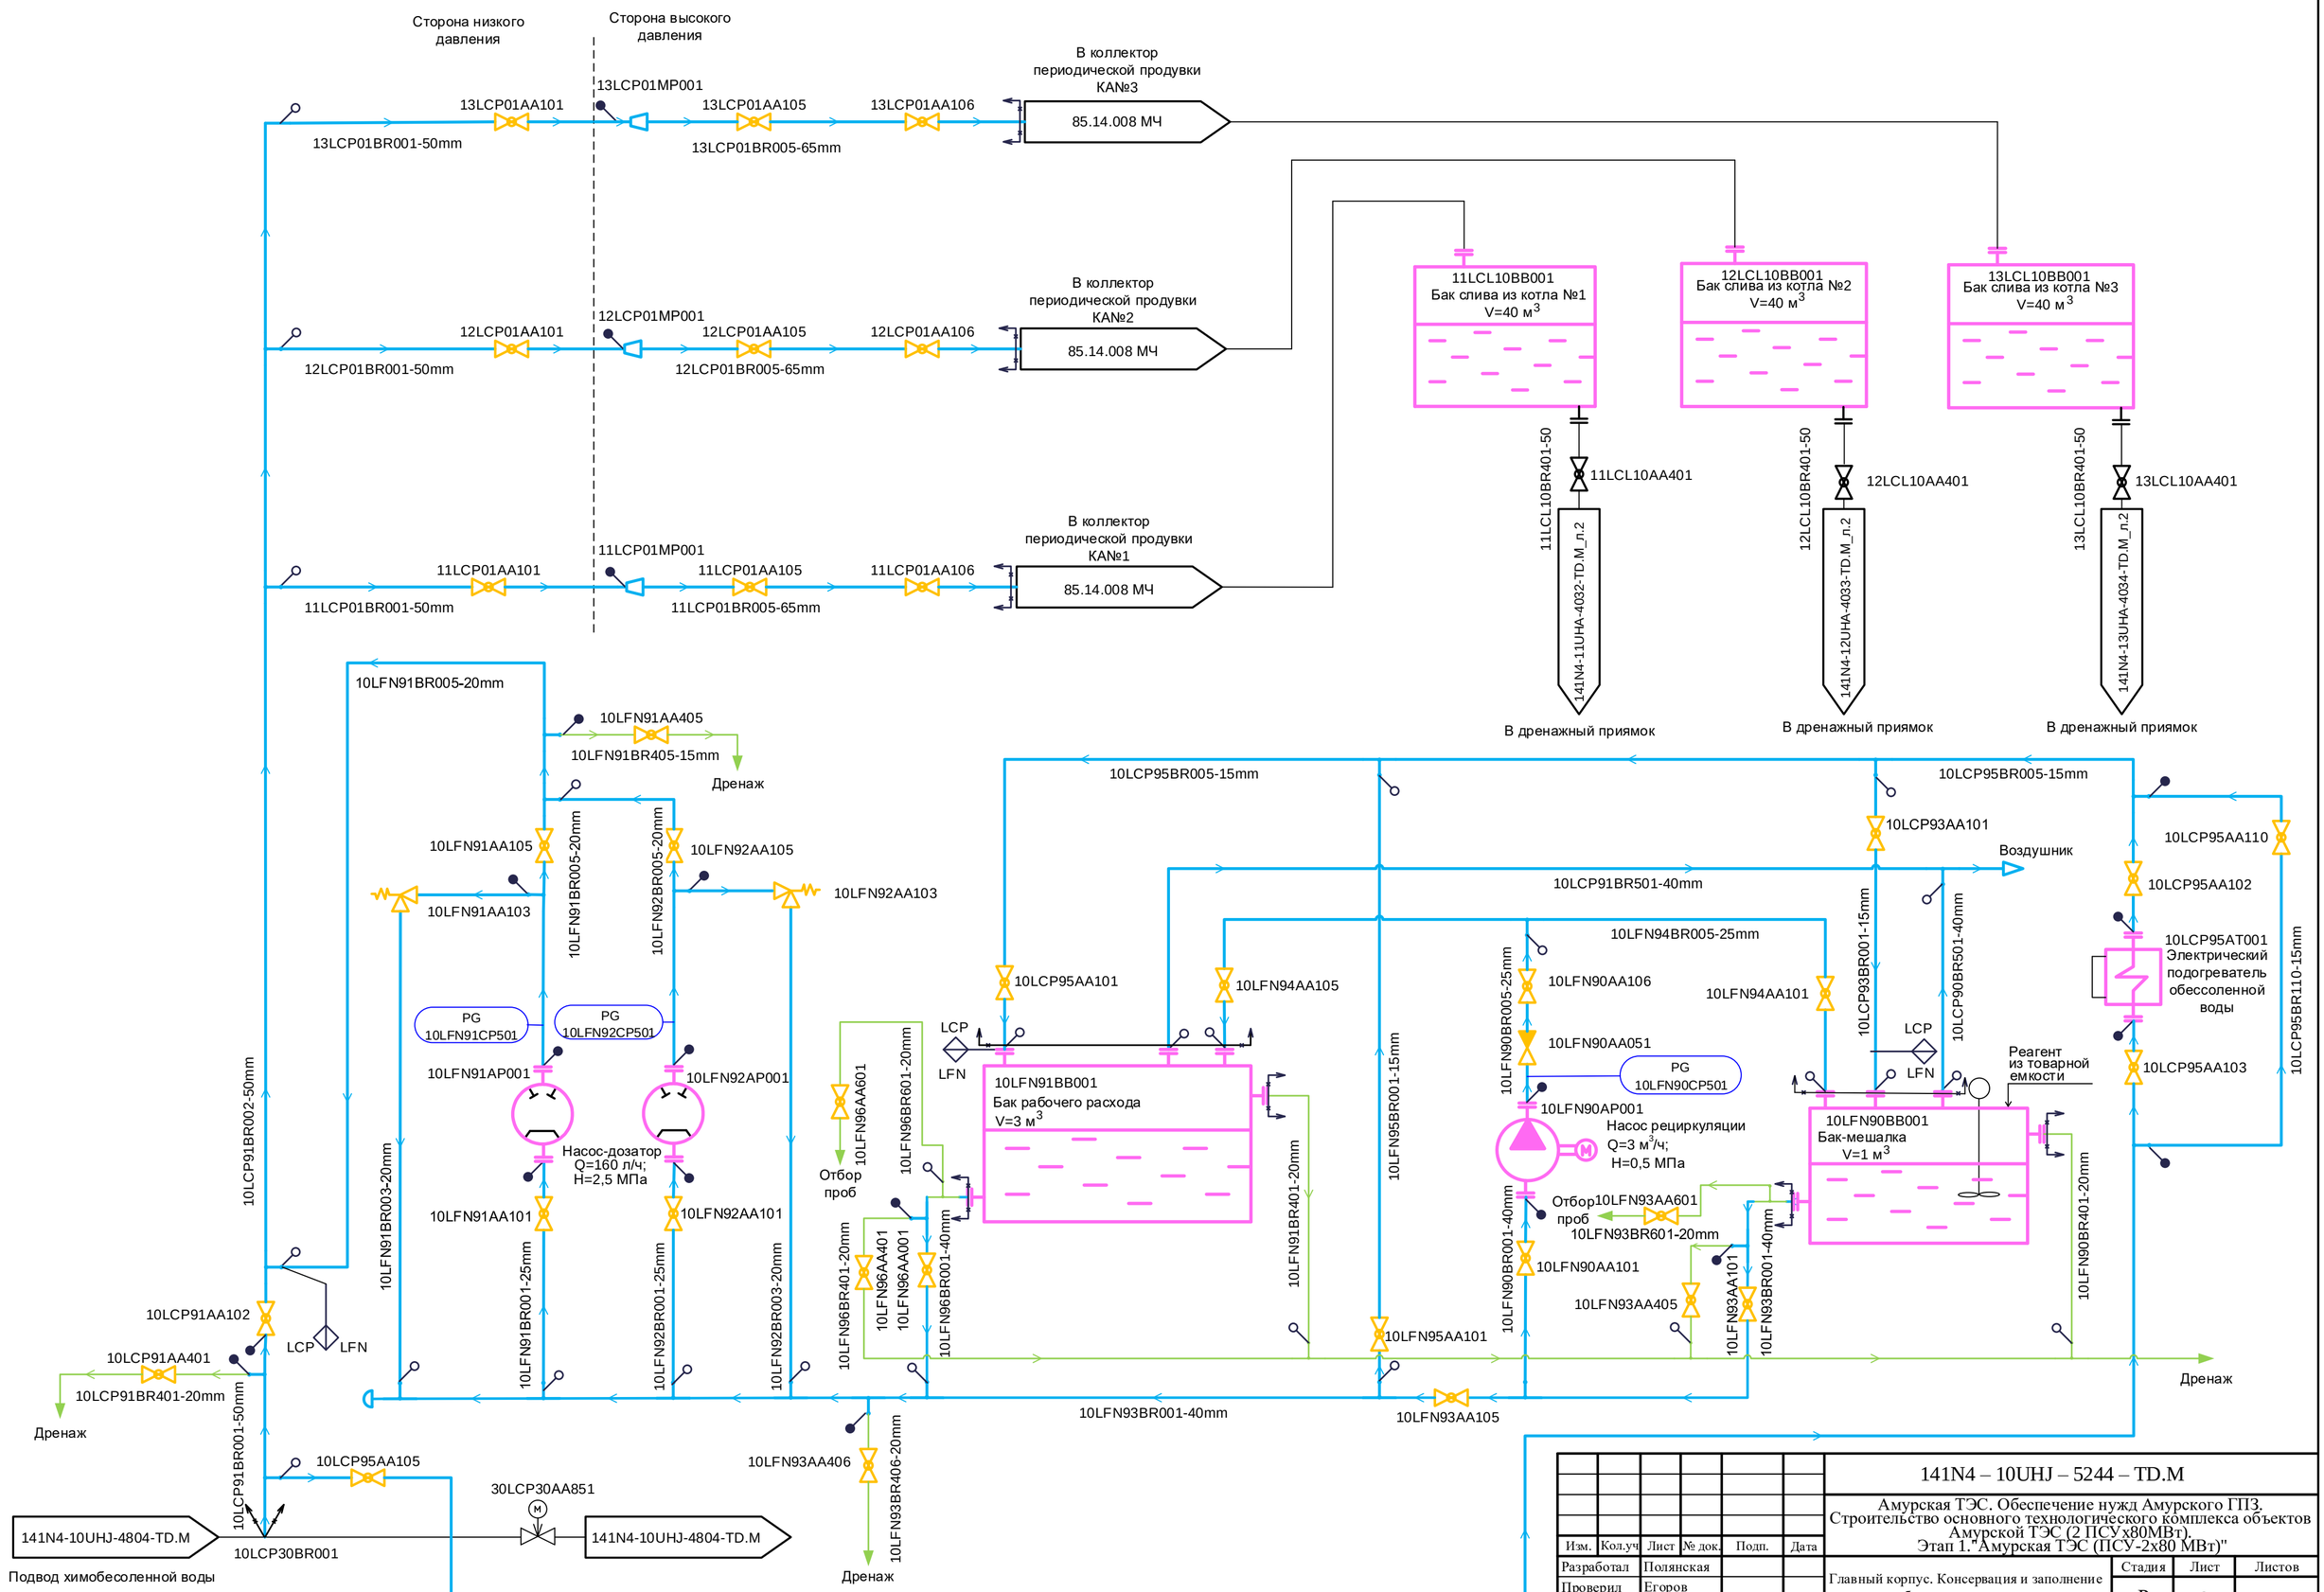

Изм.	Кол.уч	Лист	№ док.	Подп.	Дата	141N4 – 10UHJ – 5244 – TD.M
						Амурская ТЭС. Обеспечение нужд Амурского ГПЗ. Строительство основного технологического комплекса объектов Амурской ТЭС (2 ПСУ х80МВт). Этап 1."Амурская ТЭС (ПСУ-2х80 МВт)"
Разработал		Полянская				Главный корпус. Консервация и заполнение котлов ингибиторами коррозии
Проверил		Егоров				Стадия: Р; Лист: 2; Листов:
Н. контр.		Гридчина				PI-диаграмма консервации и заполнения котлов ингибиторами коррозии

АКЦИОНЕРНОЕ ОБЩЕСТВО ИНСТИТУТ ТЕПЛОЭЛЕКТРОПРОЕКТ Г. МОСКВА

Согласовано: ОАСУ Соболева

Взам. инв. № | Подпись и дата | Инв. № подл.

Формат А2