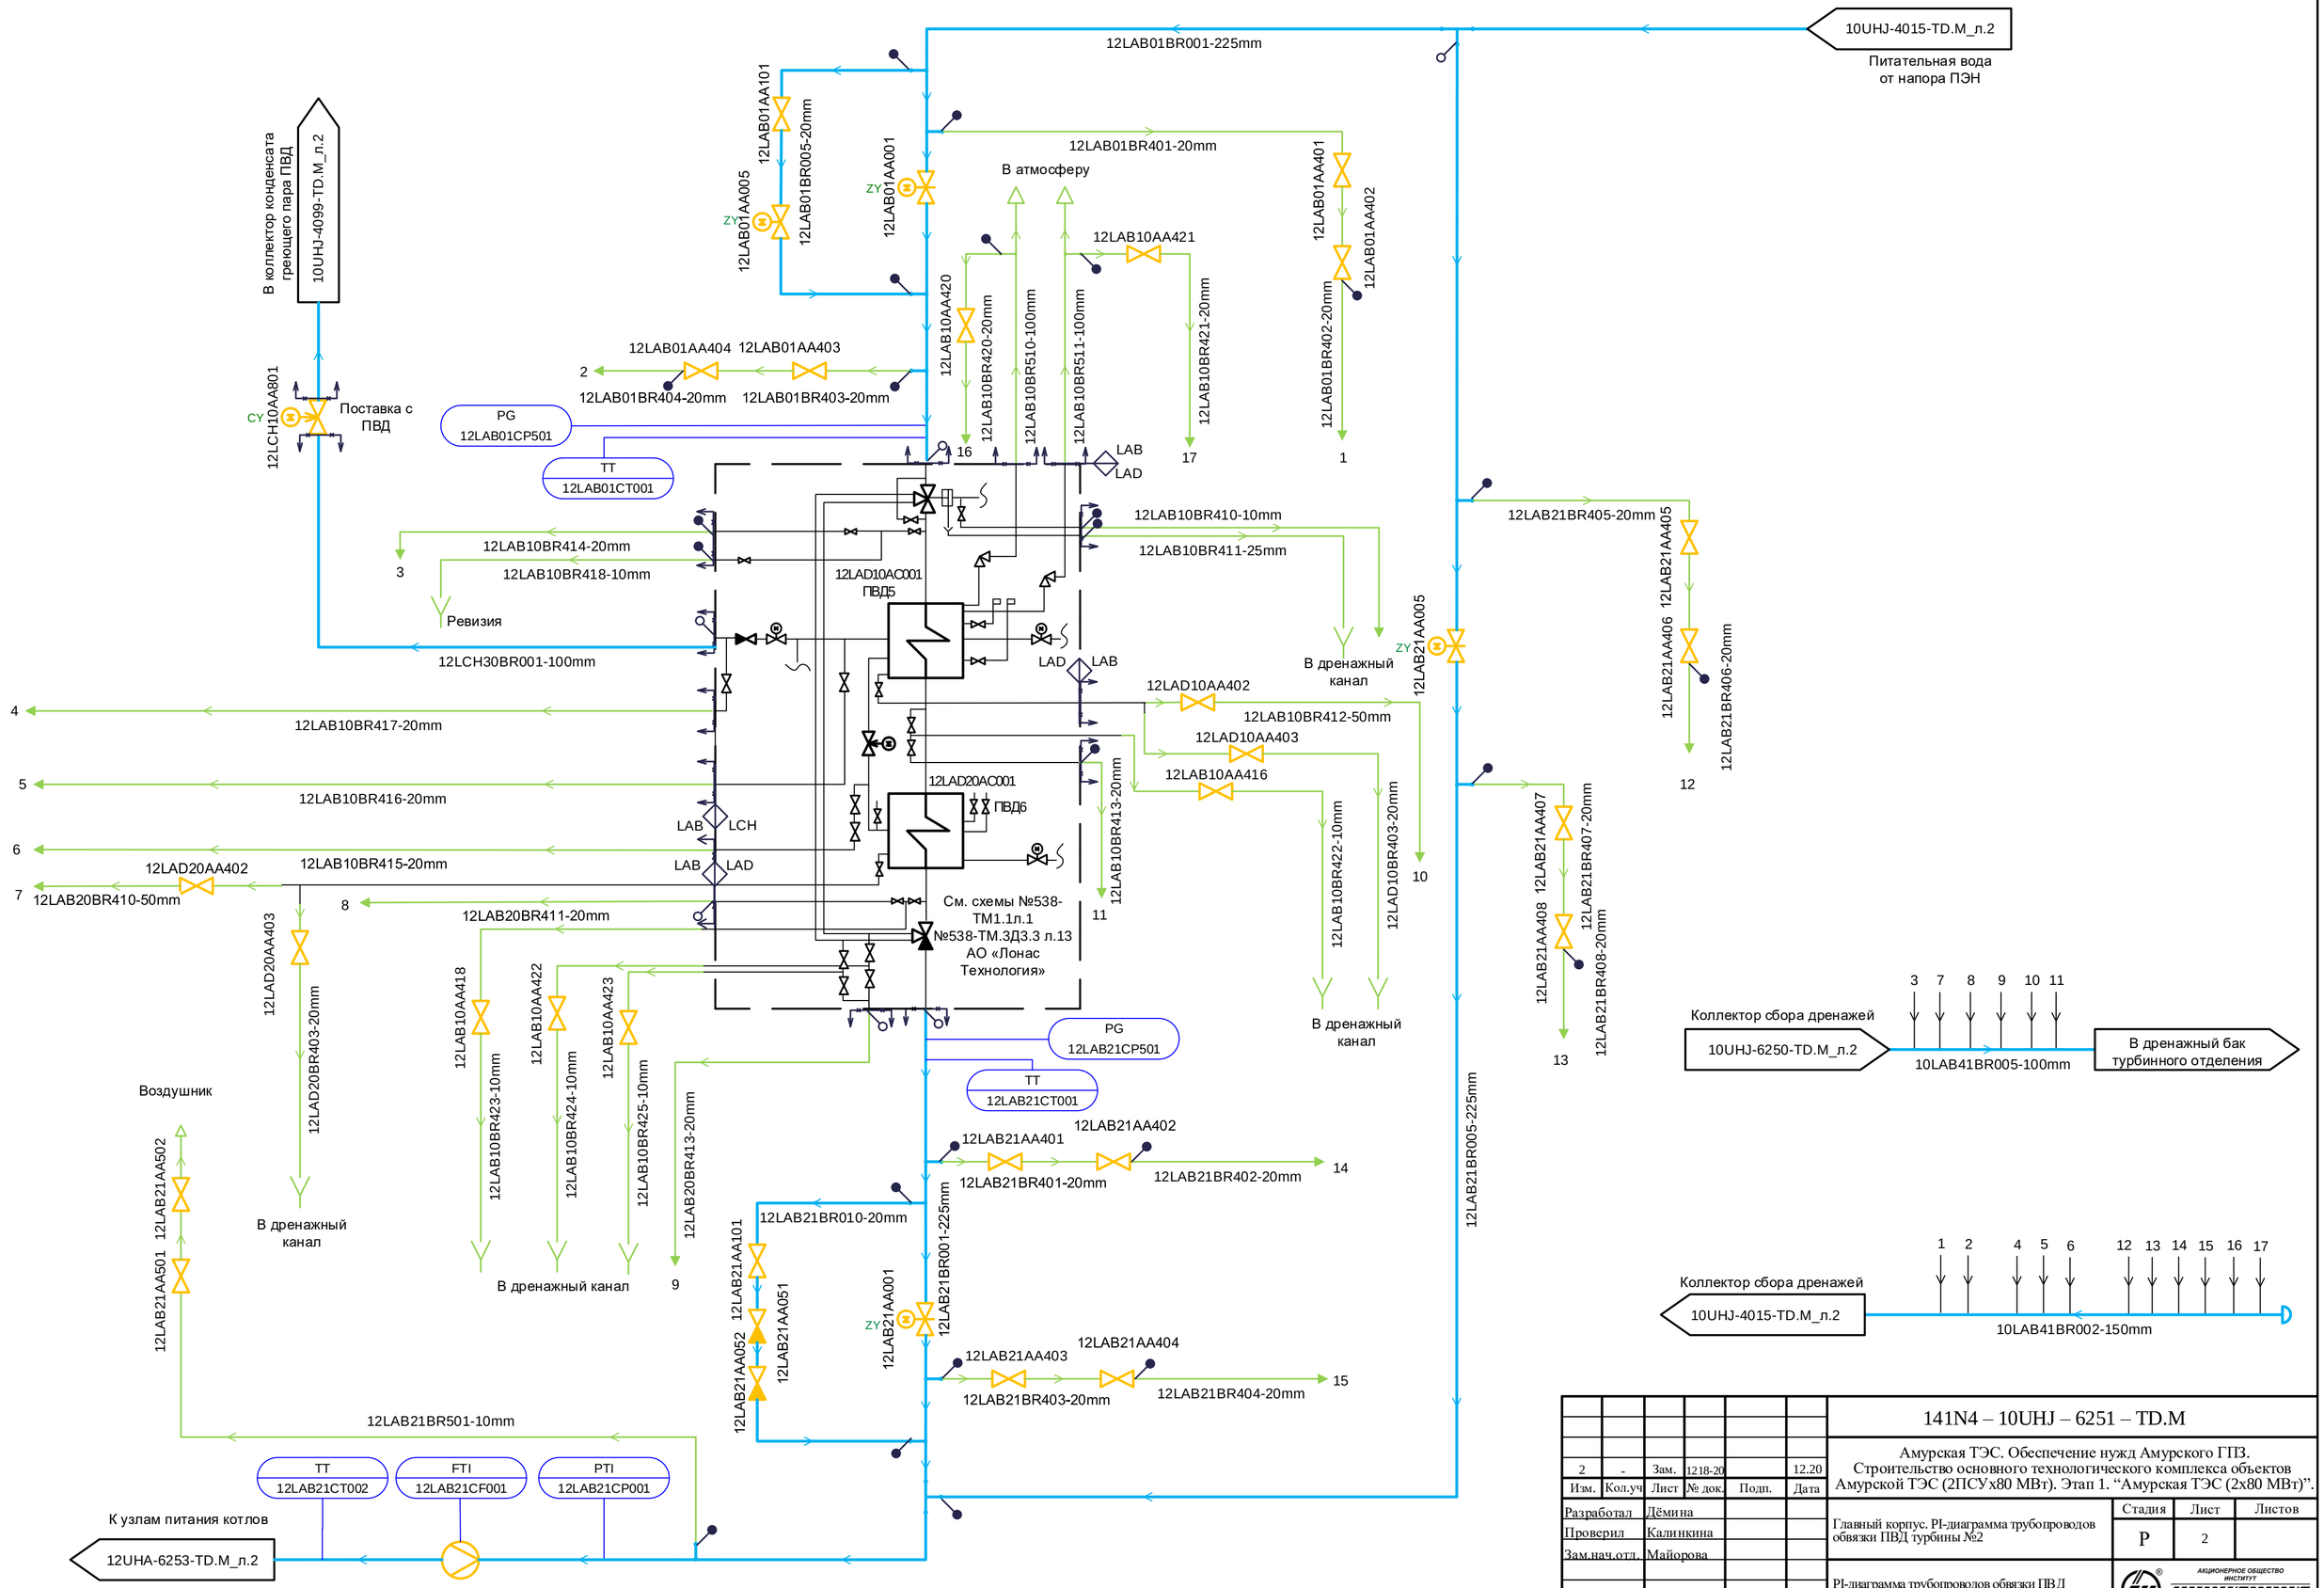

2	-	Зам.	1218-20		12.20	
Изм.	Кол.уч	Лист	№ док.	Подп.	Дата	
Разработал		Дёмина				
Проверил		Калинкина				
Зам.нач.отд.		Майорова				
Н. контр.		Астраханцев				

141N4 – 10UHJ – 6251 – TD.M

Амурская ТЭС. Обеспечение нужд Амурского ГПЗ.
Строительство основного технологического комплекса объектов Амурской ТЭС (2ПСУх80 МВт). Этап 1. "Амурская ТЭС (2х80 МВт)".

Главный корпус. PI-диаграмма трубопроводов обвязки ПВД турбины №2

Стадия	Лист	Листов
Р	2	

PI-диаграмма трубопроводов обвязки ПВД турбины №2. Система LAB

АКЦИОНЕРНОЕ ОБЩЕСТВО ИНСТИТУТ ТЕПЛОЭЛЕКТРОПРОЕКТ г. МОСКВА

Согласовано
ОАСУ Соболева
Взам. инв. №
Подпись и дата
Инв. № подл.

Формат А2