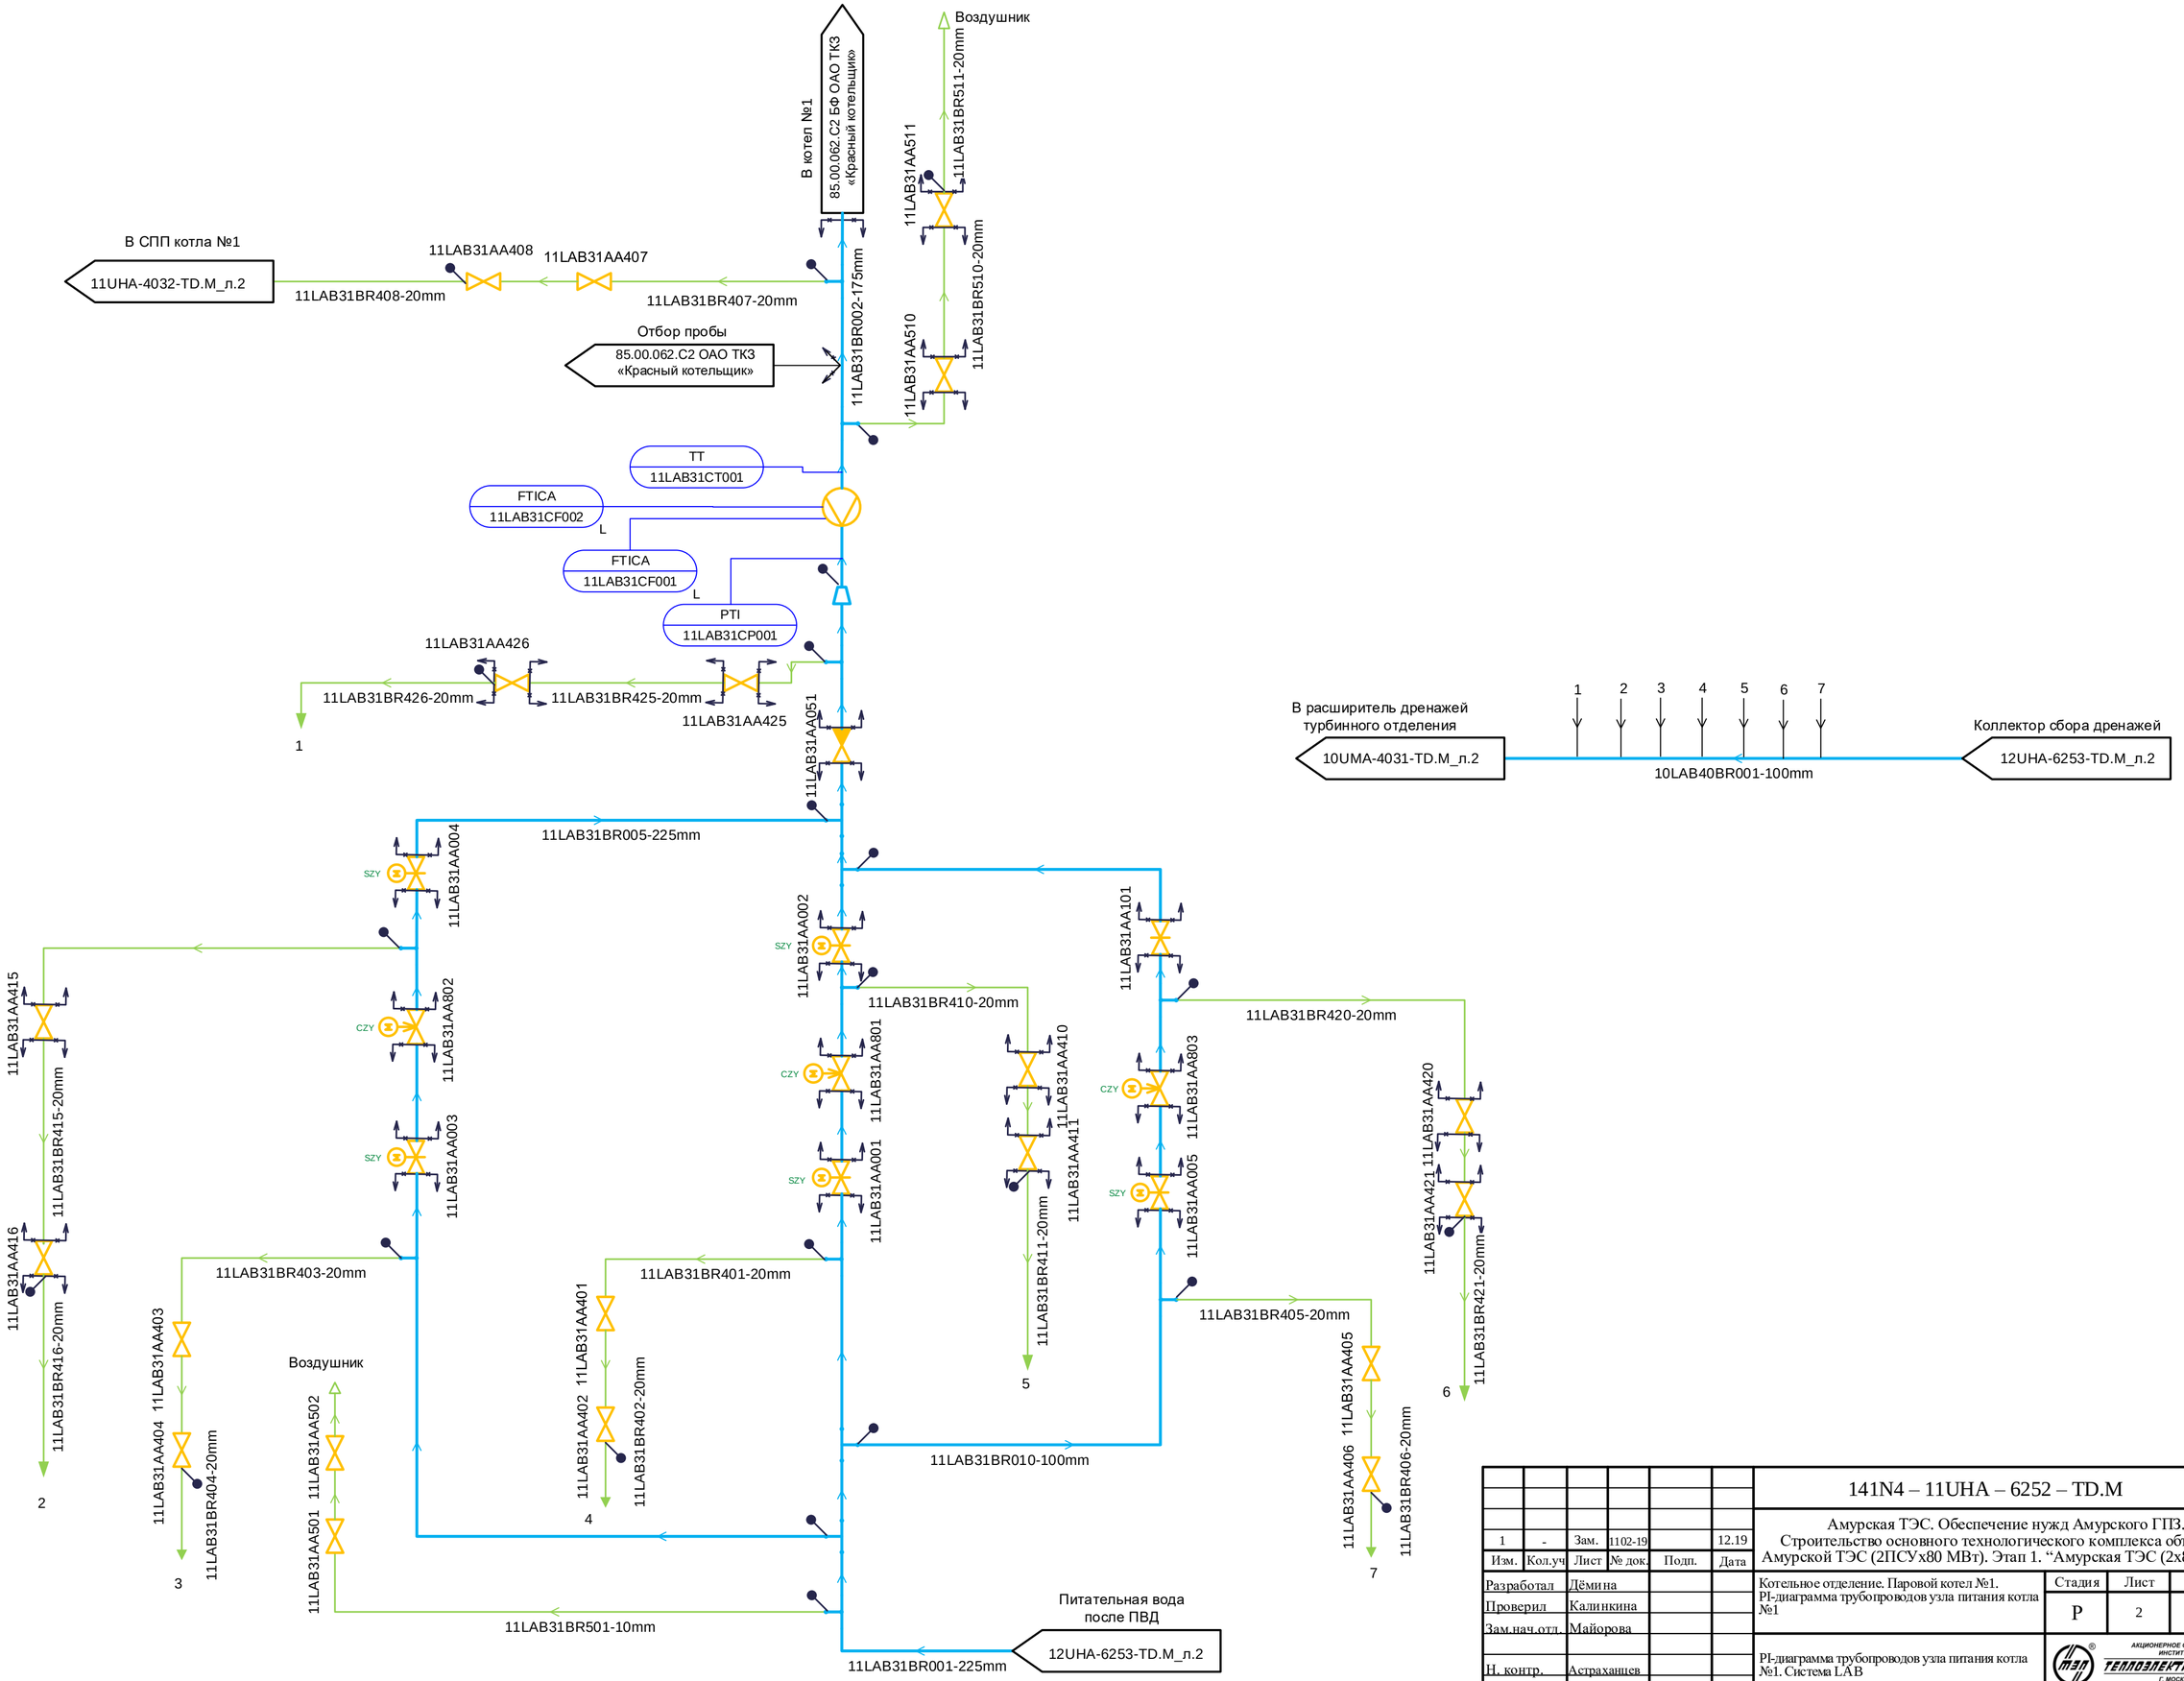

1	-	Зам.	1102-19		12.19	
Изм.	Кол.уч	Лист	№ док.	Подп.	Дата	

141N4 – 11UHA – 6252 – TD.M

Амурская ТЭС. Обеспечение нужд Амурского ГПЗ. Строительство основного технологического комплекса объектов Амурской ТЭС (2ПСУх80 МВт). Этап 1. "Амурская ТЭС (2х80 МВт)".

Разработал	Дёмина	
Проверил	Калинкина	
Зам.нач.отд.	Майорова	
Н. контр.	Астраханцев	

Котельное отделение. Паровой котел №1. PI-диаграмма трубопроводов узла питания котла №1

Стадия	Лист	Листов
Р	2	

PI-диаграмма трубопроводов узла питания котла №1. Система LAB

АКЦИОНЕРНОЕ ОБЩЕСТВО ИНСТИТУТ ТЕПЛОЭЛЕКТРОПРОЕКТ Г. МОСКВА

Согласовано

ОАСУ Соболева

Взам. инв. №

Подпись и дата

Инв. № подл.

Формат А2