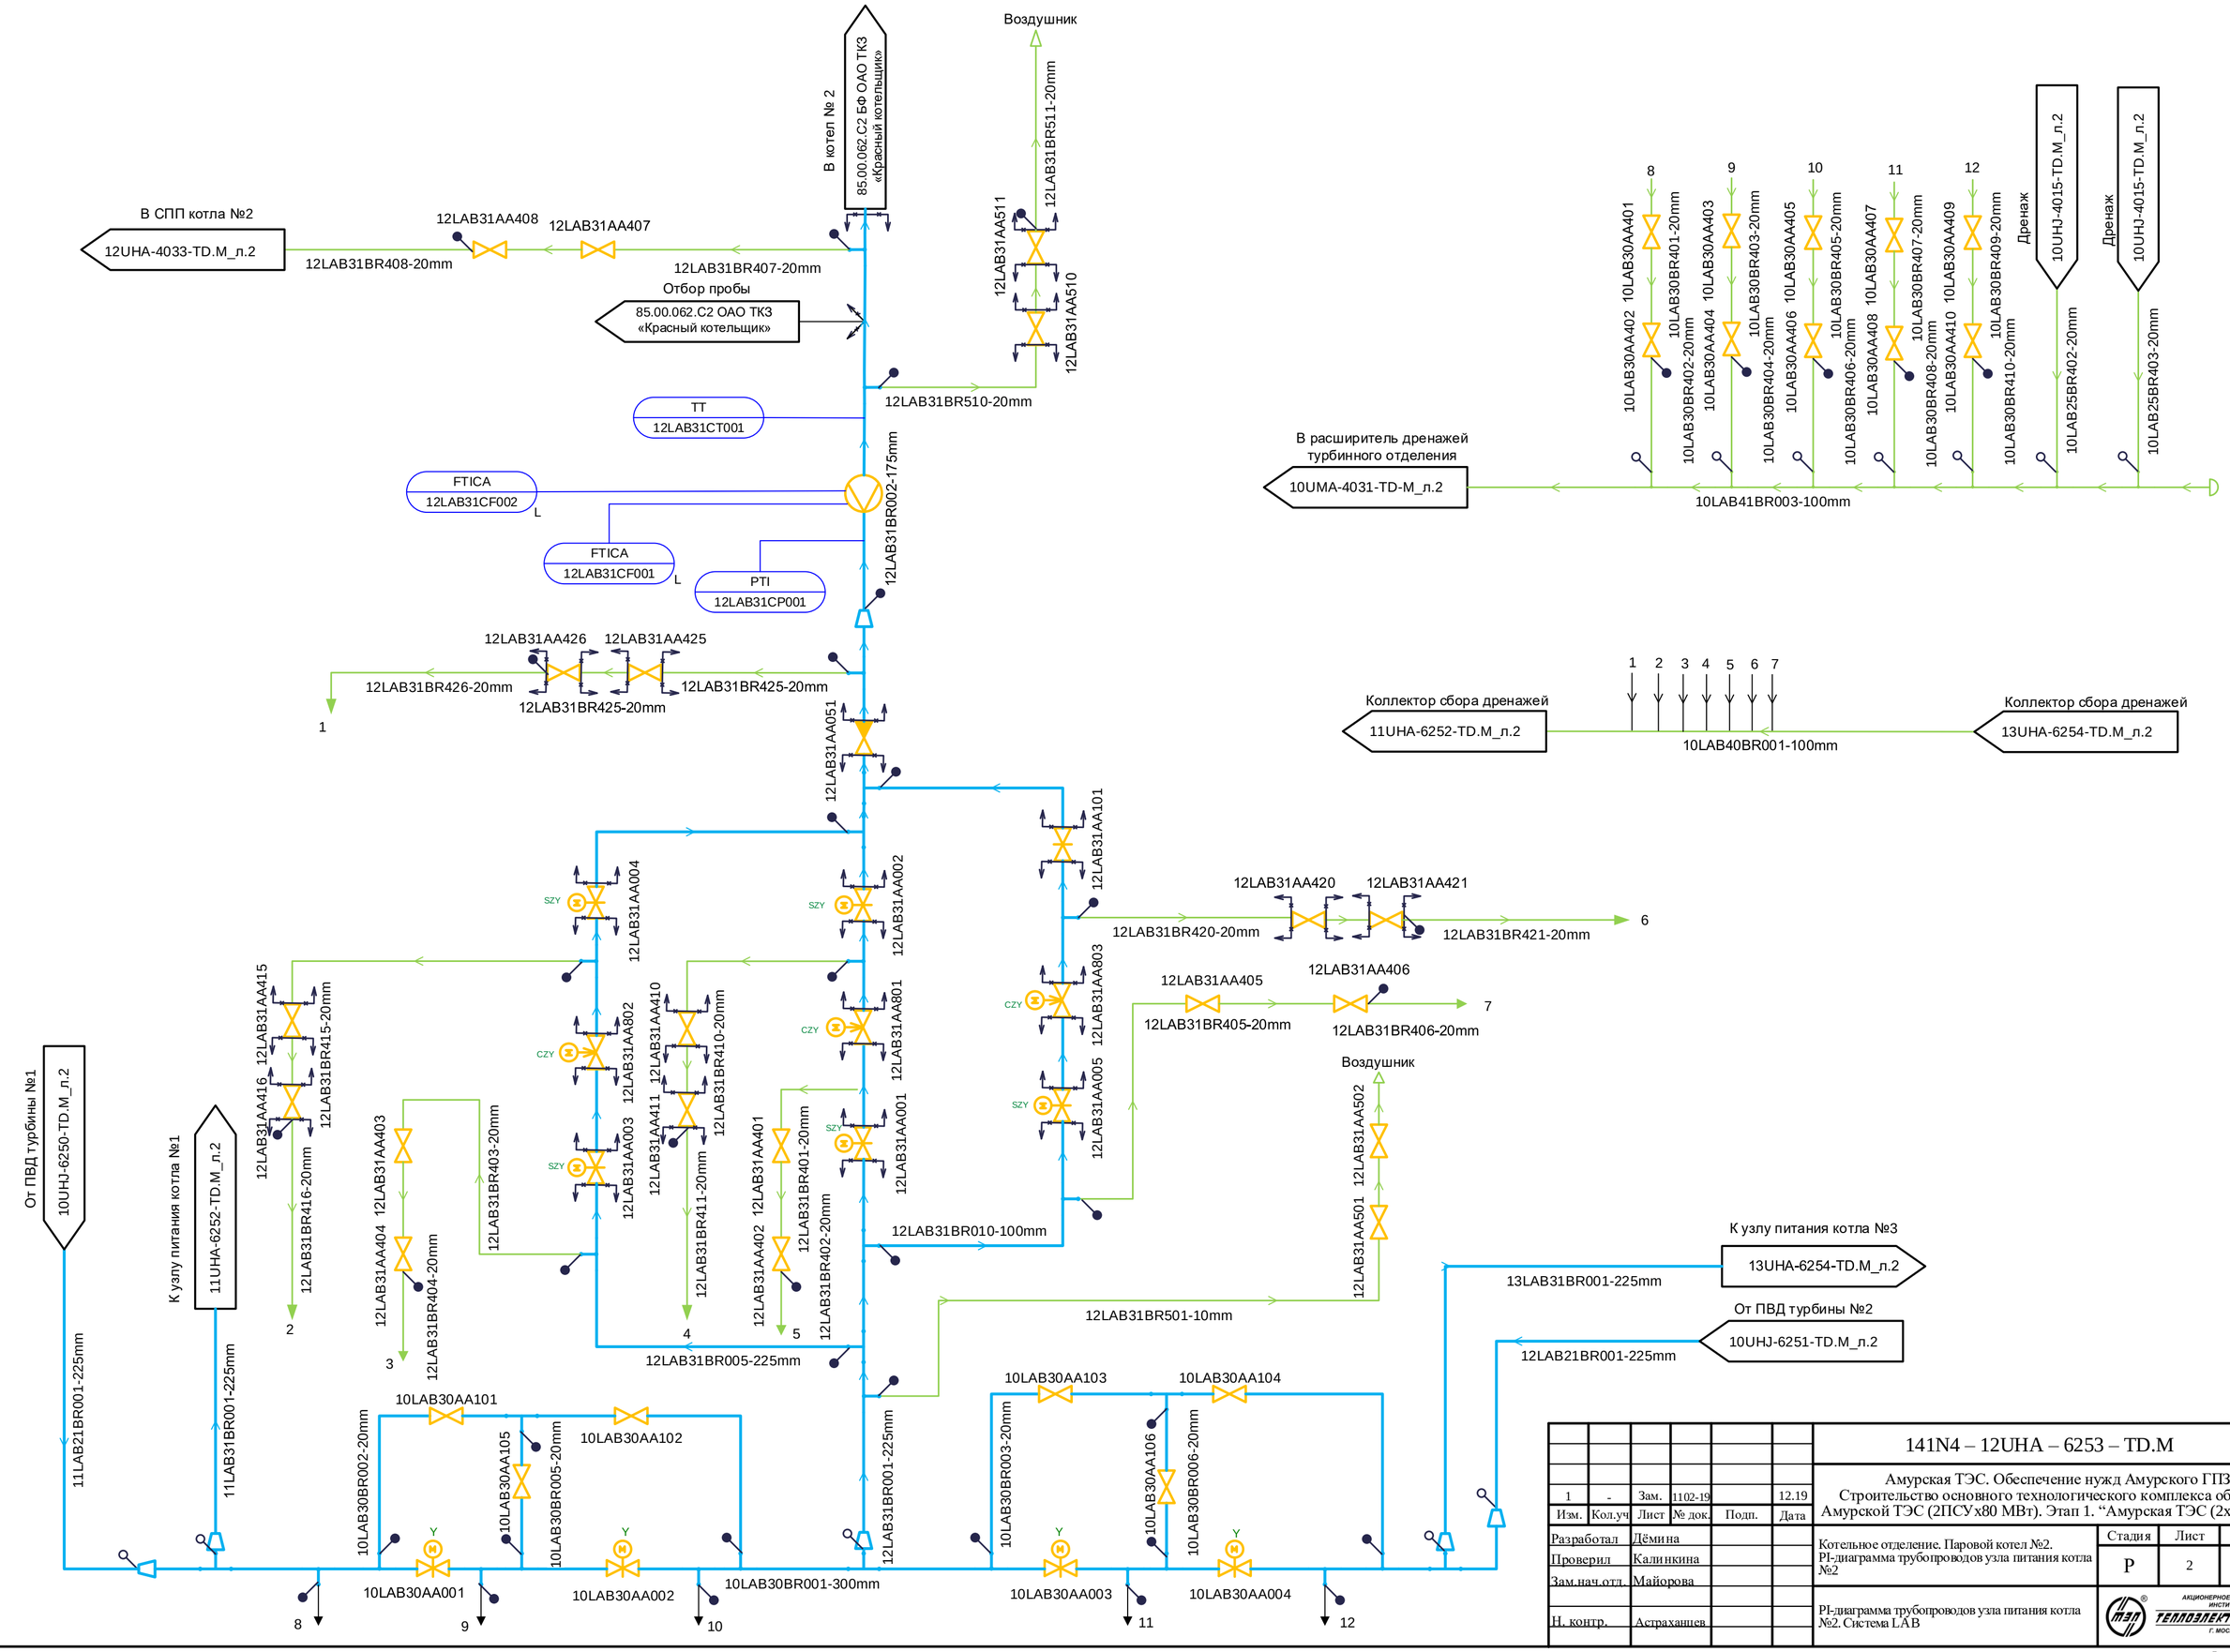

1	-	Зам.	1102-19		12.19	141N4 – 12UHA – 6253 – TD.M
Изм.	Кол.уч	Лист	№ док.	Подп.	Дата	Амурская ТЭС. Обеспечение нужд Амурского ГПЗ. Строительство основного технологического комплекса объектов Амурской ТЭС (2ПСУх80 МВт). Этап 1. "Амурская ТЭС (2х80 МВт)".
Разработал		Дёмина				Котельное отделение. Паровой котел №2. PI-диаграмма трубопроводов узла питания котла №2
Проверил		Калинкина				Стадия: Р; Лист: 2; Листов:
Зам.нач.отд.		Майорова				
Н. контр.		Астраханцев				PI-диаграмма трубопроводов узла питания котла №2. Система LAB

АКЦИОНЕРНОЕ ОБЩЕСТВО ИНСТИТУТ ТЕПЛОЭЛЕКТРОПРОЕКТ Г. МОСКВА

Согласовано

ОАСУ Соболева

Взам. инв. №

Подпись и дата

Инв. № подл.

Формат А2