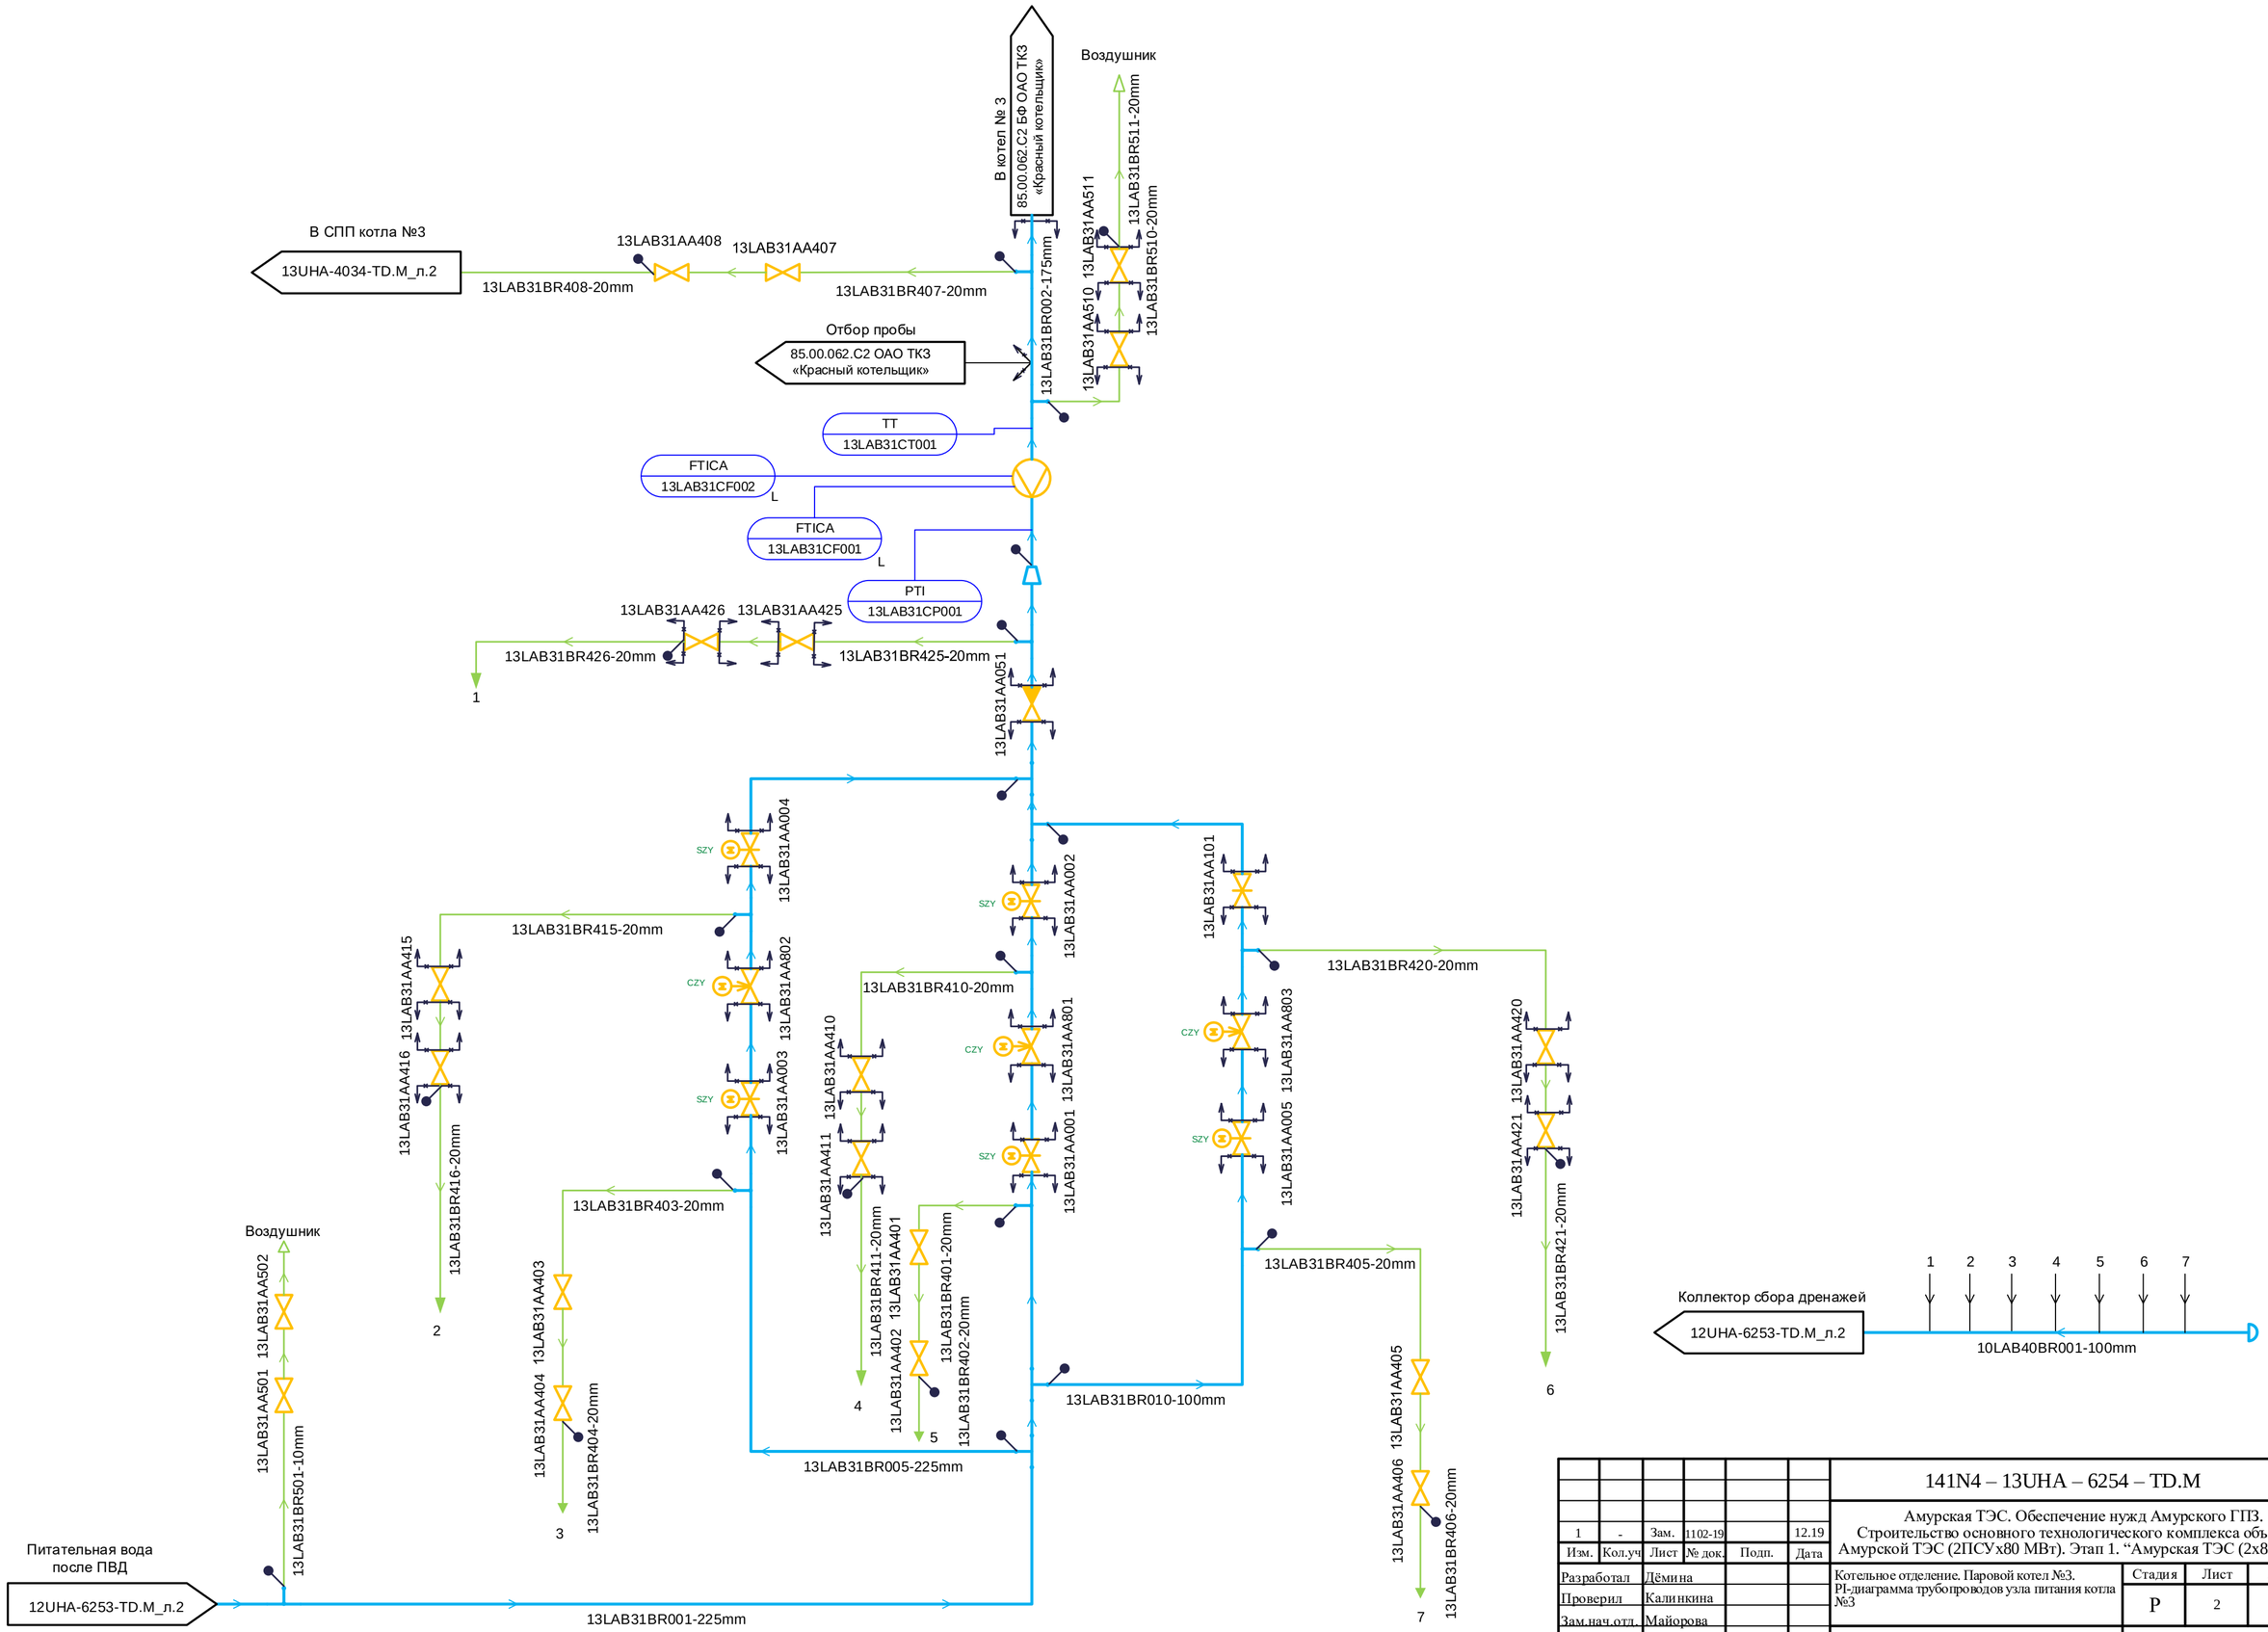

1	-	Зам.	1102-19		12.19	141N4 – 13UHA – 6254 – TD.M
Изм.	Кол.уч	Лист	№ док.	Подп.	Дата	Амурская ТЭС. Обеспечение нужд Амурского ГПЗ. Строительство основного технологического комплекса объектов Амурской ТЭС (2ПСУх80 МВт). Этап 1. “Амурская ТЭС (2х80 МВт)”.
Разработал	Дёмина					Котельное отделение. Паровой котел №3. PI-диаграмма трубопроводов узла питания котла №3
Проверил	Калинкина					Стадия: Р; Лист: 2; Листов:
Зам.нач.отд.	Майорова					
Н. контр.	Астраханцев					PI-диаграмма трубопроводов узла питания котла №3. Система LAB

АКЦИОНЕРНОЕ ОБЩЕСТВО ИНСТИТУТ ТЕПЛОЭЛЕКТРОПРОЕКТ Г. МОСКВА

Согласовано: ОАСУ Соболева

Взам. инв. № | Подпись и дата | Инв. № подл.

Формат А2