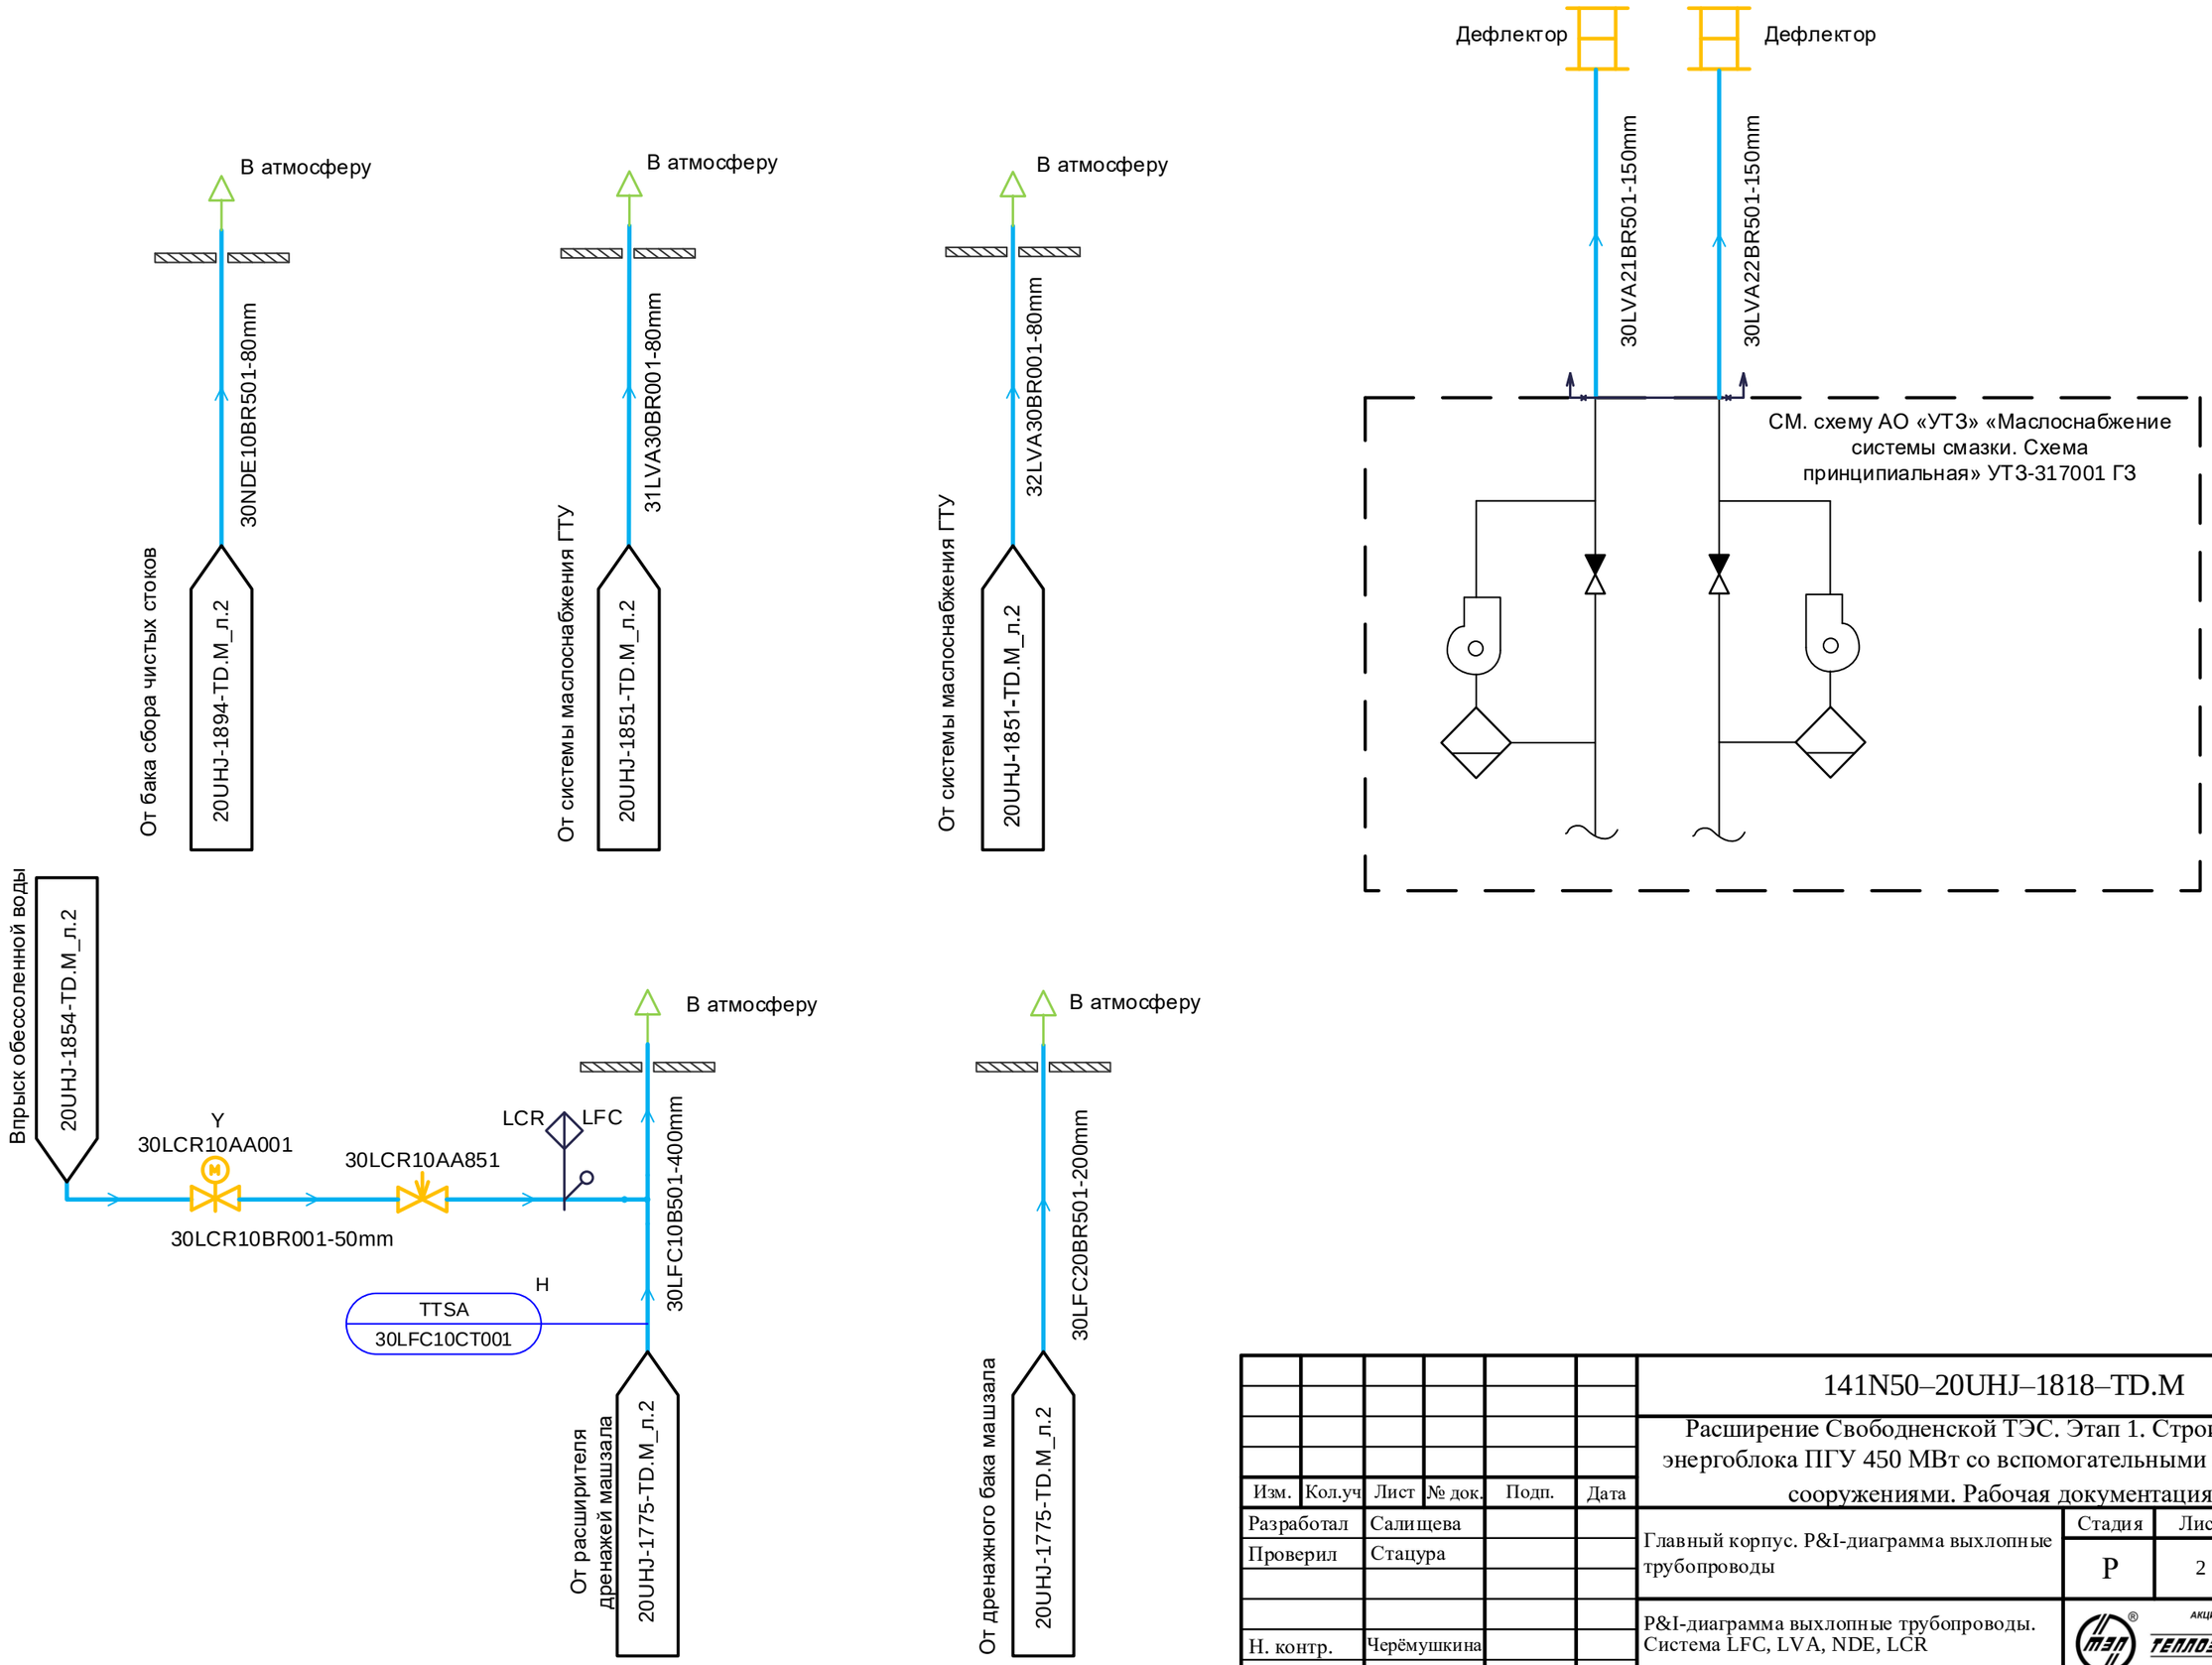

Изм.	Кол.уч	Лист	№ док.	Подп.	Дата
Разработал		Салищева			
Проверил		Стацура			
Н. контр.		Черёмушкина			

141N50–20UHJ–1818–TD.M

Расширение Свободненской ТЭС. Этап 1. Строительство энергоблока ПГУ 450 МВт со вспомогательными зданиями и сооружениями. Рабочая документация.

Главный корпус. P&I-диаграмма выхлопные трубопроводы

Стадия	Лист	Листов
Р	2	

P&I-диаграмма выхлопные трубопроводы. Система LFC, LVA, NDE, LCR

АКЦИОНЕРНОЕ ОБЩЕСТВО ИНСТИТУТ ТЕПЛОЭЛЕКТРОПРОЕКТ Г. МОСКВА

Согласовано

ОАСУ

Взам. инв. №

Подпись и дата

Инв. № подл.

Формат А3