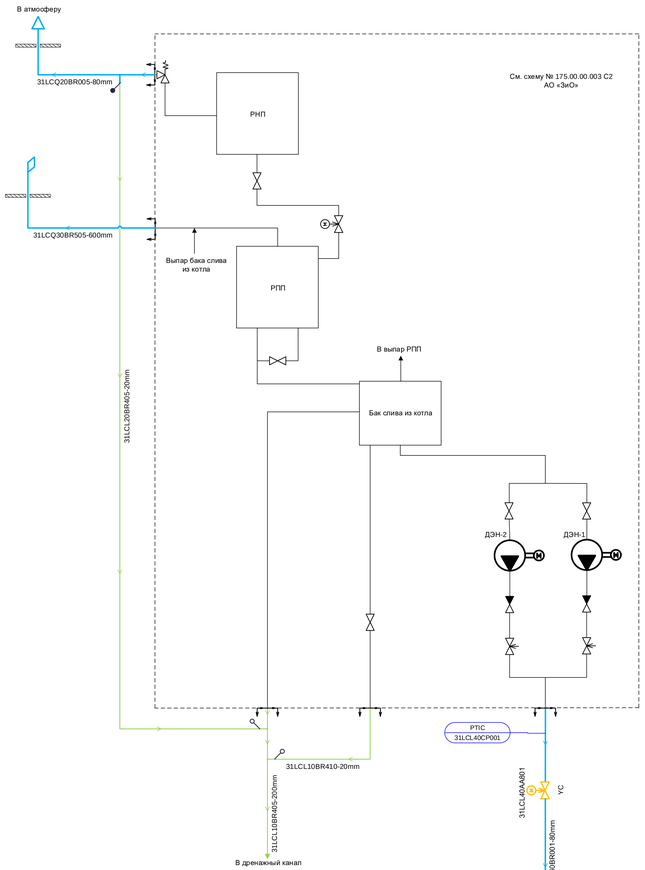


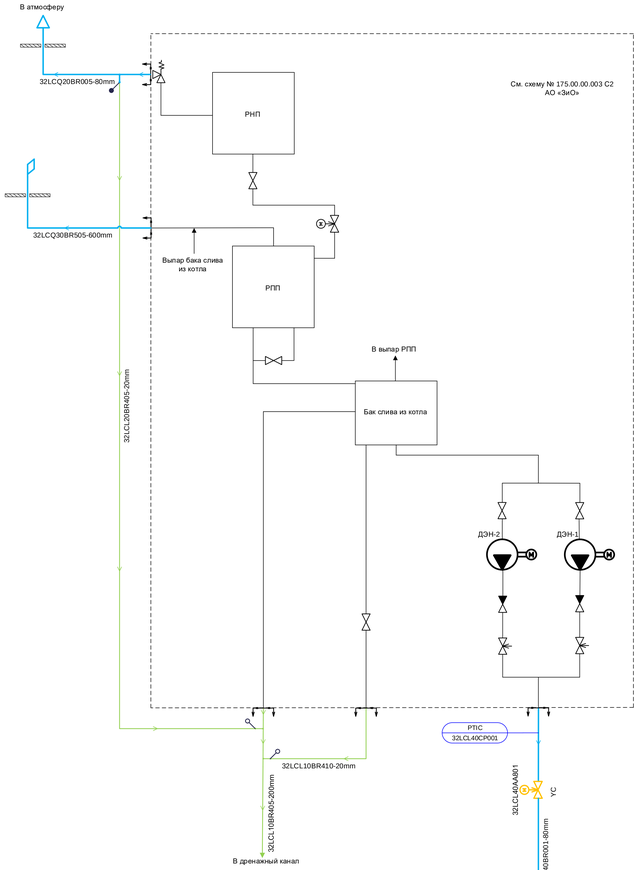


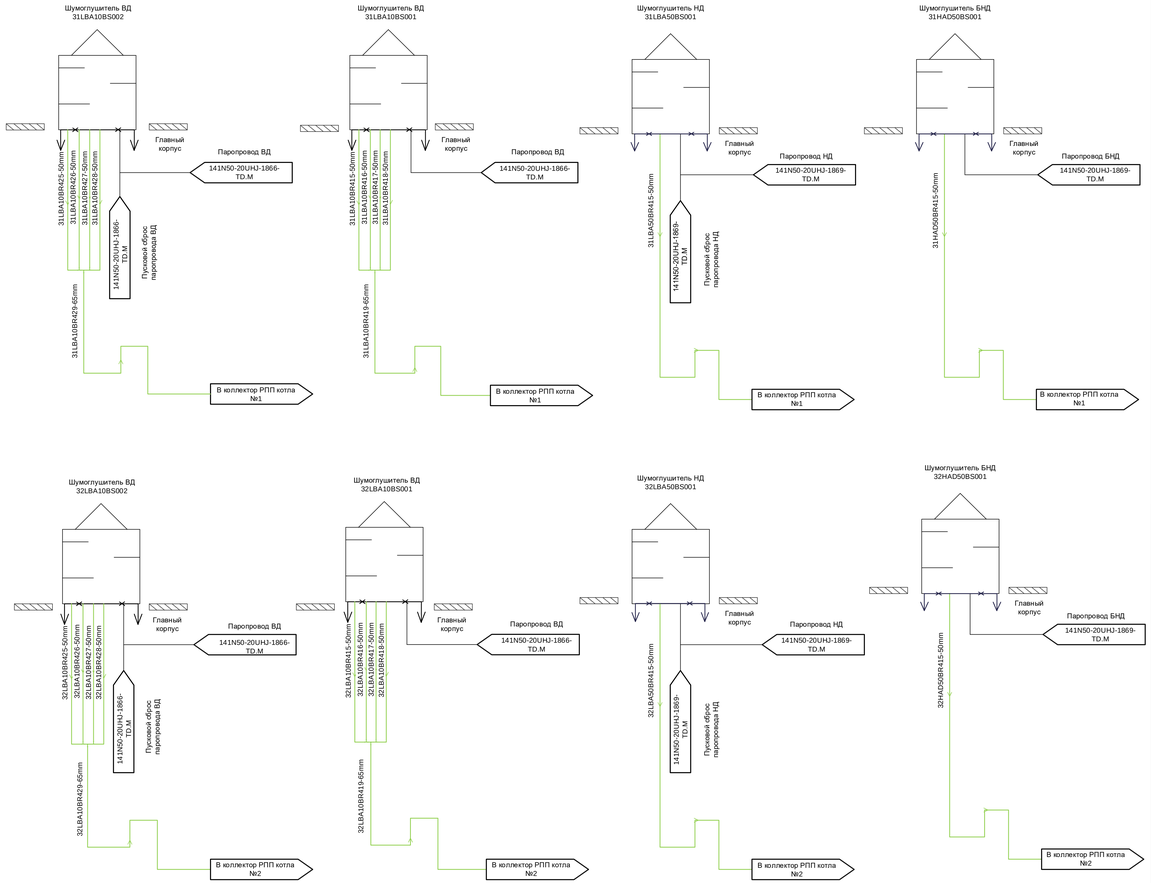


От коллектора основного конденсата

20UHJ-1857-TD.M_n.2 — 33LCA10BR410-80mm

В коллектор грязного конденсата

141N50-20UHJ-1833-TD.M — 31LCL40BR001-80mm — 03LCM05BR001-125mm

| | | | | | | | |
|---|---|---|---|---|---|---|---|
| Изм. | Кол.уч | Лист | № док. | Подп. | Дата | 141N50–20UHJ–1821–TD.M | |
| Разработал | Глухова | | | | | Расширение Свободненской ТЭС. Этап 1. Строительство энергоблока ПГУ 450 МВт со вспомогательными зданиями и сооружениями. Рабочая документация. | |
| Проверил | Стадуха | | | | | Главный корпус. P&I-диаграмма дренажей, воздушников и вспомогательных трубопроводов котла. | Стадия: Р; Лист: 2; Листов: |
| Гл.спец. | Черемнини | | | | | | |
| Н. контр. | Черемнини | | | | | P&I-диаграмма дренажей, воздушников и вспомогательных трубопроводов котла. | АКЦИОНЕРНОЕ ОБЩЕСТВО «ТЕХЭНЕРГОПРОМ» МОСКВА |

Согласовано

Взам. инв. №

Подпись и дата

Инв. № подл.

Формат А2х3