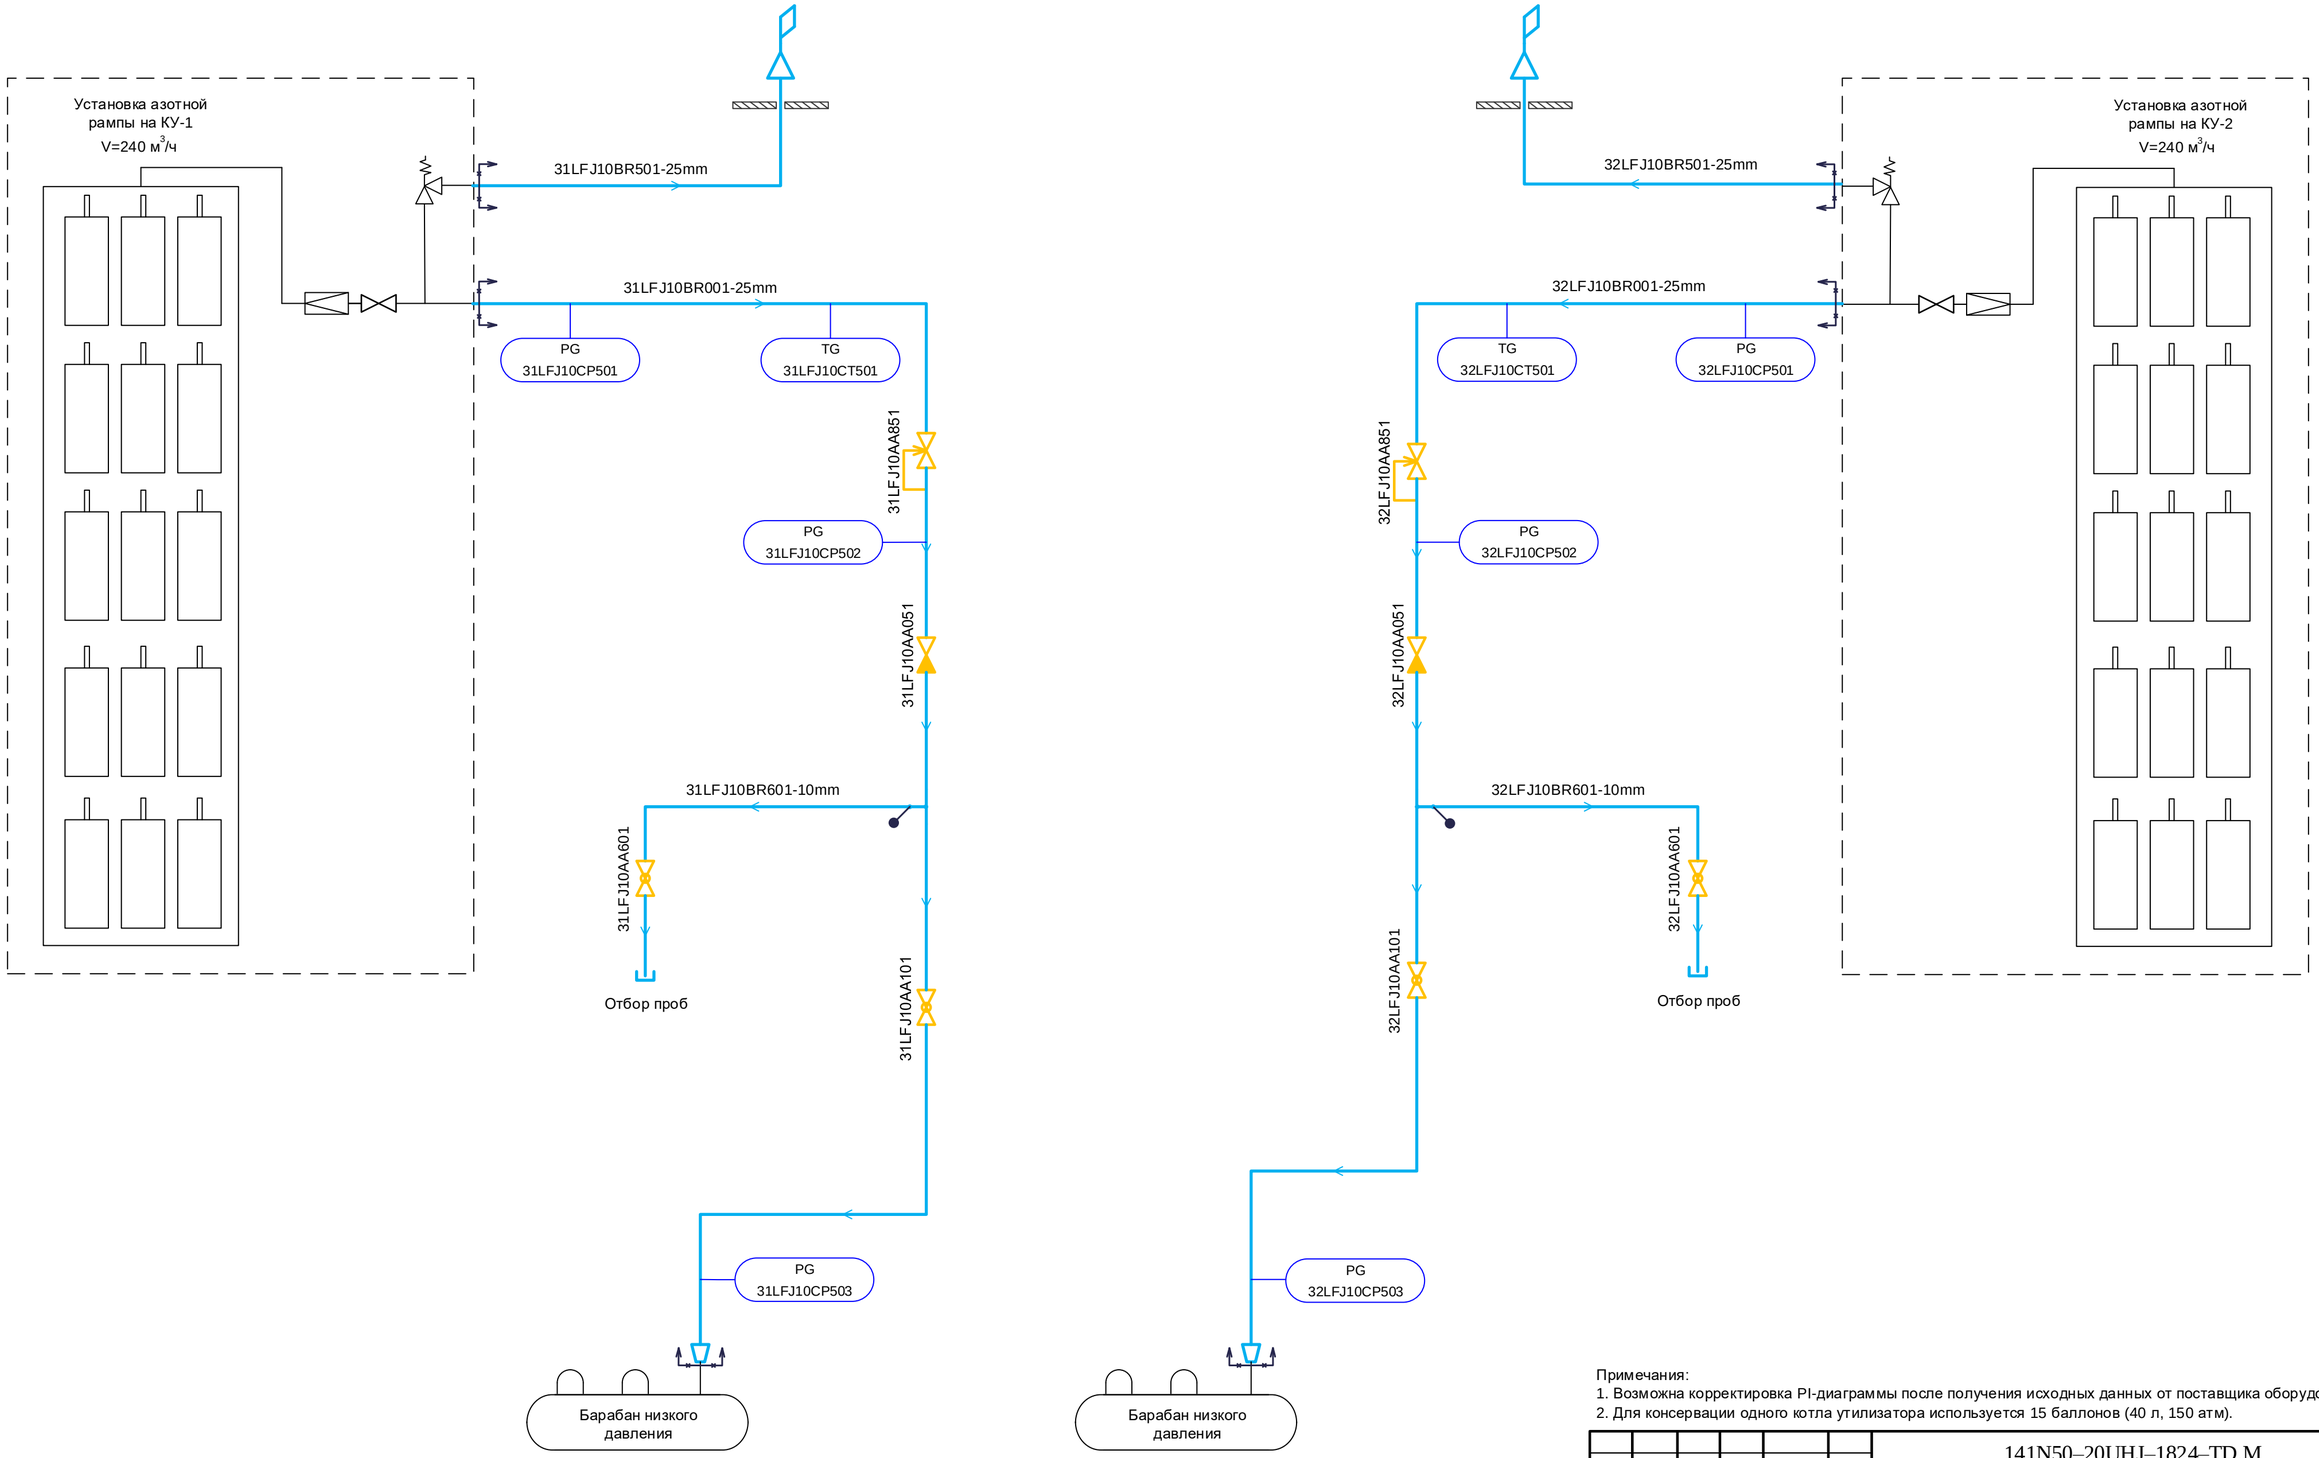

Примечания:
1. Возможна корректировка PI-диаграммы после получения исходных данных от поставщика оборудования;
2. Для консервации одного котла утилизатора используется 15 баллонов (40 л, 150 атм).

						141N50–20UHJ–1824–TD.M		
						Расширение Свободненской ТЭС. Этап 1. Строительство энергоблока ПГУ 450 МВт со вспомогательными зданиями и сооружениями. Рабочая документация.		
Изм.	Кол.уч	Лист	№ док.	Подп.	Дата			
Разработал		Гончар				Главный корпус. P&I-диаграмма трубопроводов азотной консервации.	Стадия	Лист	Листов
Проверил		Стацура					Р	2	
Н. контр.		Черёмушкина				P&I-диаграмма трубопроводов азотной консервации. Система LFJ.	АКЦИОНЕРНОЕ ОБЩЕСТВО ИНСТИТУТ ТЕПЛОЭЛЕКТРОПРОЕКТ Г. МОСКВА		

Согласовано

Взам. инв. №

Подпись и дата

Инв. № подл.

Формат А2