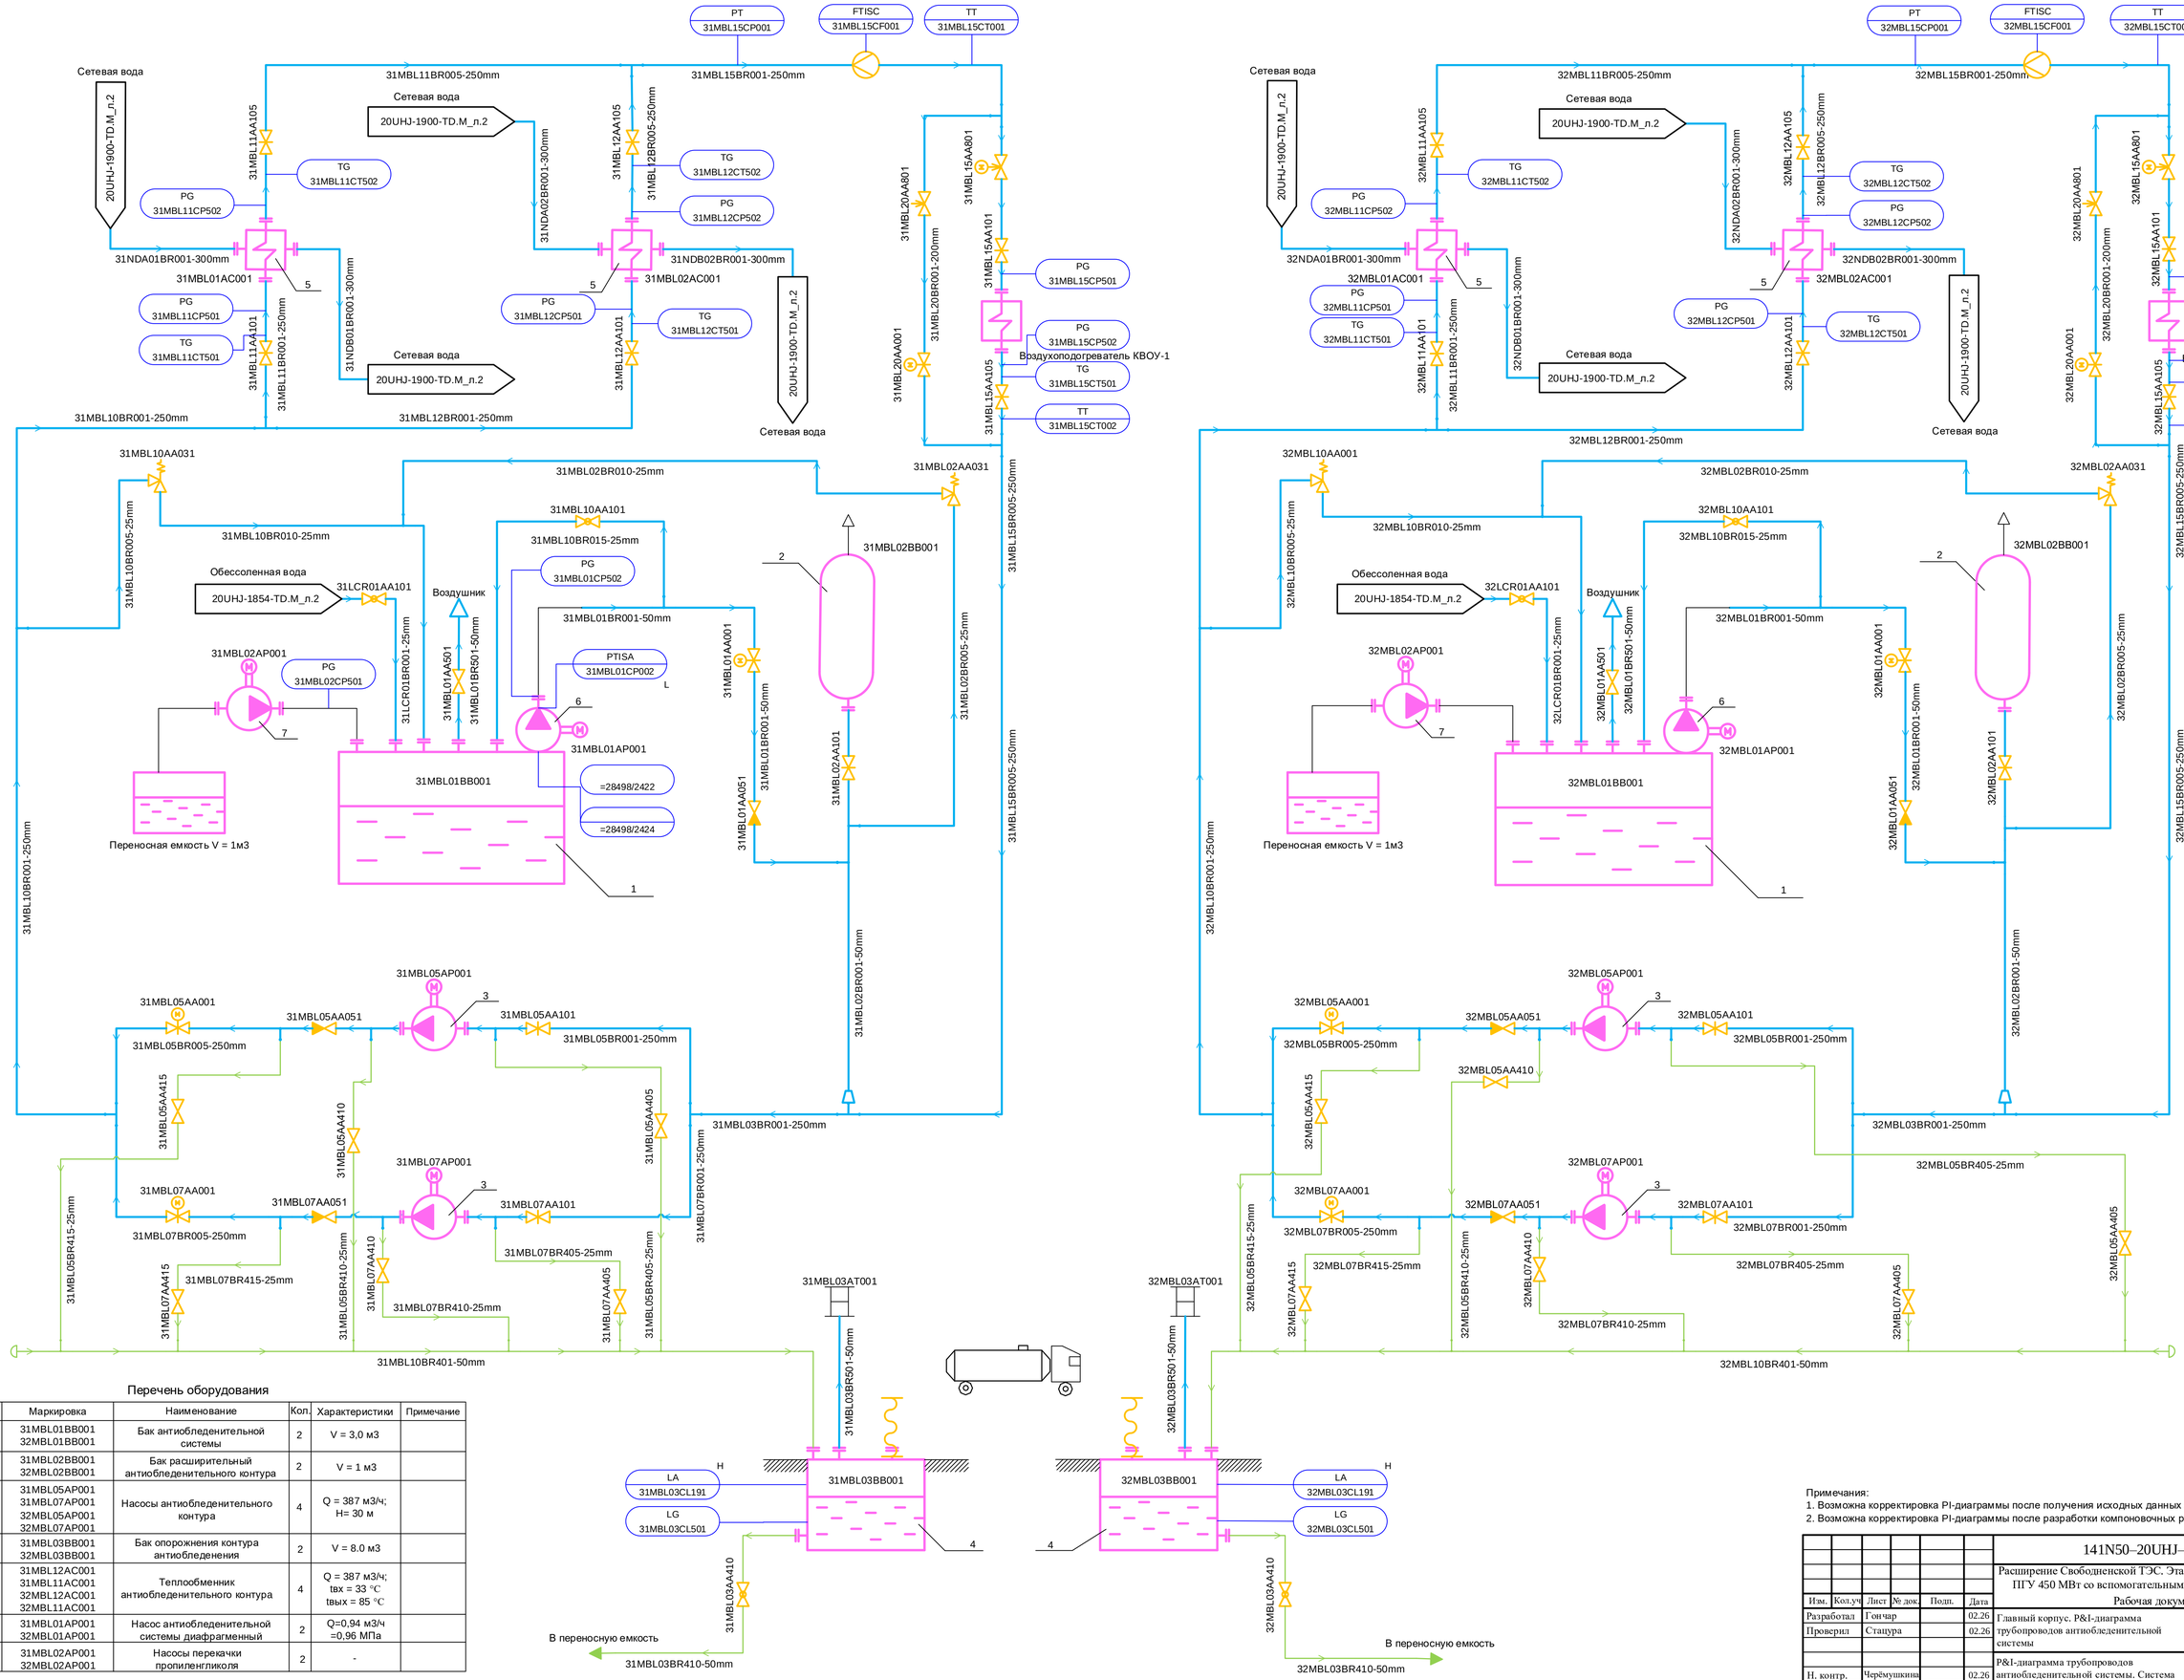

Перечень оборудования

Поз.	Маркировка	Наименование	Кол.	Характеристики	Примечание
1	31MBL01BB001 32MBL01BB001	Бак антиобледенительной системы	2	V = 3,0 м3	
2	31MBL02BB001 32MBL02BB001	Бак расширительный антиобледенительного контура	2	V = 1 м3	
3	31MBL05AP001 31MBL07AP001 32MBL05AP001 32MBL07AP001	Насосы антиобледенительного контура	4	Q = 387 м3/ч; H= 30 м	
4	31MBL03BB001 32MBL03BB001	Бак опорожнения контура антиобледенения	2	V = 8.0 м3	
5	31MBL12AC001 31MBL11AC001 32MBL12AC001 32MBL11AC001	Теплообменник антиобледенительного контура	4	Q = 387 м3/ч; tвх = 33 °С tвых = 85 °С	
6	31MBL01AP001 32MBL01AP001	Насос антиобледенительной системы диафрагменный	2	Q=0,94 м3/ч =0,96 МПа	
7	31MBL02AP001 32MBL02AP001	Насосы перекачки пропиленгликоля	2	-	

Примечания:
1. Возможна корректировка PI-диаграммы после получения исходных данных от поставщиков оборудования;
2. Возможна корректировка PI-диаграммы после разработки компоновочных решений.

						141N50–20UHJ–1827–TD.M			
						Расширение Свободненской ТЭС. Этап 1. Строительство энергоблока ПГУ 450 МВт со вспомогательными зданиями и сооружениями. Рабочая документация.			
Изм.	Кол.уч	Лист	№ док.	Подп.	Дата				
Разработал		Гончар			02.26	Главный корпус. P&I-диаграмма трубопроводов антиобледенительной системы	Стадия	Лист	Листов
Проверил		Стацура			02.26		Р	2	
Н. контр.		Черёмушкина			02.26	P&I-диаграмма трубопроводов антиобледенительной системы. Система MBL.	АКЦИОНЕРНОЕ ОБЩЕСТВО ИНСТИТУТ ТЕПЛОЭЛЕКТРОПРОЕКТ г. МОСКВА		

Согласовано

Взам. инв. №

Подпись и дата

Инв. № подл.

Формат А1