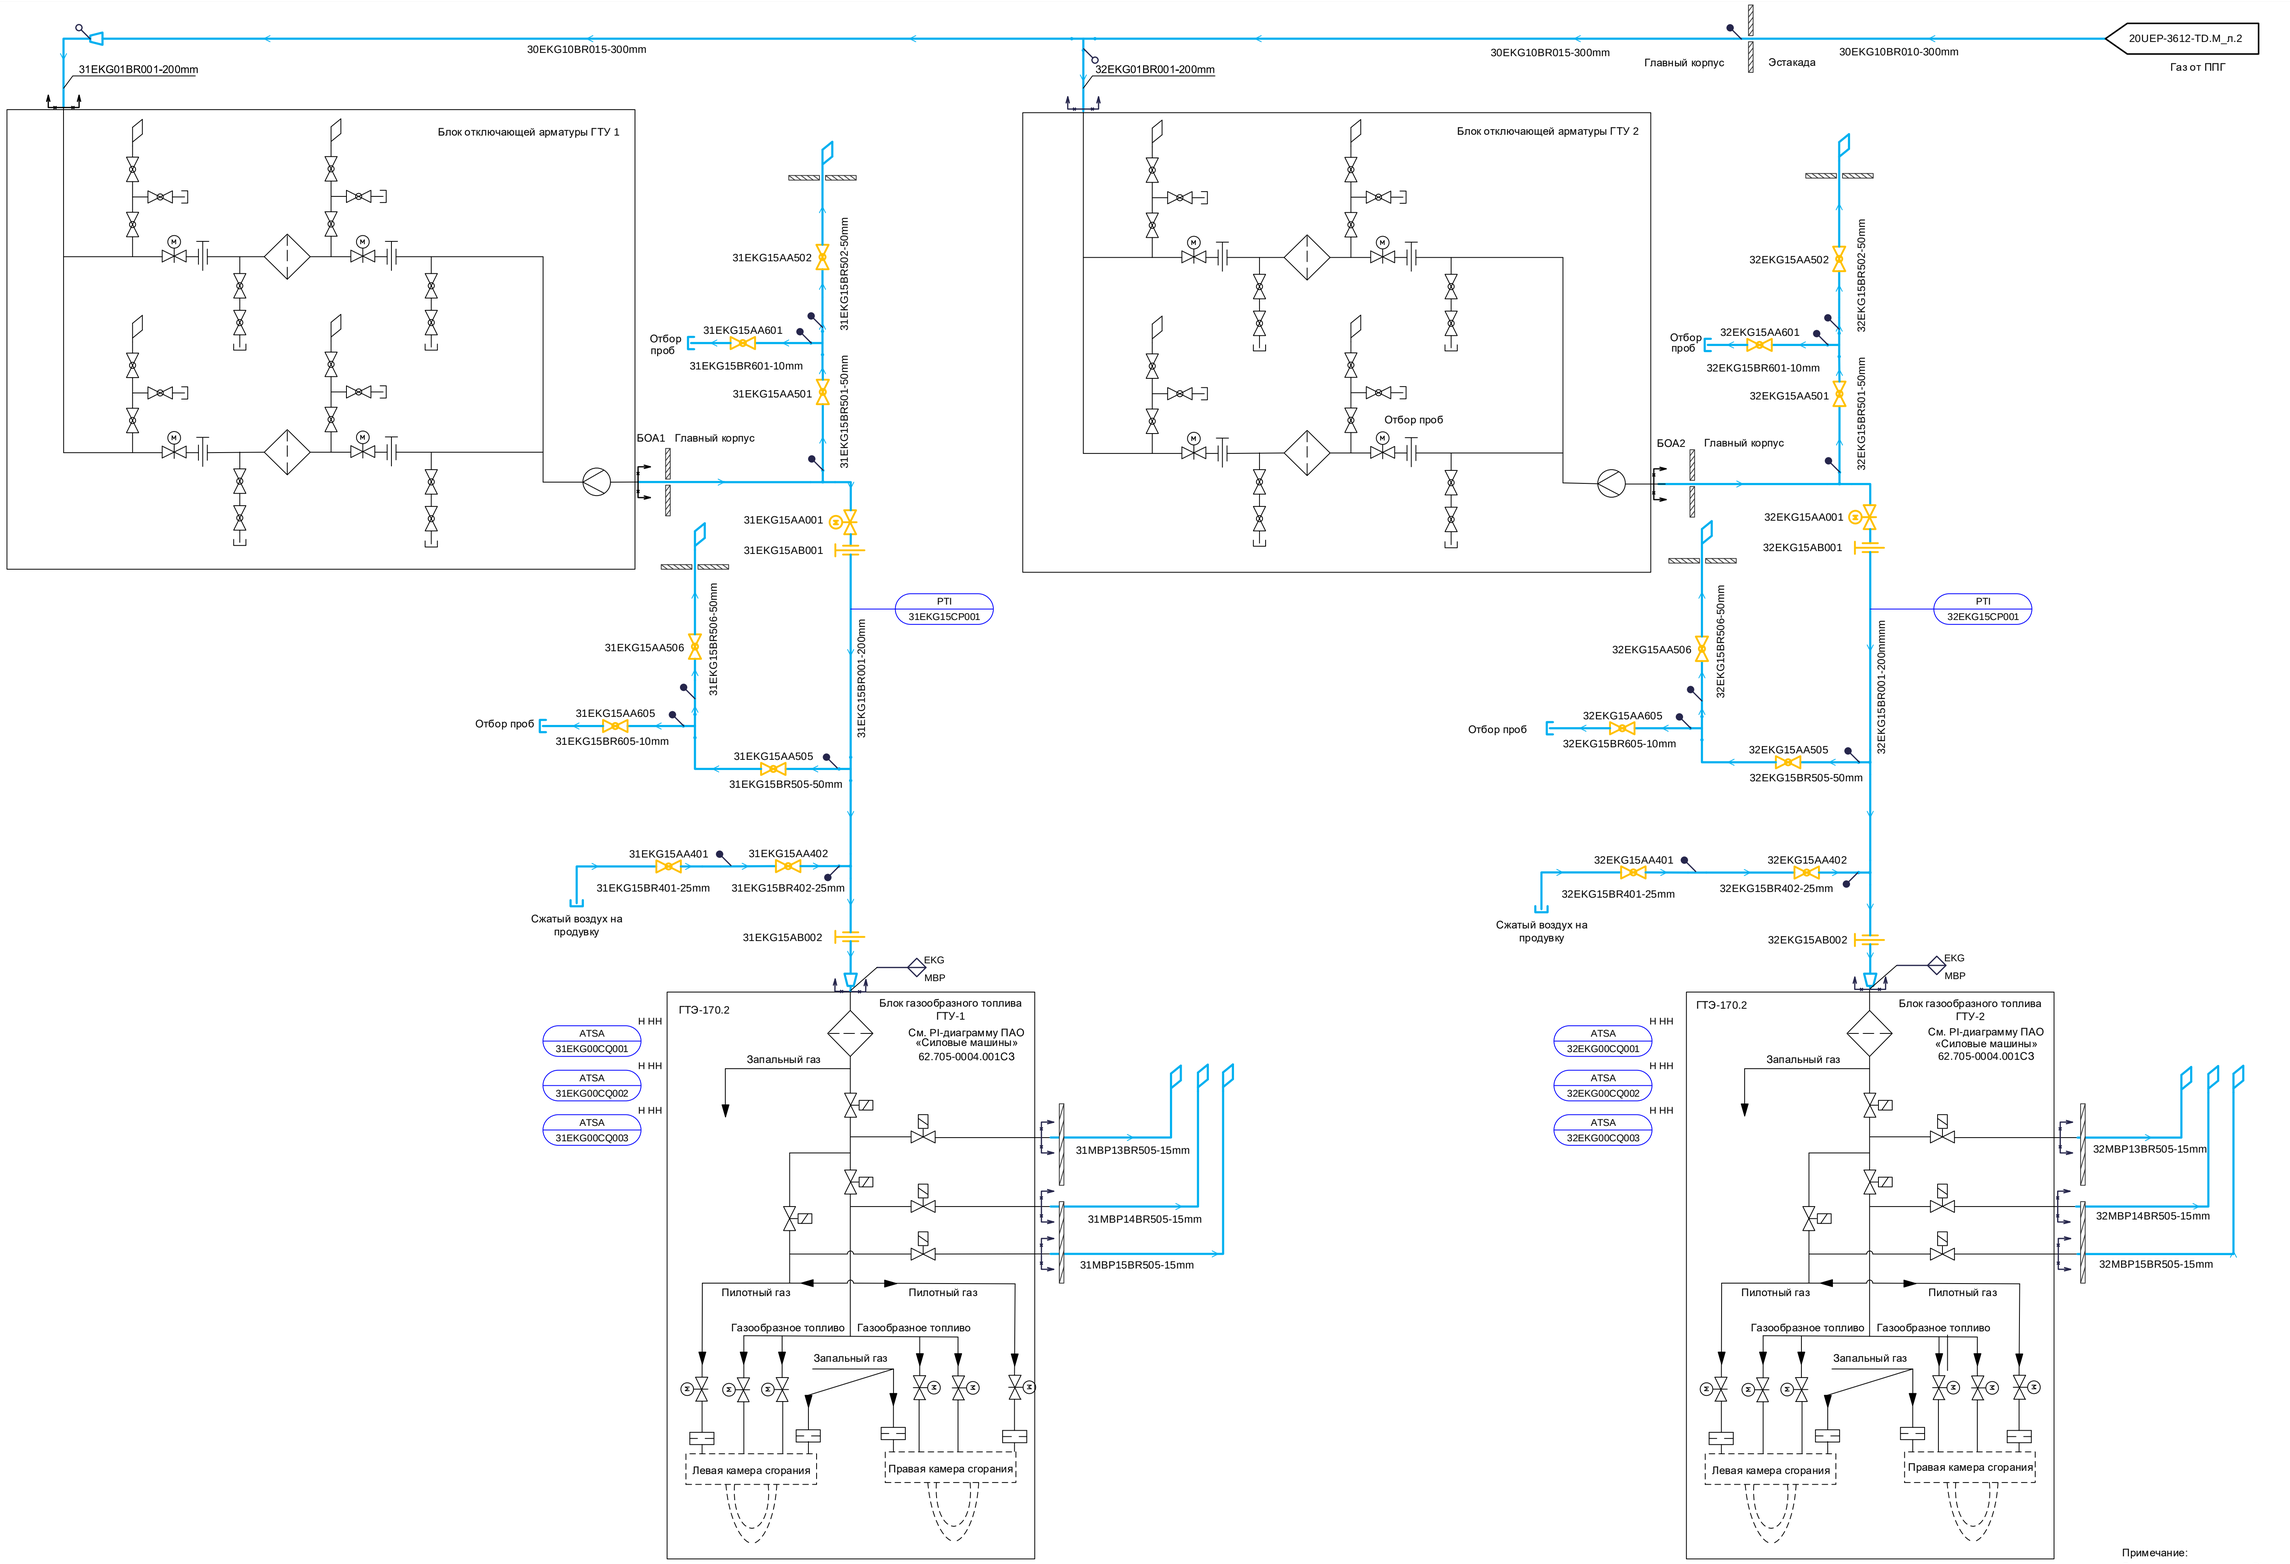

Примечание:

Возможна корректировка PI-диаграммы после выбора поставщика БОА и получения от них исходных данных.

Изм.	Кол.уч	Лист	№ док.	Подп.	Дата	144N50 – 20UHJ – 1830 – TD.M
						Расширение Свободненской ТЭС. Этап 1. Строительство энергоблока ПГУ 450 МВт со вспомогательными зданиями и сооружениями. Рабочая документация
Разработал		Полянская				Здание главного корпуса. PI-диаграмма трубопроводов газового топлива. Газопроводы ГТУ.
Проверил		Стацура				
Н. контр.		Черемушкина				PI-Диаграмма трубопроводов газового топлива. Газопроводы ГТУ. Система EKG

Стадия	Лист	Листов
Р	2	

АКЦИОНЕРНОЕ ОБЩЕСТВО ИНСТИТУТ ТЕПЛОЭЛЕКТРОПРОЕКТ г. МОСКВА

Согласовано

Взам. инв. №

Подпись и дата

Инв. № подл.

Формат А1