## Перечень оборудования

| Поз. | Маркировка | Наименование | Кол. | Характеристики | Примечание |
|---|---|---|---|---|---|
| 1 | 03LCM10BB001 | Бак «грязного» конденсата | 1 | V=1000 м3 | |
| 2 | 03LCM11AP001<br>03LCM12AP001 | Насос бака «грязного» конденсата | 2 | Q=70 м3/ч;<br>H=1,8 МПа | |
| 3 | 03LCM21AC001<br>03LCM22AC001 | Охладители «грязного» конденсата | 2 | | |

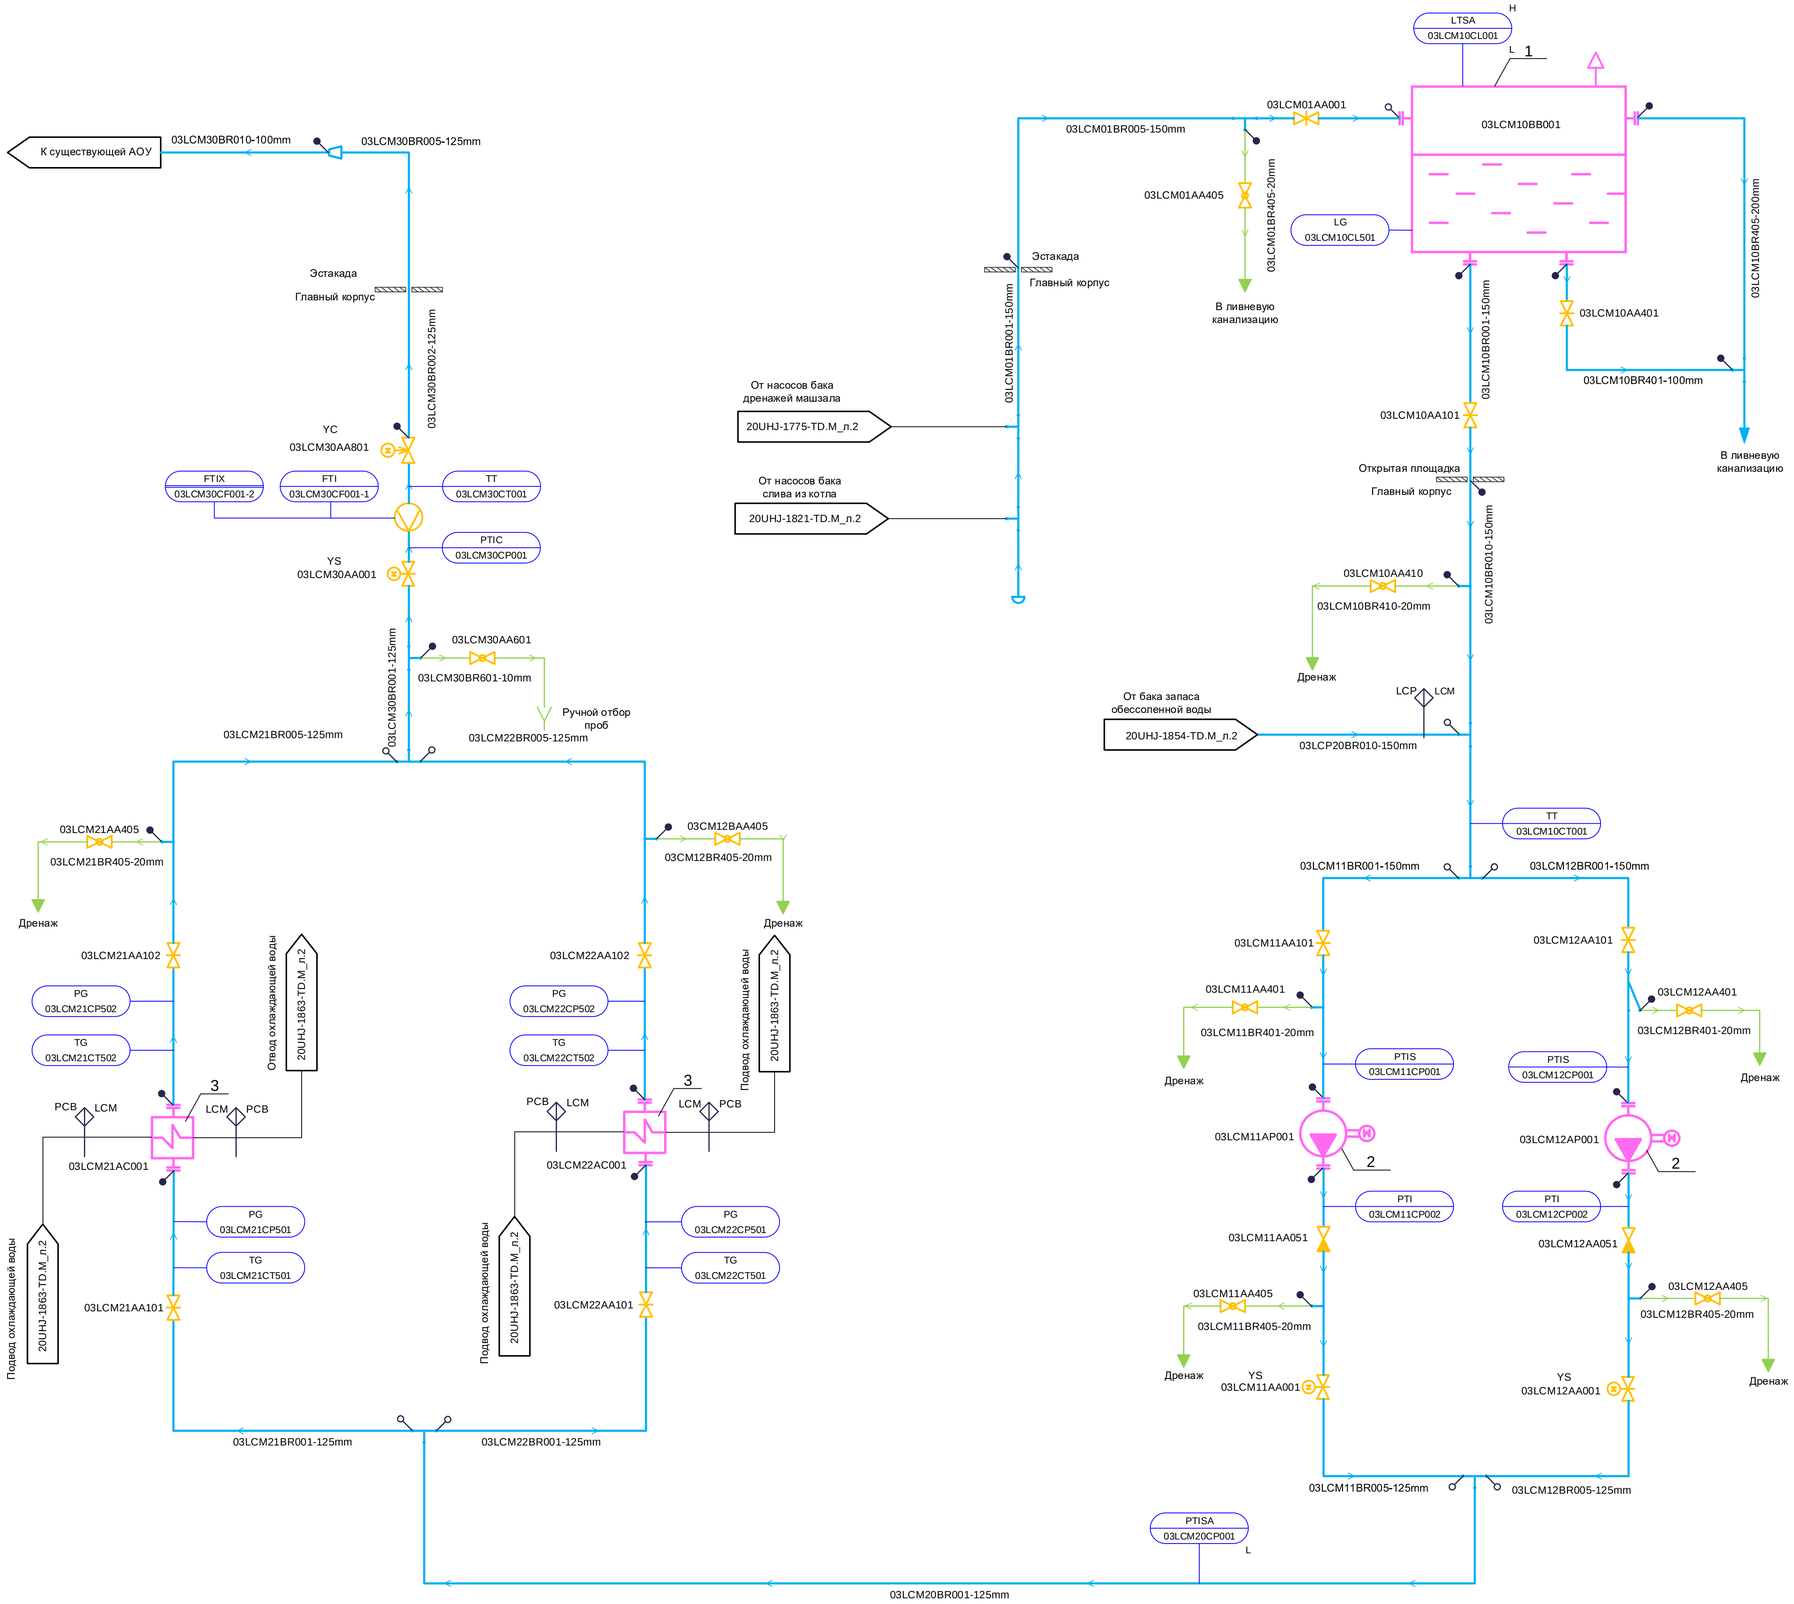


Согласовано

Взам. инв. №

Подпись и дата

Инв. № подл.

| Изм. | Кол.уч | Лист | № док. | Подп. | Дата |
|---|---|---|---|---|---|
| Разработал | | Салищева | | | |
| Проверил | | Стацура | | | |
| Н. контр. | | Черёмушкина | | | |

141N50–20UHJ–1833–TD.L

Расширение Свободненской ТЭС. Этап 1. Строительство энергоблока ПГУ 450 МВт со вспомогательными зданиями и сооружениями. Рабочая документация.

Главный корпус. P&I-диаграмма трубопроводов грязного конденсата. Локальное задание

P&I-диаграмма трубопроводов грязного конденсата

| Стадия | Лист | Листов |
|---|---|---|
| Р | 2 | |

АКЦИОНЕРНОЕ ОБЩЕСТВО ИНСТИТУТ ТЕПЛОЭЛЕКТРОПРОЕКТ г. МОСКВА

Формат А1