Перечень оборудования

Поз.	Маркировка	Наименование	Кол.	Характеристики	Примечание
1	03LCP11BB001 03LCP12BB001	Бак запаса обессоленной воды	2	V=1000 м3	
2	03LCP21AP001 03LCP22AP001	Насос «нормального» добавка	2	Q=12 м3/ч; H=0,65 МПа	
3	03LCP31AP001 03LCP32AP001	Насос «аварийного» добавка	2	Q=92 м3/ч; H=0,65 МПа	

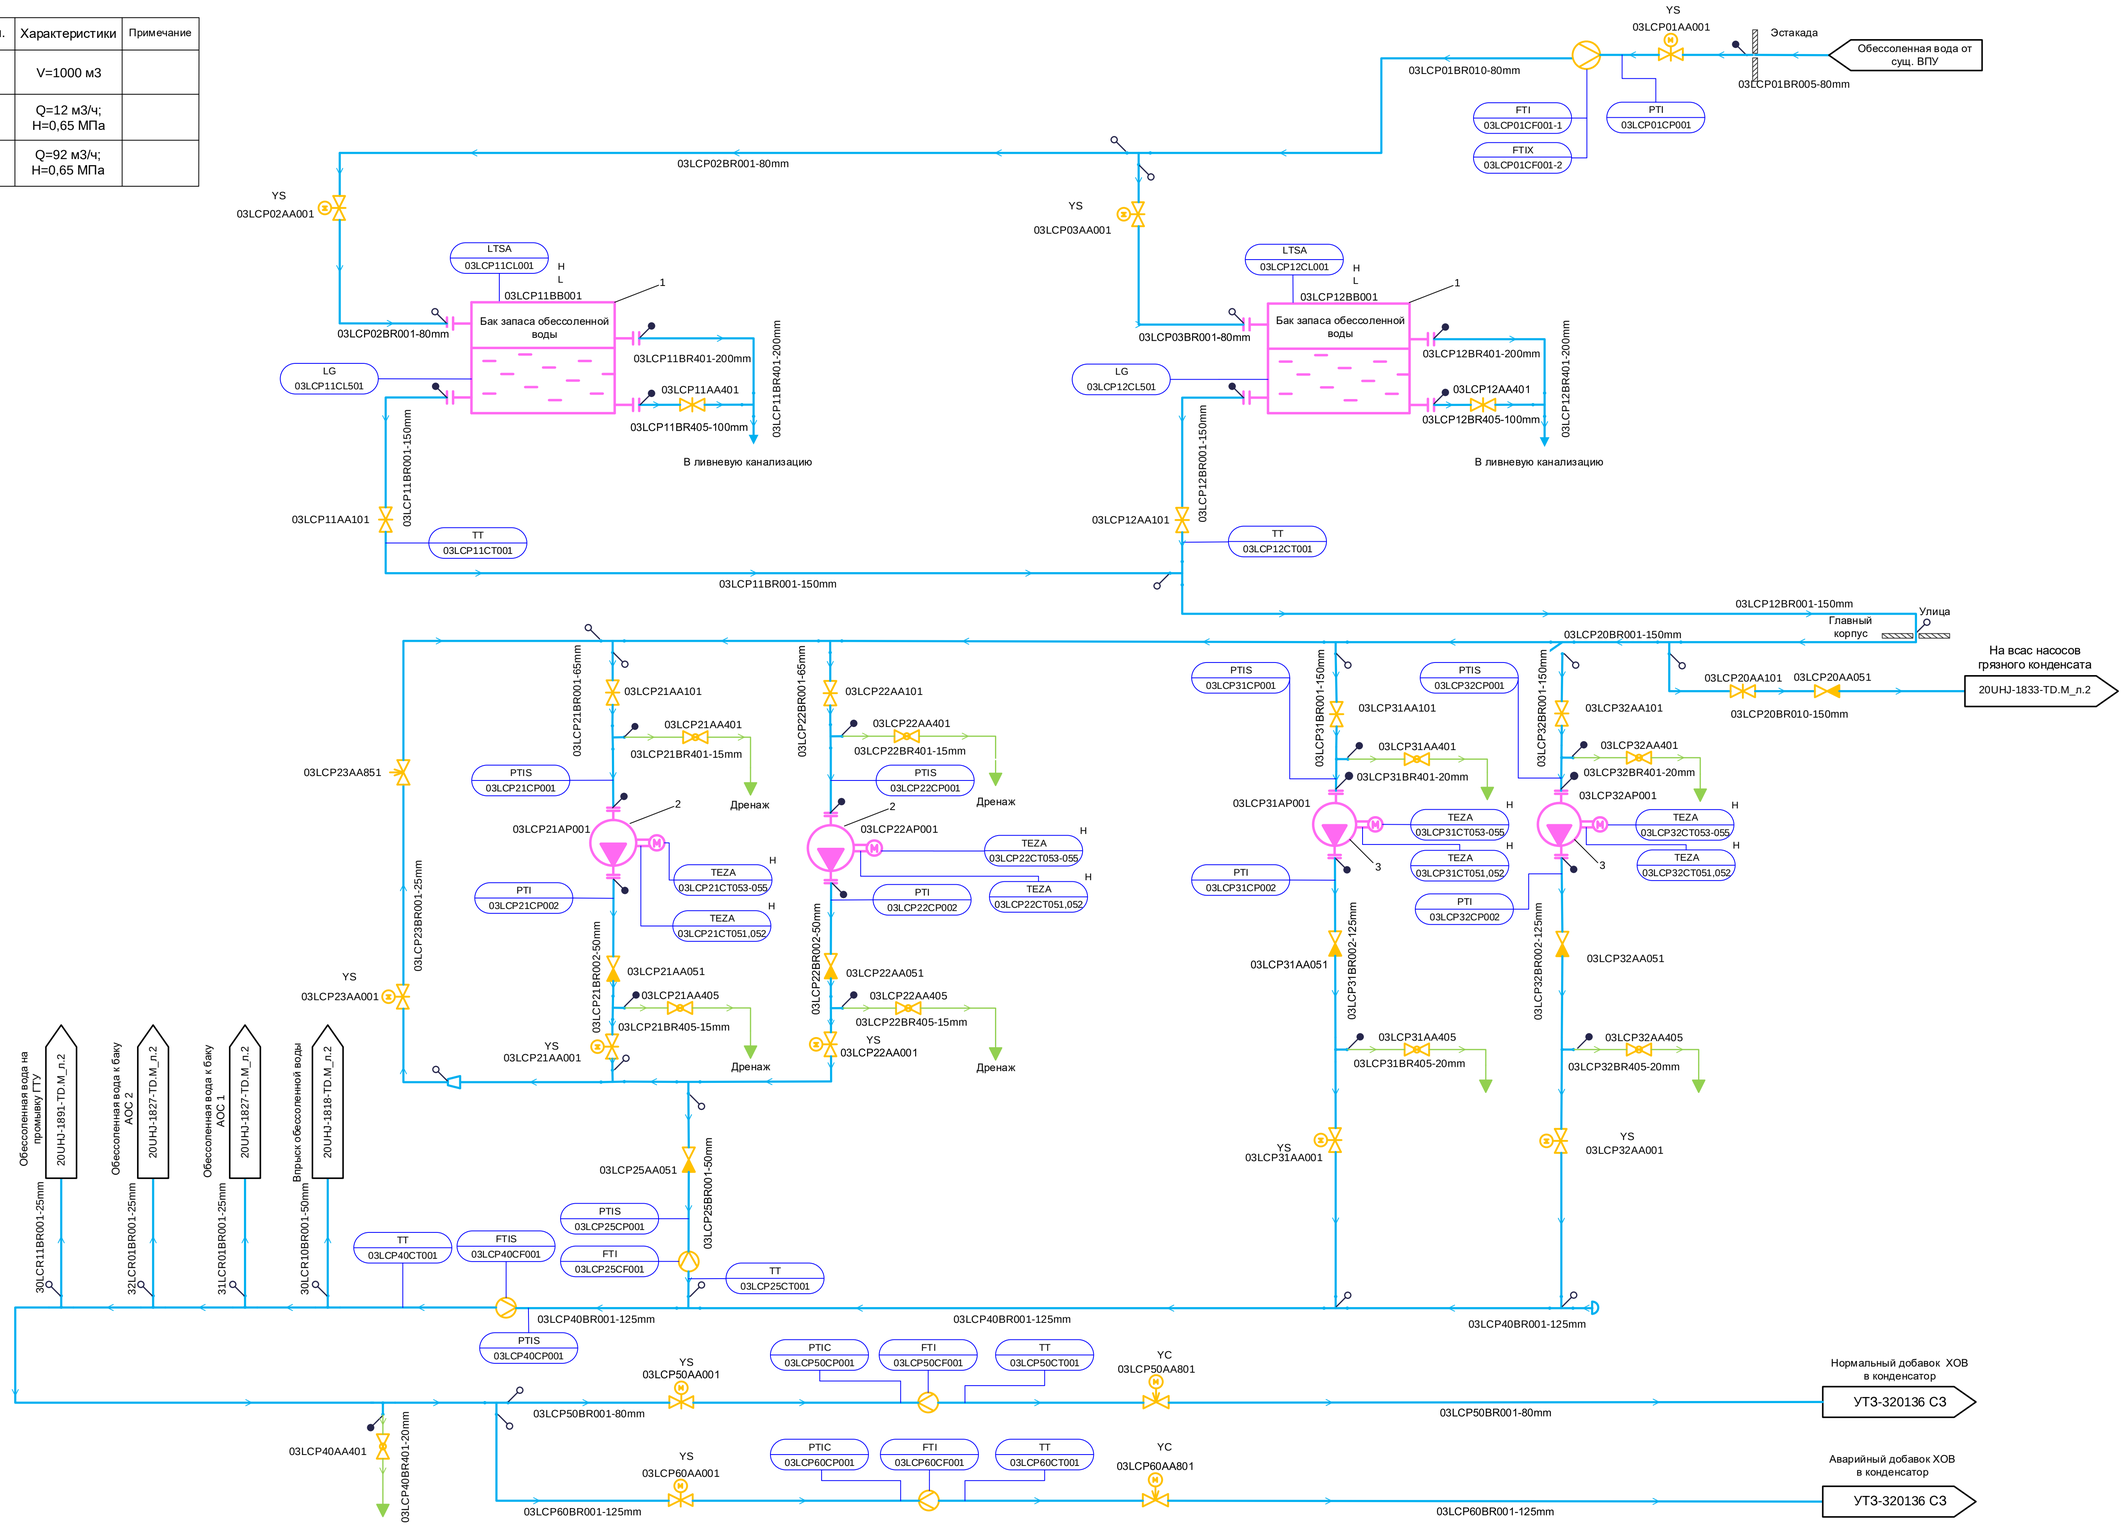

Согласовано

Взам. инв. №

Подпись и дата

Инв. № подл.

Изм.	Кол.уч	Лист	№ док.	Подп.	Дата
Разработал	Глухова				
Проверил	Салищева				
Гл.спец.	Черемикин				
Гл.спец.	Стацура				
Н. контр.	Черемушкина				

141N50–20UHJ–1854–TD.L

Расширение Свободненской ТЭС. Этап 1. Строительство энергоблока ПГУ 450 МВт со вспомогательными зданиями и сооружениями. Рабочая документация.

Главный корпус. P&I-диаграмма трубопроводов обессоленной воды. Локальное задание.

P&I-диаграмма трубопроводов обессоленной воды.

Стадия	Лист	Листов
Р	2	

АКЦИОНЕРНОЕ ОБЩЕСТВО ИНСТИТУТ ТЕПЛОЭЛЕКТРОПРОЕКТ г. МОСКВА

Формат А1