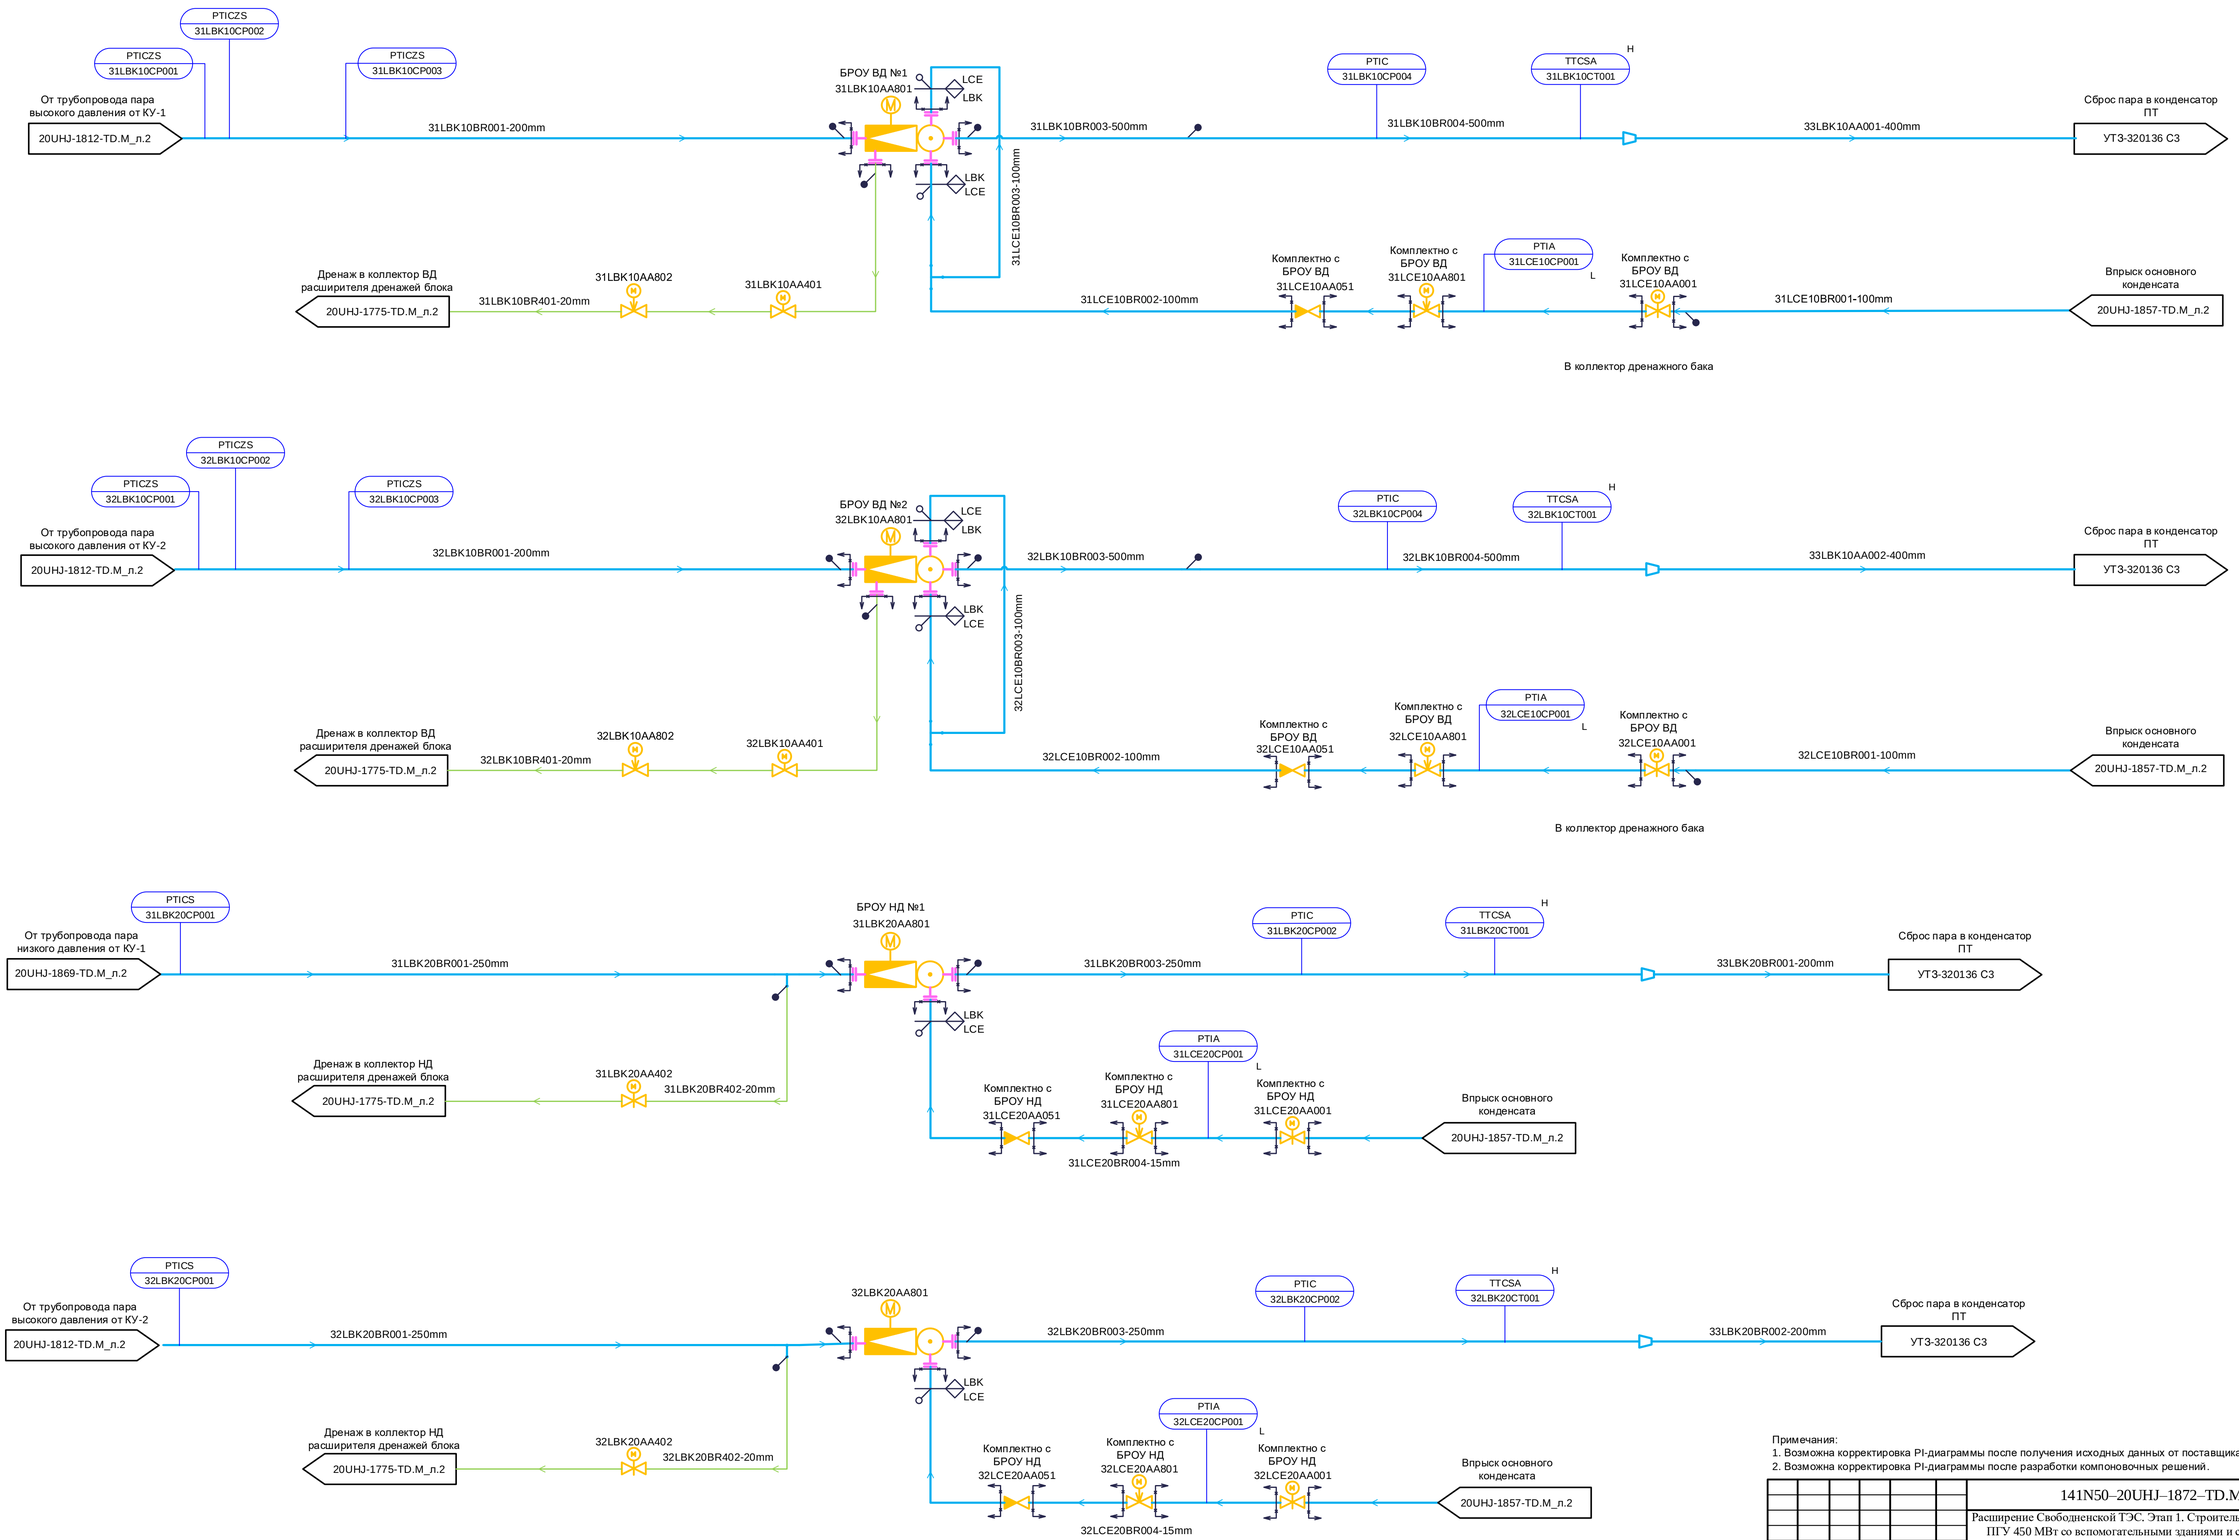

Примечания:
1. Возможна корректировка PI-диаграммы после получения исходных данных от поставщика оборудования;
2. Возможна корректировка PI-диаграммы после разработки компоновочных решений.

Изм.	Кол.уч	Лист	№ док.	Подп.	Дата	141N50–20UHJ–1872–TD.M			
						Расширение Свободненской ТЭС. Этап 1. Строительство энергоблока ПГУ 450 МВт со вспомогательными зданиями и сооружениями. Рабочая документация.			
Разработал		Гончар				Главный корпус. P&I-диаграмма трубопроводов БРОУ	Стадия	Лист	Листов
Проверил		Стацура					Р	2	
Н. контр.		Черёмушкина				P&I-диаграмма трубопроводов БРОУ. Система LBK, LCE.			

Согласовано

Взам. инв. №

Подпись и дата

Инв. № подл.

Формат А1