Перечень оборудования

Поз.	Маркировка	Наименование	Кол.	Характеристики	Примечание
1	30NDK11AP001 30NDK12AP001	Насос аврийной подпитки теплосети	2	G = 32 м^3/ч * H = 35 м *	
2	30NDK11AT001 30NDK12AT001	Фильтр	2	G = 32 м^3/ч *	

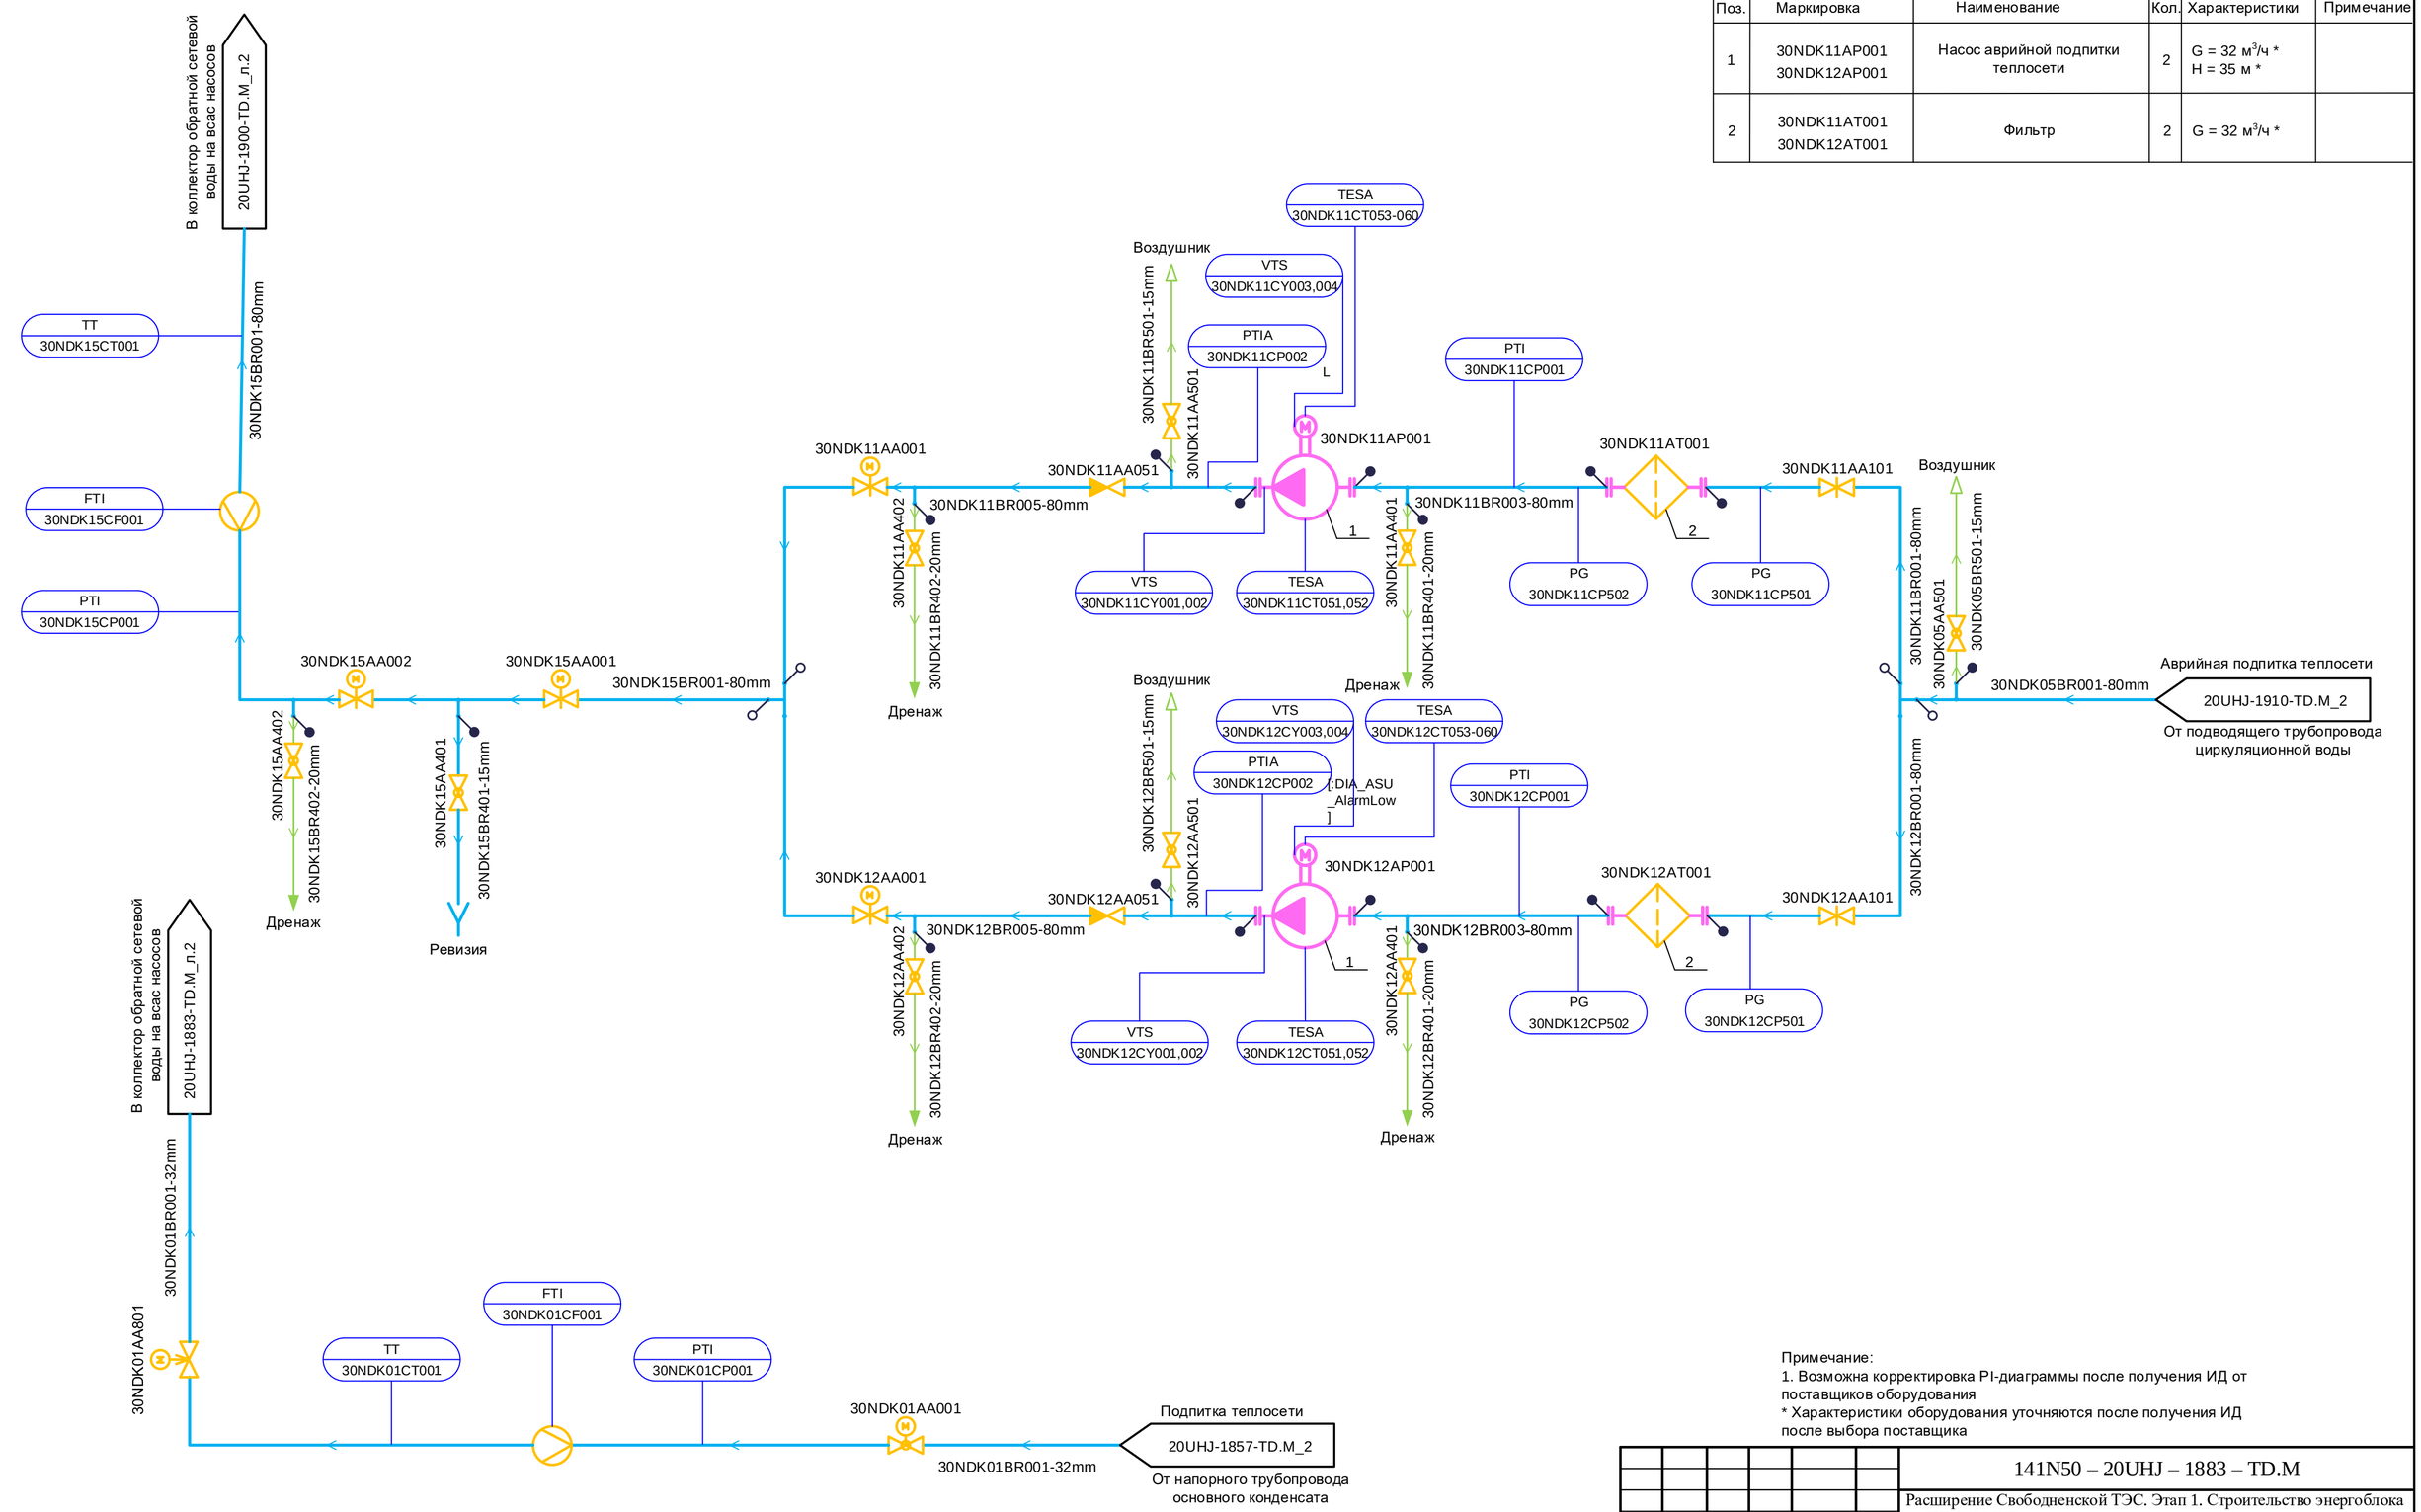

Примечание:
1. Возможна корректировка PI-диаграммы после получения ИД от поставщиков оборудования
* Характеристики оборудования уточняются после получения ИД после выбора поставщика

Изм.	Кол.уч	Лист	№ док.	Подп.	Дата
Разработал		Брылева			01.26
Проверил		Стацура			01.26
Н. контр.		Черемушкина			01.26

141N50 – 20UHJ – 1883 – TD.M

Расширение Свободненской ТЭС. Этап 1. Строительство энергоблока ПГУ 450 МВт со вспомогательными зданиями и сооружениями.

Рабочая документация.

Здание главного корпуса. PI-диаграмма трубопроводов подпитки теплосети

Стадия	Лист	Листов
Р	2	

PI-диаграмма трубопроводов подпитки теплосети. Система NDK

АКЦИОНЕРНОЕ ОБЩЕСТВО ИНСТИТУТ ТЕПЛОЭЛЕКТРОПРОЕКТ Г. МОСКВА

Согласовано
ОАСУ Доделцева
Взам. инв. №
Подпись и дата
Инв. № подл.

Формат А2