Перечень оборудования

Поз.	Маркировка	Наименование	Кол.	Характеристики	Примечание
1	30NDE10AP001	Насос бака сбора чистых стоков (полупогружной)	1	G = 25 м^3/ч * H = 20 м *	
2	30NDE10BB001	Бак сбора чистых стоков	1	V = 100 м^3	

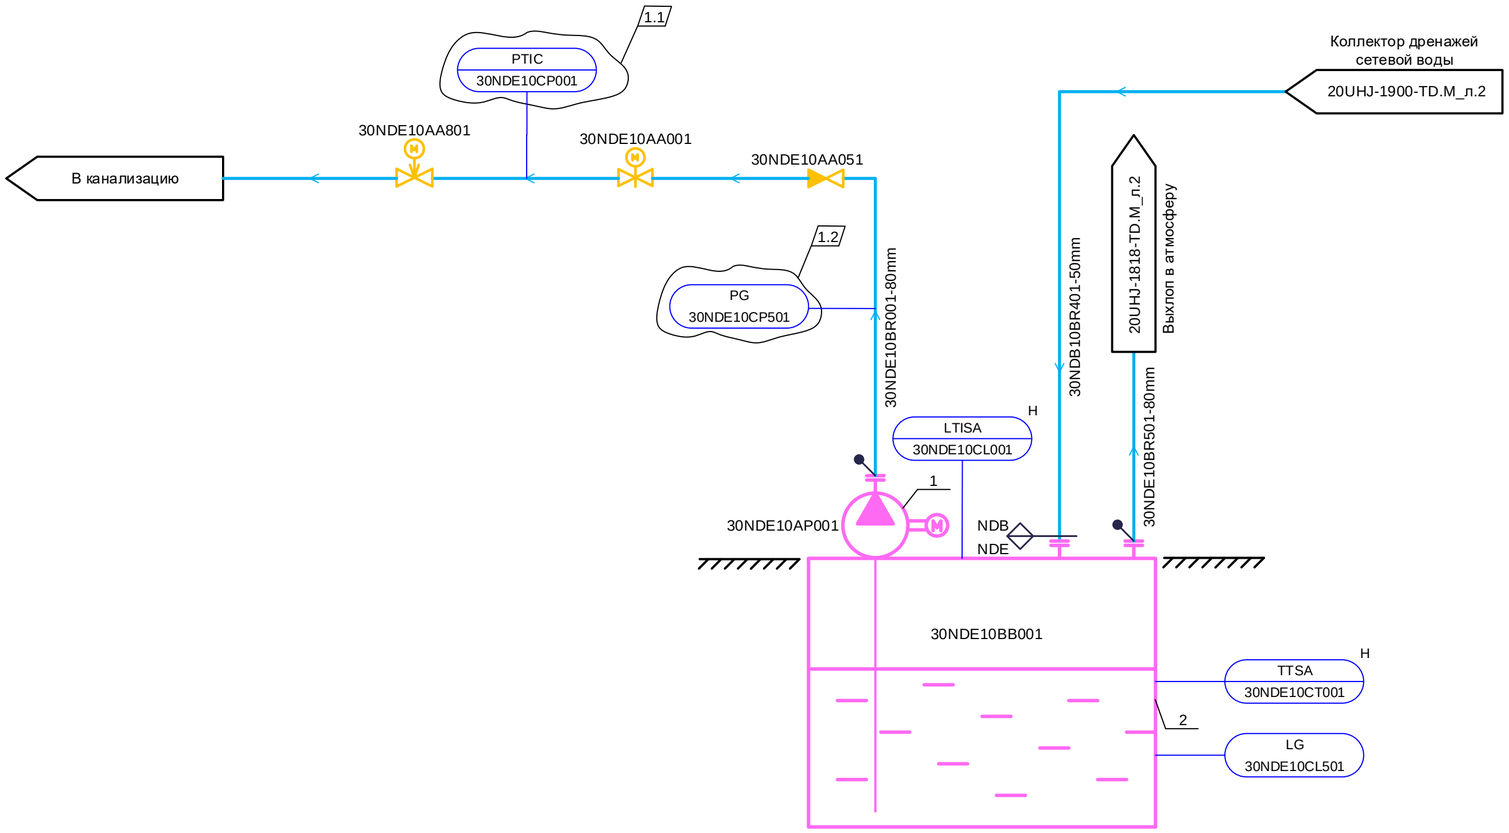

Примечание:
1. Возможна корректировка PI-диаграммы после получения ИД от поставщиков оборудования
* Характеристики оборудования уточняются после получения ИД после выбора поставщика

1	2	Зам.	896-26		02.26	141N50 – 20UHJ – 1894 – TD.M
Изм.	Кол.уч	Лист	№ док.	Подп.	Дата	Расширение Свободненской ТЭС. Этап 1. Строительство энергоблока ПГУ 450 МВт со вспомогательными зданиями и сооружениями. Рабочая документация.
Разработал		Брылева				Здание главного корпуса. P&I-диаграмма трубопроводов сбора дренажей сетевой воды
Проверил		Стацура				Стадия: Р; Лист: 2; Листов:
Н. контр.		Черемушкина				P&I-диаграмма трубопроводов сбора дренажей сетевой воды. Система NDE, NDB

АКЦИОНЕРНОЕ ОБЩЕСТВО ИНСТИТУТ ТЕПЛОЭЛЕКТРОПРОЕКТ Г. МОСКВА

Согласовано: ОАСУ, Доделышева

Взам. инв. №

Подпись и дата

Инв. № подл.

Формат А2