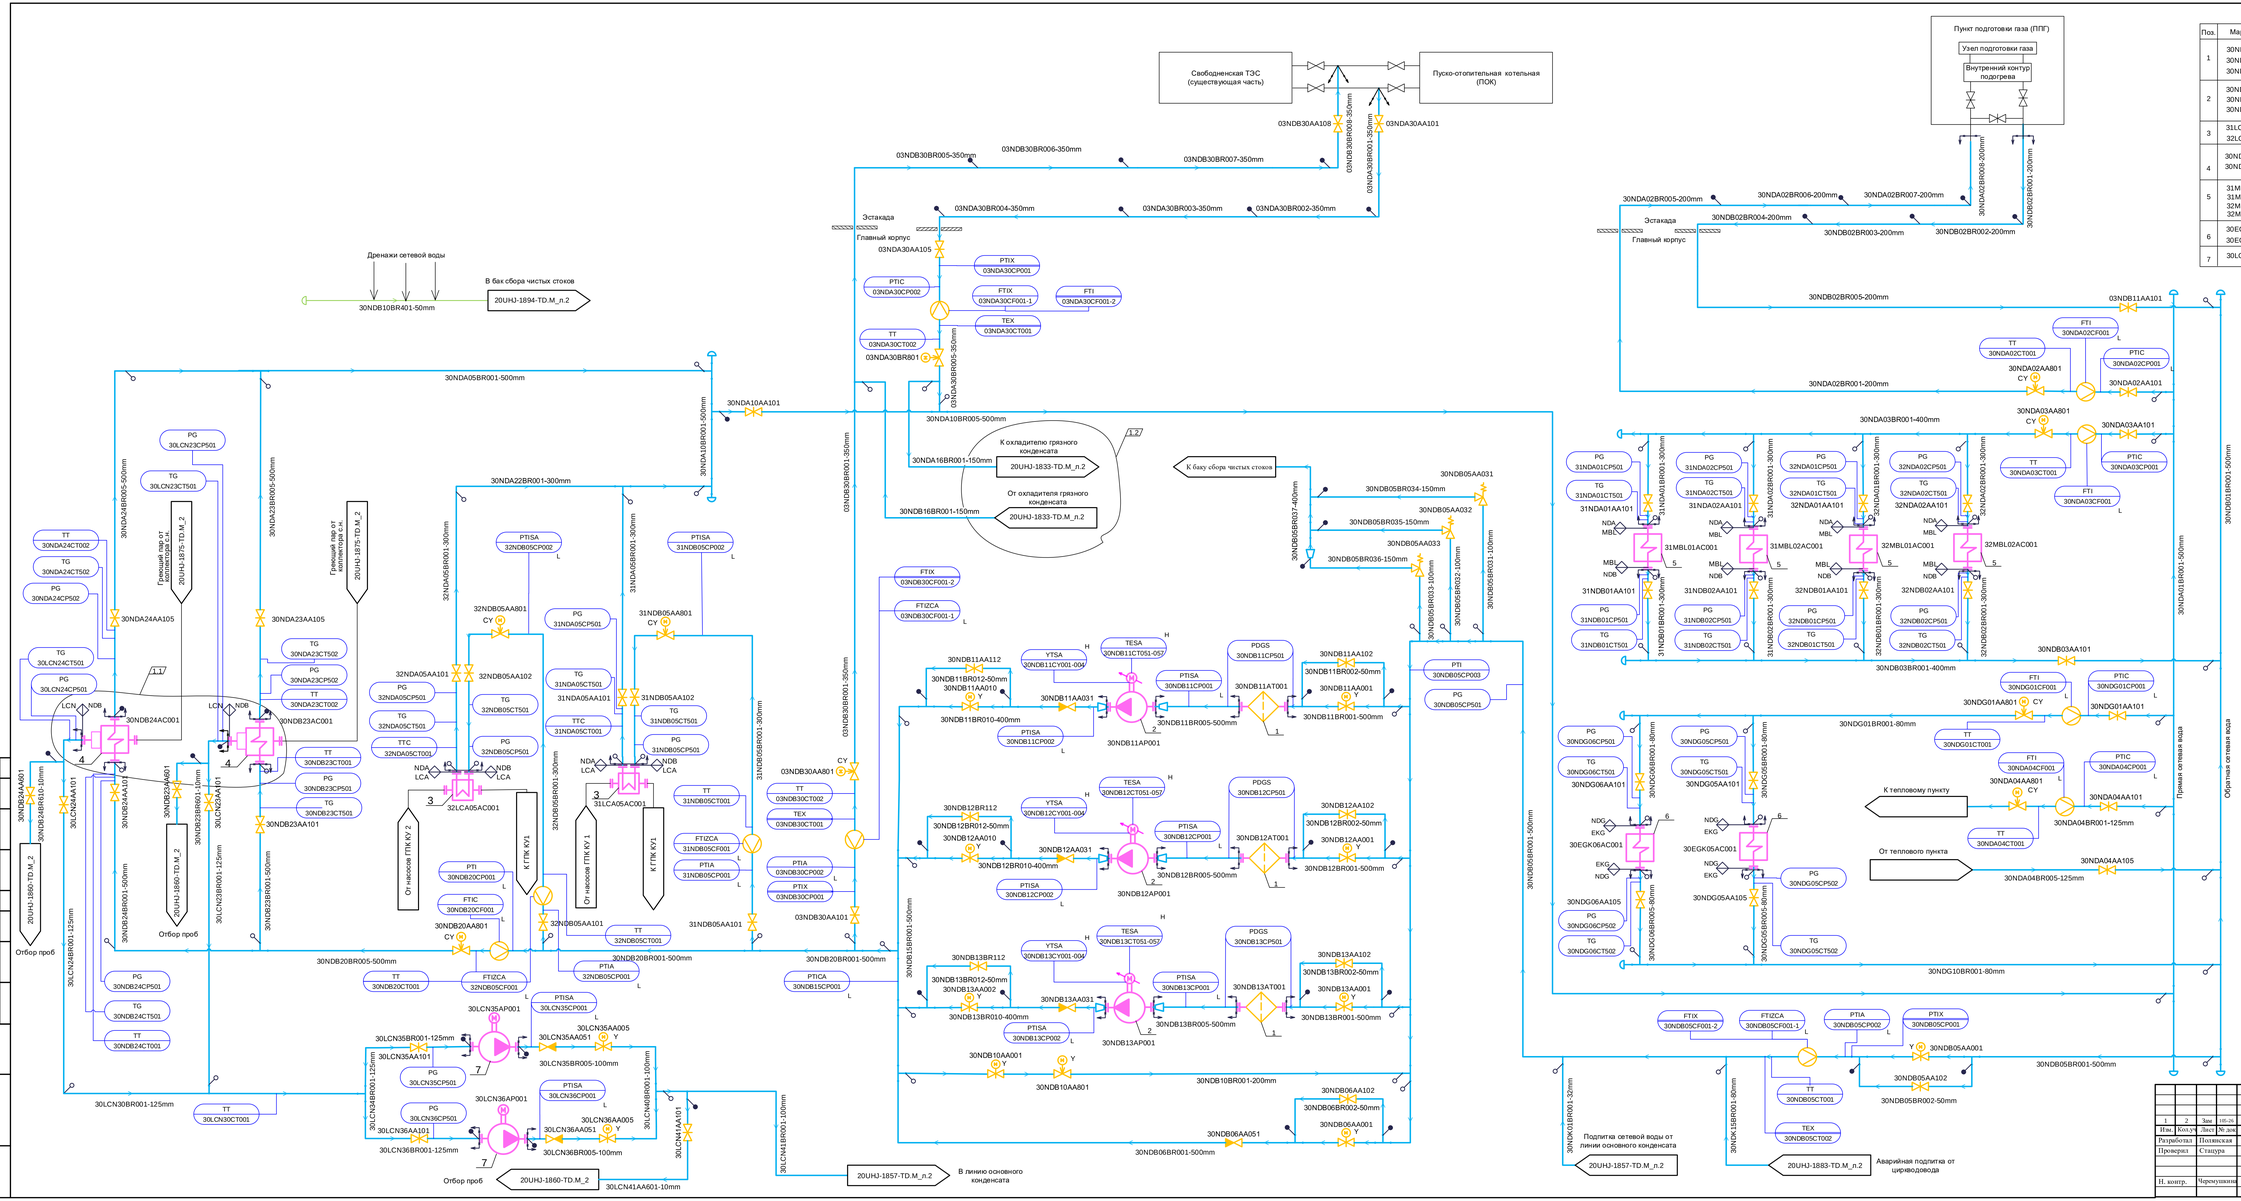

Перечень оборудования

Поз.	Маркировка	Наименование	Кол.	Характеристики	Примечание
1	30NDB11AT001 30NDB12AT001 30NDB13AT001	Фильтр (сетевые насосы)	3	G = 960 м^3/ч *	
2	30NDB11AP001 30NDB12AP001 30NDB13AP001	Сетевой насос	3	G = 960 м^3/ч * H = 120 м*	ВГМ-НЦДВ-813-390-250-4762-395 «ВОЛГА-ГИДРОМАШ»
3	31LCA05AC001 32LCA05AC001	Теплообменник ВВТО	2	Qt=11.2 Гкал/ч	
4	30NDB23AC001 30NDB24AC001	Подогреватель сетевой воды (ПСВ) со встроенным охладителем	2	Qt=27.3 Гкал/ч	
5	31MBL01AC001 31MBL02AC001 32MBL01AC001 32MBL02AC001	Теплообменник антиобледенительного контура	4	Qt=5.0 Гкал/ч	
6	30EGK05AC001 30EGK06AC001	Теплообменник горячего водоснабжения ГВС	2	Qt=8.0 Гкал/ч	
7	30LCN35AP001	Насос сливной	2	G = 81.0 м^3/ч H = 242 м	

Примечание:

1. Возможна корректировка PI-диаграммы после получения ИД от поставщиков оборудования

							141N50 – 20UHJ – 1900 – TD.M
1	2	Зам	105-16			02.26	Расширение Свободненской ТЭС. Этап 1. Строительство энергоблока ПГУ 450 МВт со вспомогательными зданиями и сооружениями.
Изм.	Кол.уч.	Лист	№ док.	Подп.		Дата	Рабочая документация.
Разработал		Поповская				02.26	Здание главного корпуса. PI-диаграмма трубопроводов сетевой воды
Проверил		Сидорук				02.26	Стадия: Р; Лист: 2; Листов:
Н. контр.		Черемушкина				02.26	PI-диаграмма трубопроводов сетевой воды. Система NDA, NDB, LCN

АКЦИОНЕРНОЕ ОБЩЕСТВО «ТЕХЭНЕРГОСЕРВИС» ВТИ

Формат А2х3

Согласовано

Взам. инв. №

Подпись и дата

Инв. № подл.