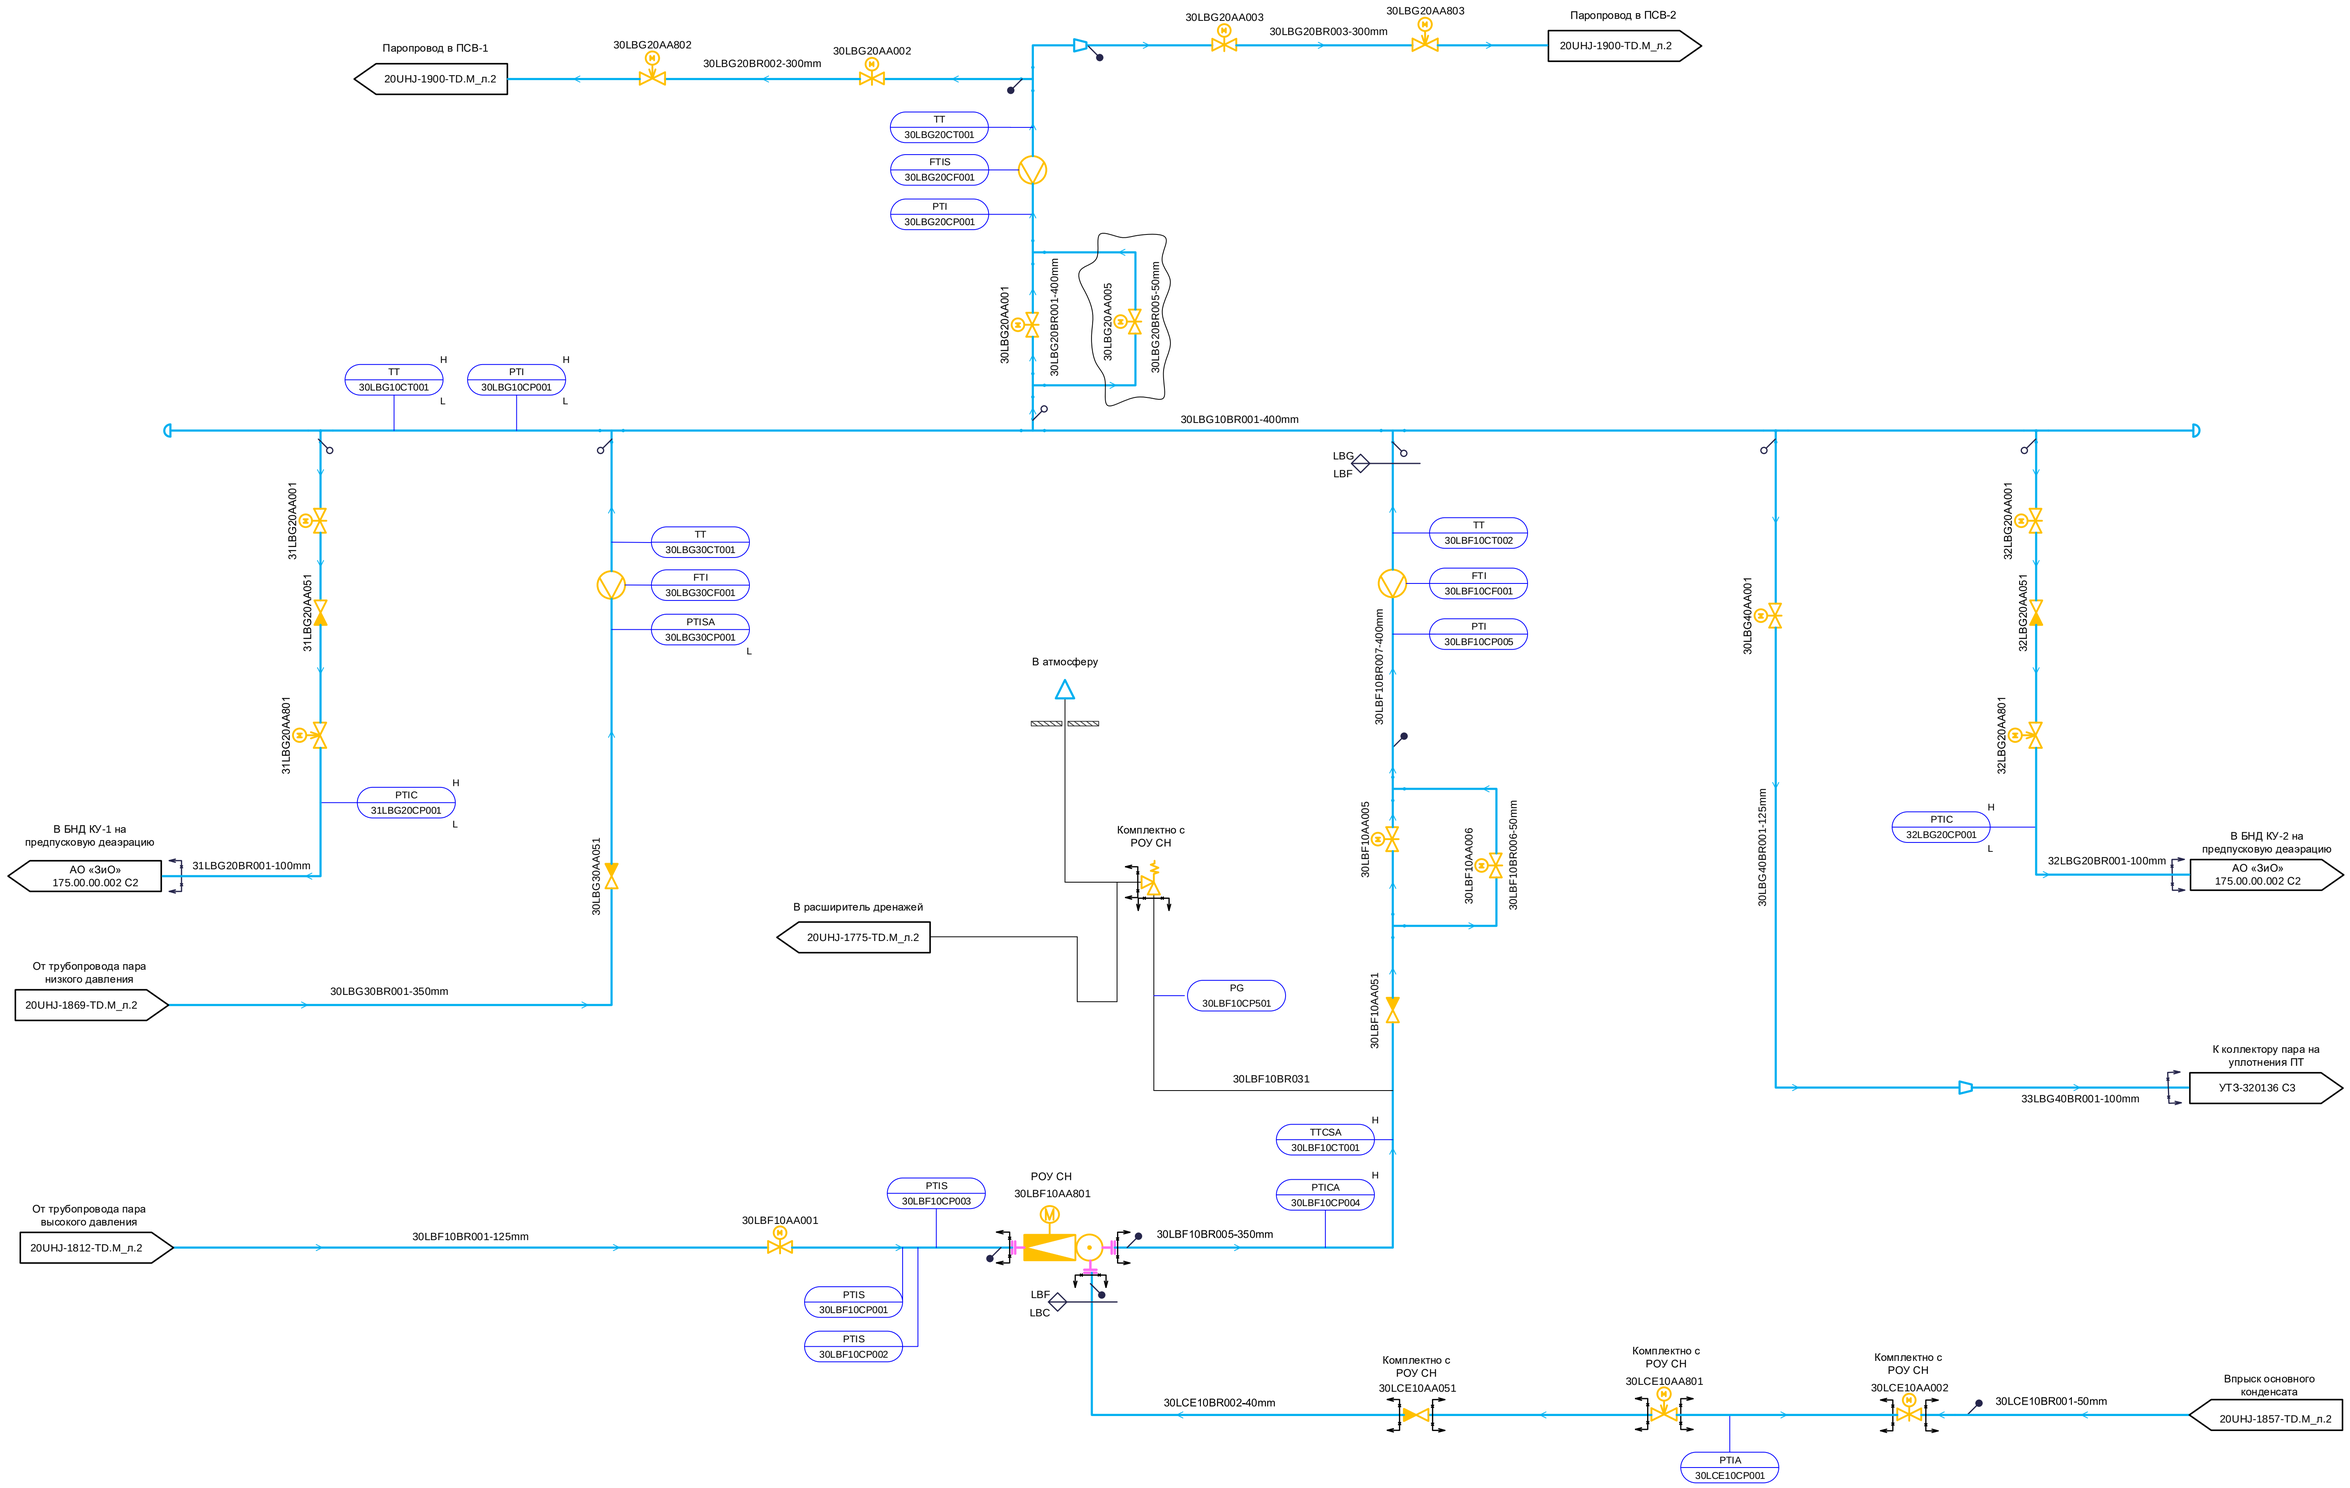

Примечания:
1. Возможна корректировка PI-диаграммы после получения исходных данных от поставщика оборудования;
2. Возможна корректировка PI-диаграммы после разработки компоновочных решений.

2	-	Зам.	744-26		02.26	141N50–20UHJ–1962–TD.M
1	-	Зам.	228-26		01.26	Расширение Свободненской ТЭС. Этап 1. Строительство энергоблока ПГУ 450 МВт со вспомогательными зданиями и сооружениями.
Изм.	Кол.уч	Лист	№ док.	Подп.	Дата	Рабочая документация.
Разработал		Гончар			02.26	Главный корпус. P&I-диаграмма трубопроводов РОУ СН
Проверил		Стацура			02.26	
Н. контр.		Черёмушкина			02.26	P&I-диаграмма трубопроводов РОУ СН. Система LBG.

Стадия	Лист	Листов
Р	2	

АКЦИОНЕРНОЕ ОБЩЕСТВО ИНСТИТУТ ТЕПЛОЭЛЕКТРОПРОЕКТ г. МОСКВА

Согласовано

Взам. инв. №

Подпись и дата

Инв. № подл.

Формат А1