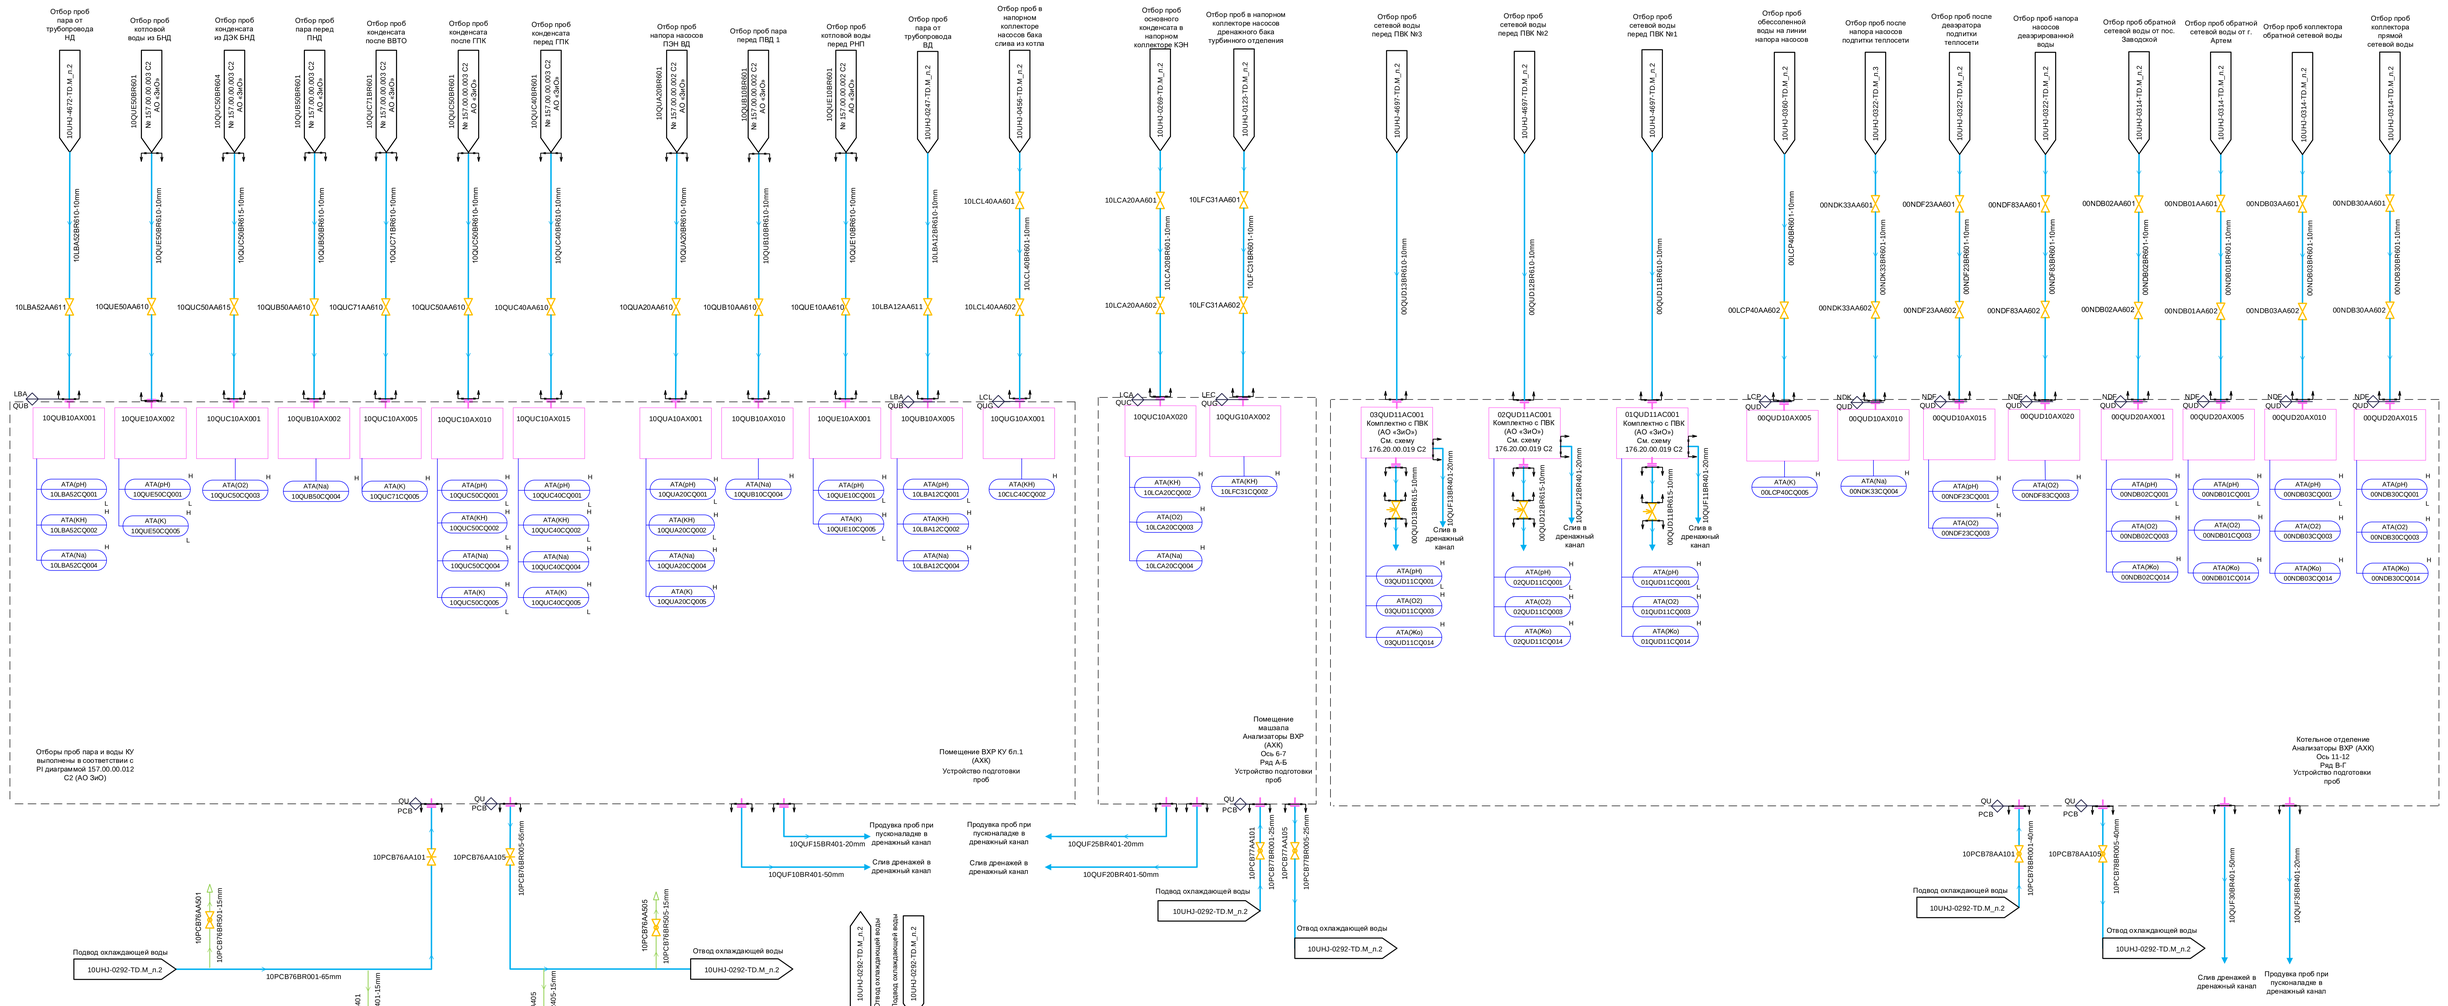

Изм.	Кол.уч.	Лист	№ док.	Подп.	Дата	144N70-10UHJ-0119-TD.M	
						Строительство Артемовской ТЭЦ-2 с внеплощадной инфраструктурой	
Разработал	Дроздов					Здание главного корпуса с баковым хозяйством. PI-диаграмма трубопроводов отбора пара и воды.	Стадия: Р; Лист: 2; Листов:
Проверил	Демина						
Н. контр.	Астраханцев					PI-диаграмма трубопроводов отбора пара и воды. Системы PCB,QUB, QUC, QUE, QUA, LBA, LCA, LFC, LCL, NDF, LCP, NDK, NDB	ГЕНЕРАЛЬНЫЙ ПРОЕКТИРОВЩИК ТЕХЭНЕРГОПРОМ ГРУППА ЕВРАЗ

Согласовано

Взам. инв. №

Подпись и дата

Инв. № подл.

Формат А2х3