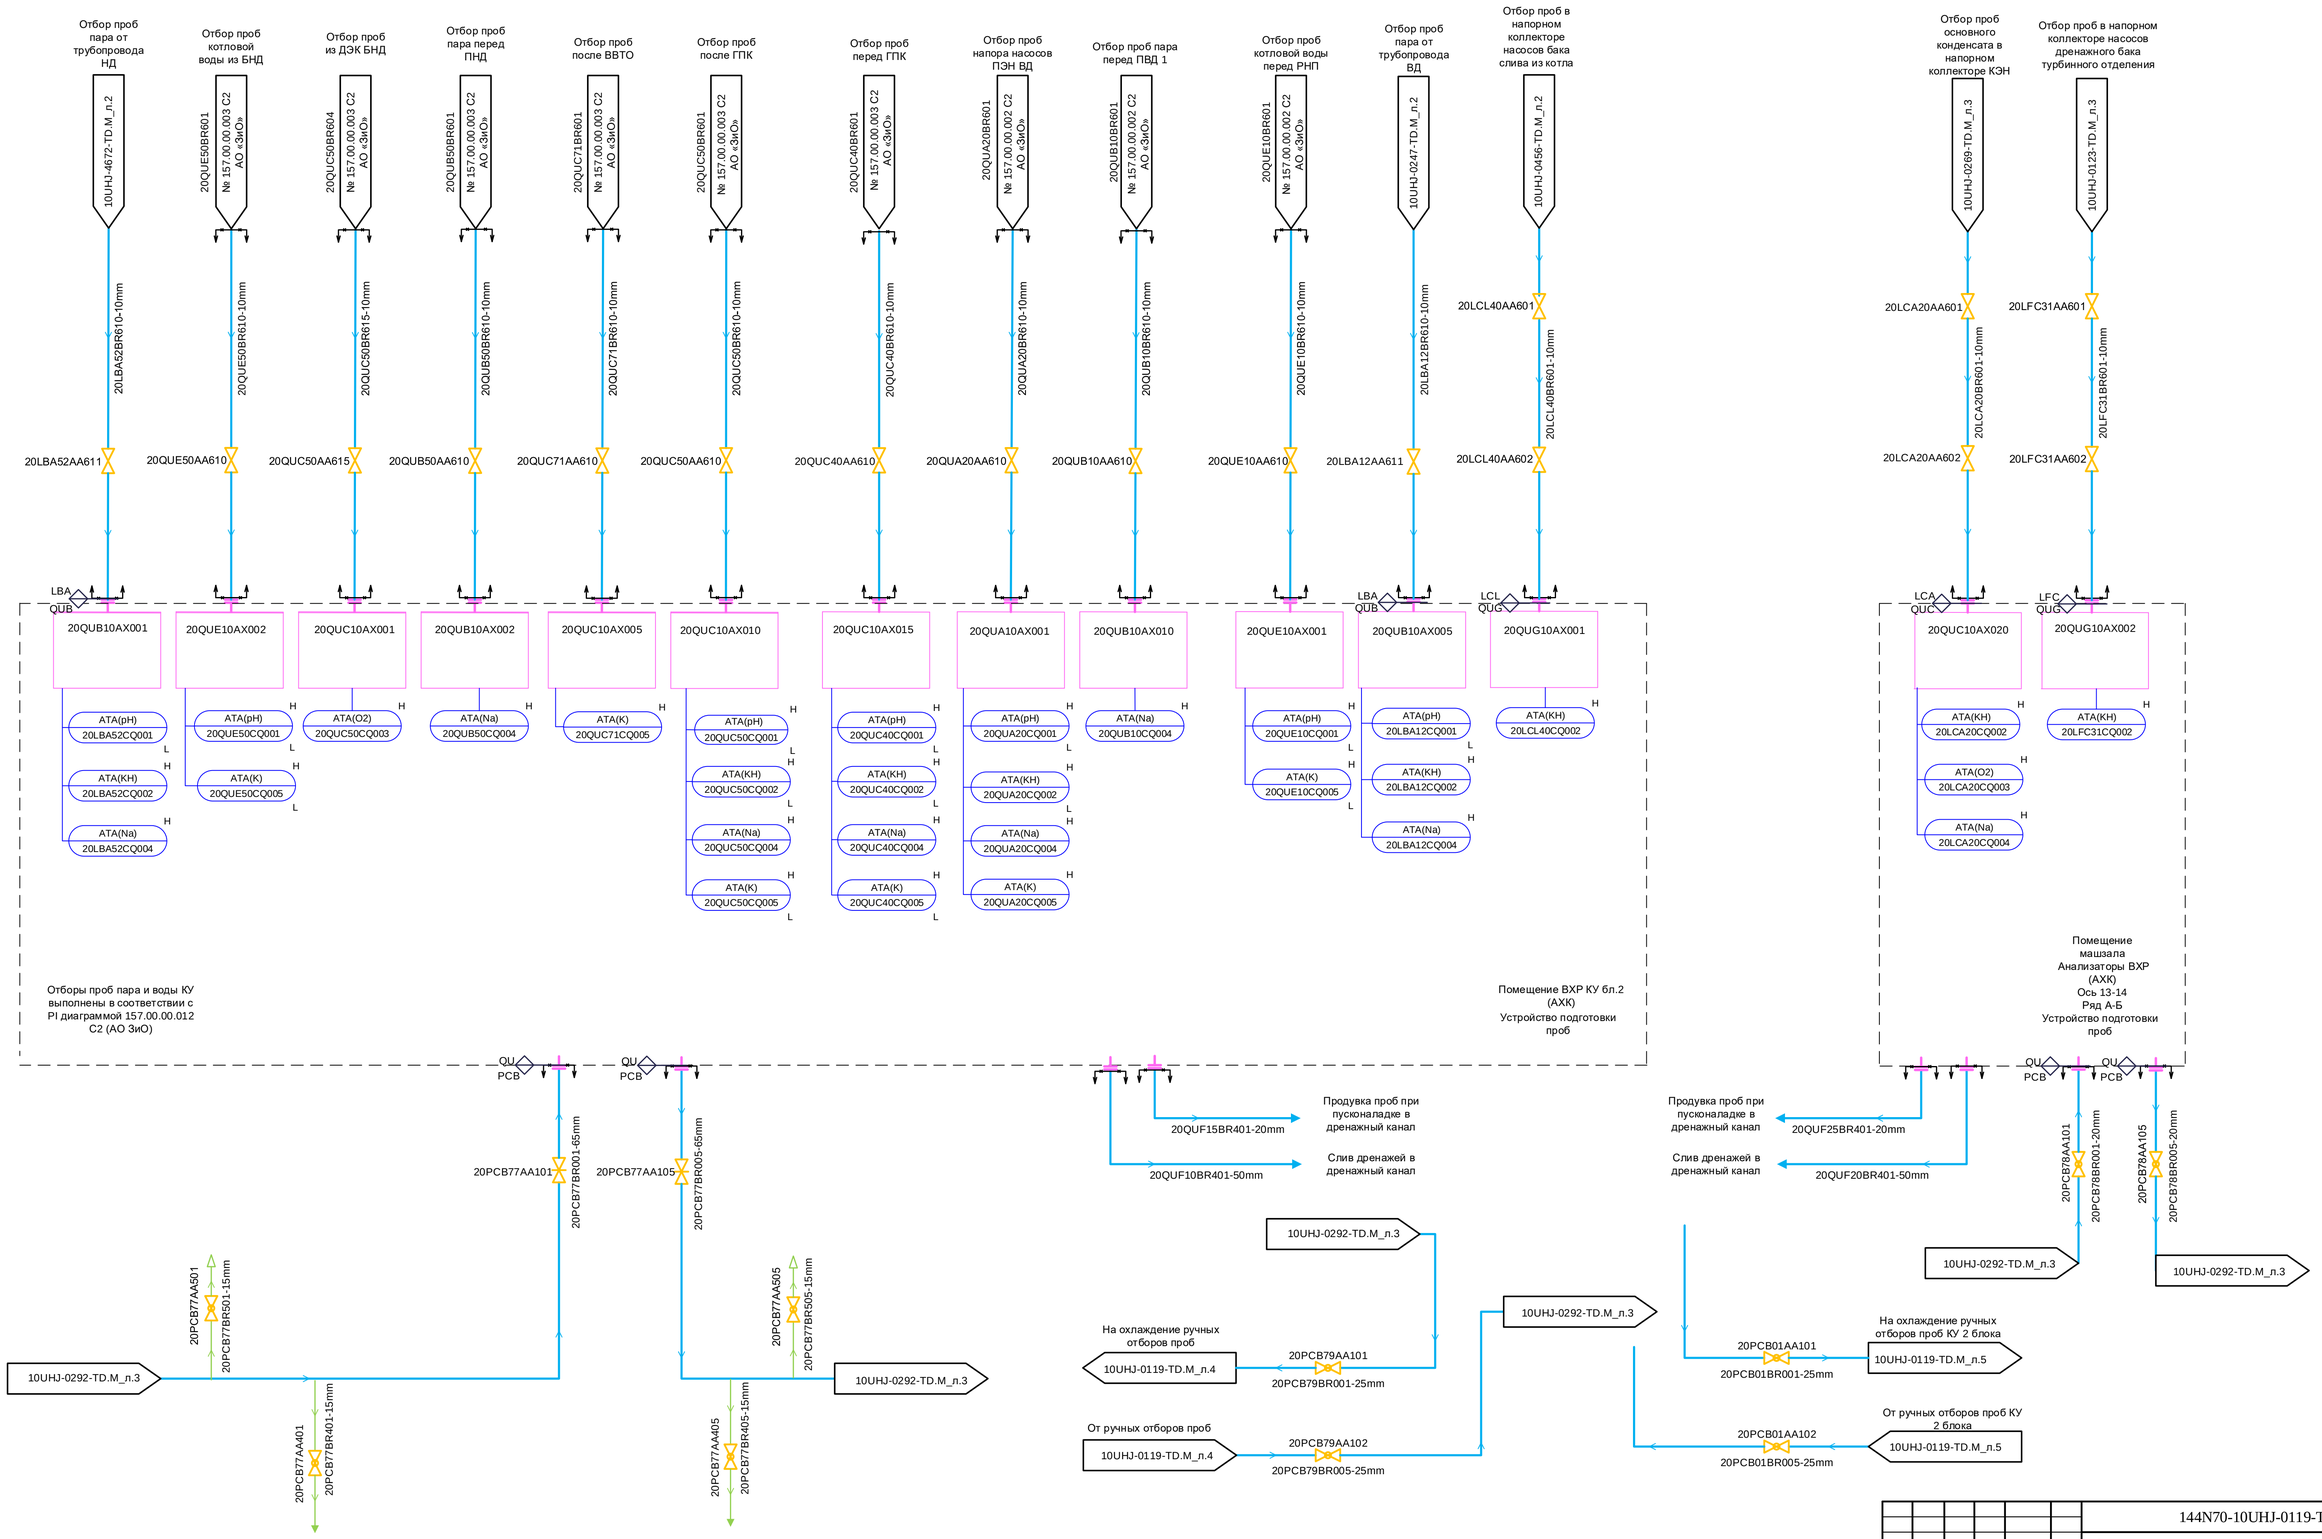


| Изм. | Кол.уч | Лист | № док. | Подп. | Дата |
|---|---|---|---|---|---|
| Разработал | | Дроздов | | | |
| Проверил | | Демина | | | |
| Н. контр. | | Астраханцев | | | |

144N70-10UHJ-0119-TD.M

Строительство Артемовской ТЭЦ-2 с внеплощадной инфраструктурой

Здание главного корпуса с баковым хозяйством. PI-диаграмма трубопроводов отбора пара и воды.

PI-диаграмма трубопроводов отбора пара и воды. Система PCB, QUB, QUC, QUE, QUA, LBA, LCA, LFC, LCL.

| Стадия | Лист | Листов |
|---|---|---|
| Р | 3 | |

АКЦИОНЕРНОЕ ОБЩЕСТВО ИНСТИТУТ ТЕПЛОЭЛЕКТРОПРОЕКТ г. МОСКВА

Согласовано

Взам. инв. №

Подпись и дата

Инв. № подл.

Формат А1