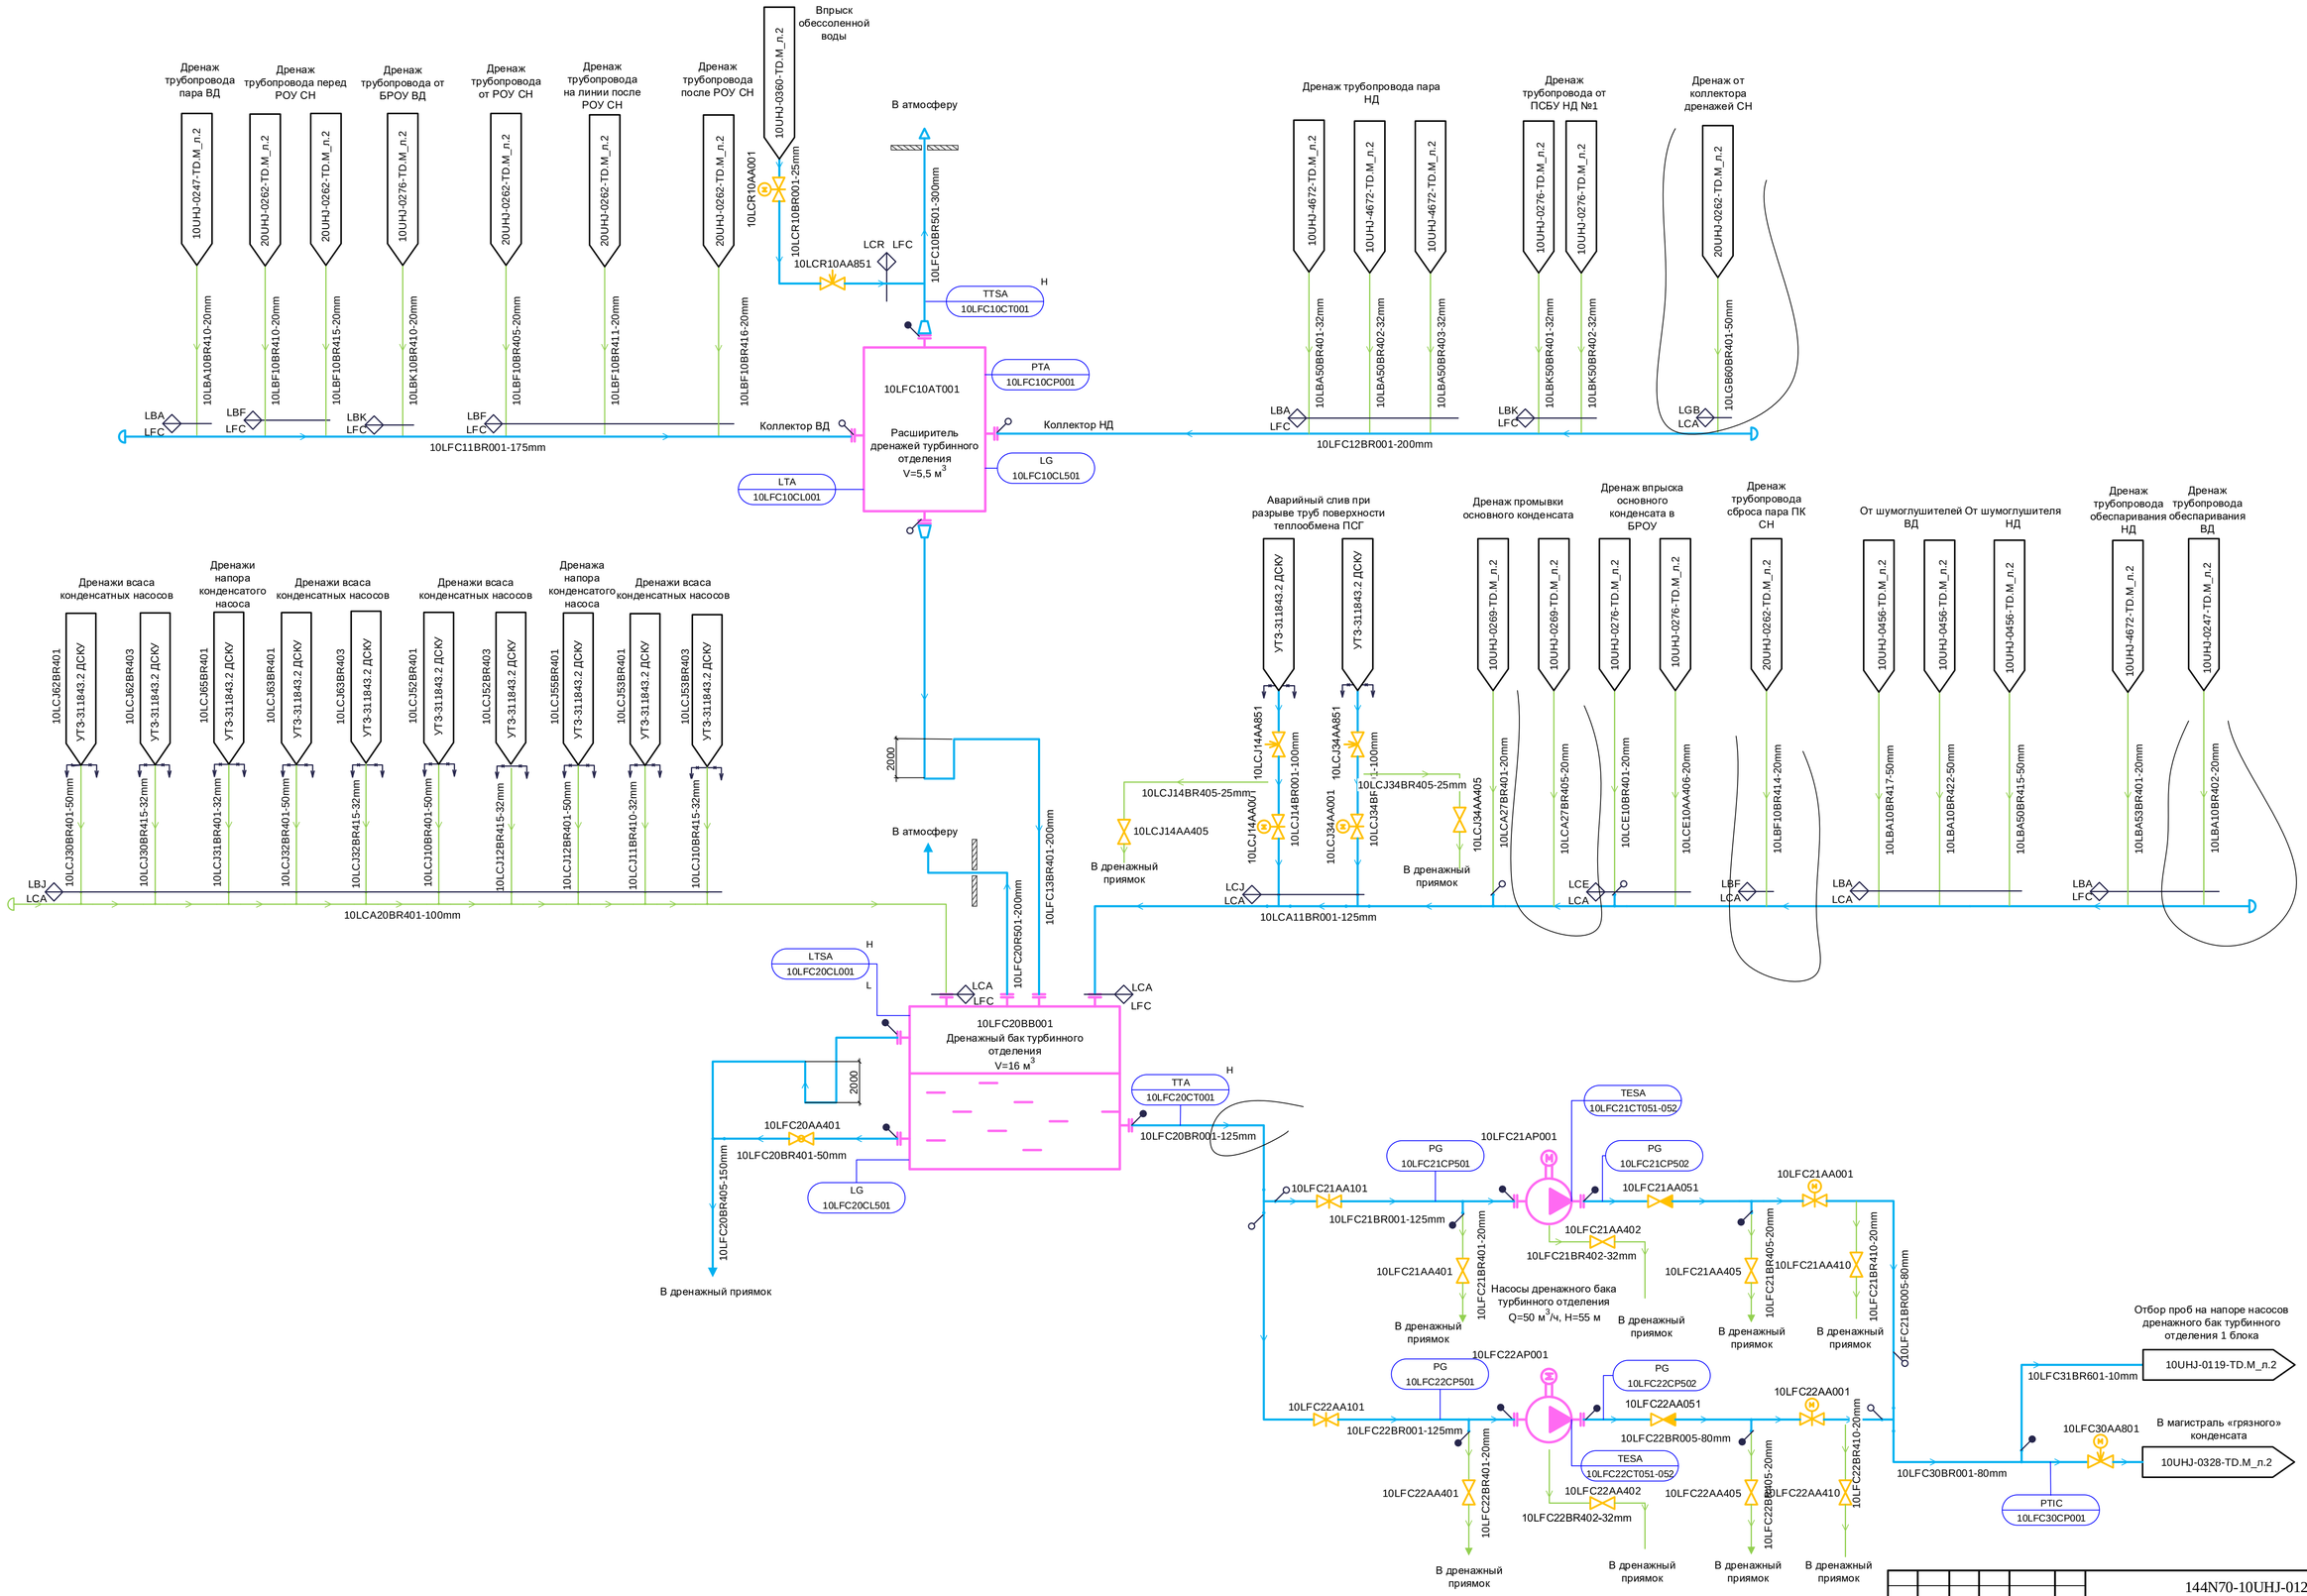


| | | | | | | |
|---|---|---|---|---|---|---|
| Изм. | Кол.уч | Лист | № док. | Подп. | Дата | 144N70-10UHJ-0123-TD.M |
| | | | | | | Строительство Артемовской ТЭЦ-2 с внеплощадной инфраструктурой |
| Разработал | | Дроздов | | | | Здание главного корпуса с баковым хозяйством. PI-диаграмма трубопроводов дренажей турбинного отделения. |
| Проверил | | Демина | | | | |
| Н. контр. | | Астраханцев | | | | PI-диаграмма трубопроводов дренажей турбинного отделения. Система LFC. |

| Стадия | Лист | Листов |
|---|---|---|
| Р | 2 | |

АКЦИОНЕРНОЕ ОБЩЕСТВО ИНСТИТУТ ТЕПЛОЭЛЕКТРОПРОЕКТ г. МОСКВА

Согласовано

Взам. инв. №

Подпись и дата

Инв. № подл.

Формат А1