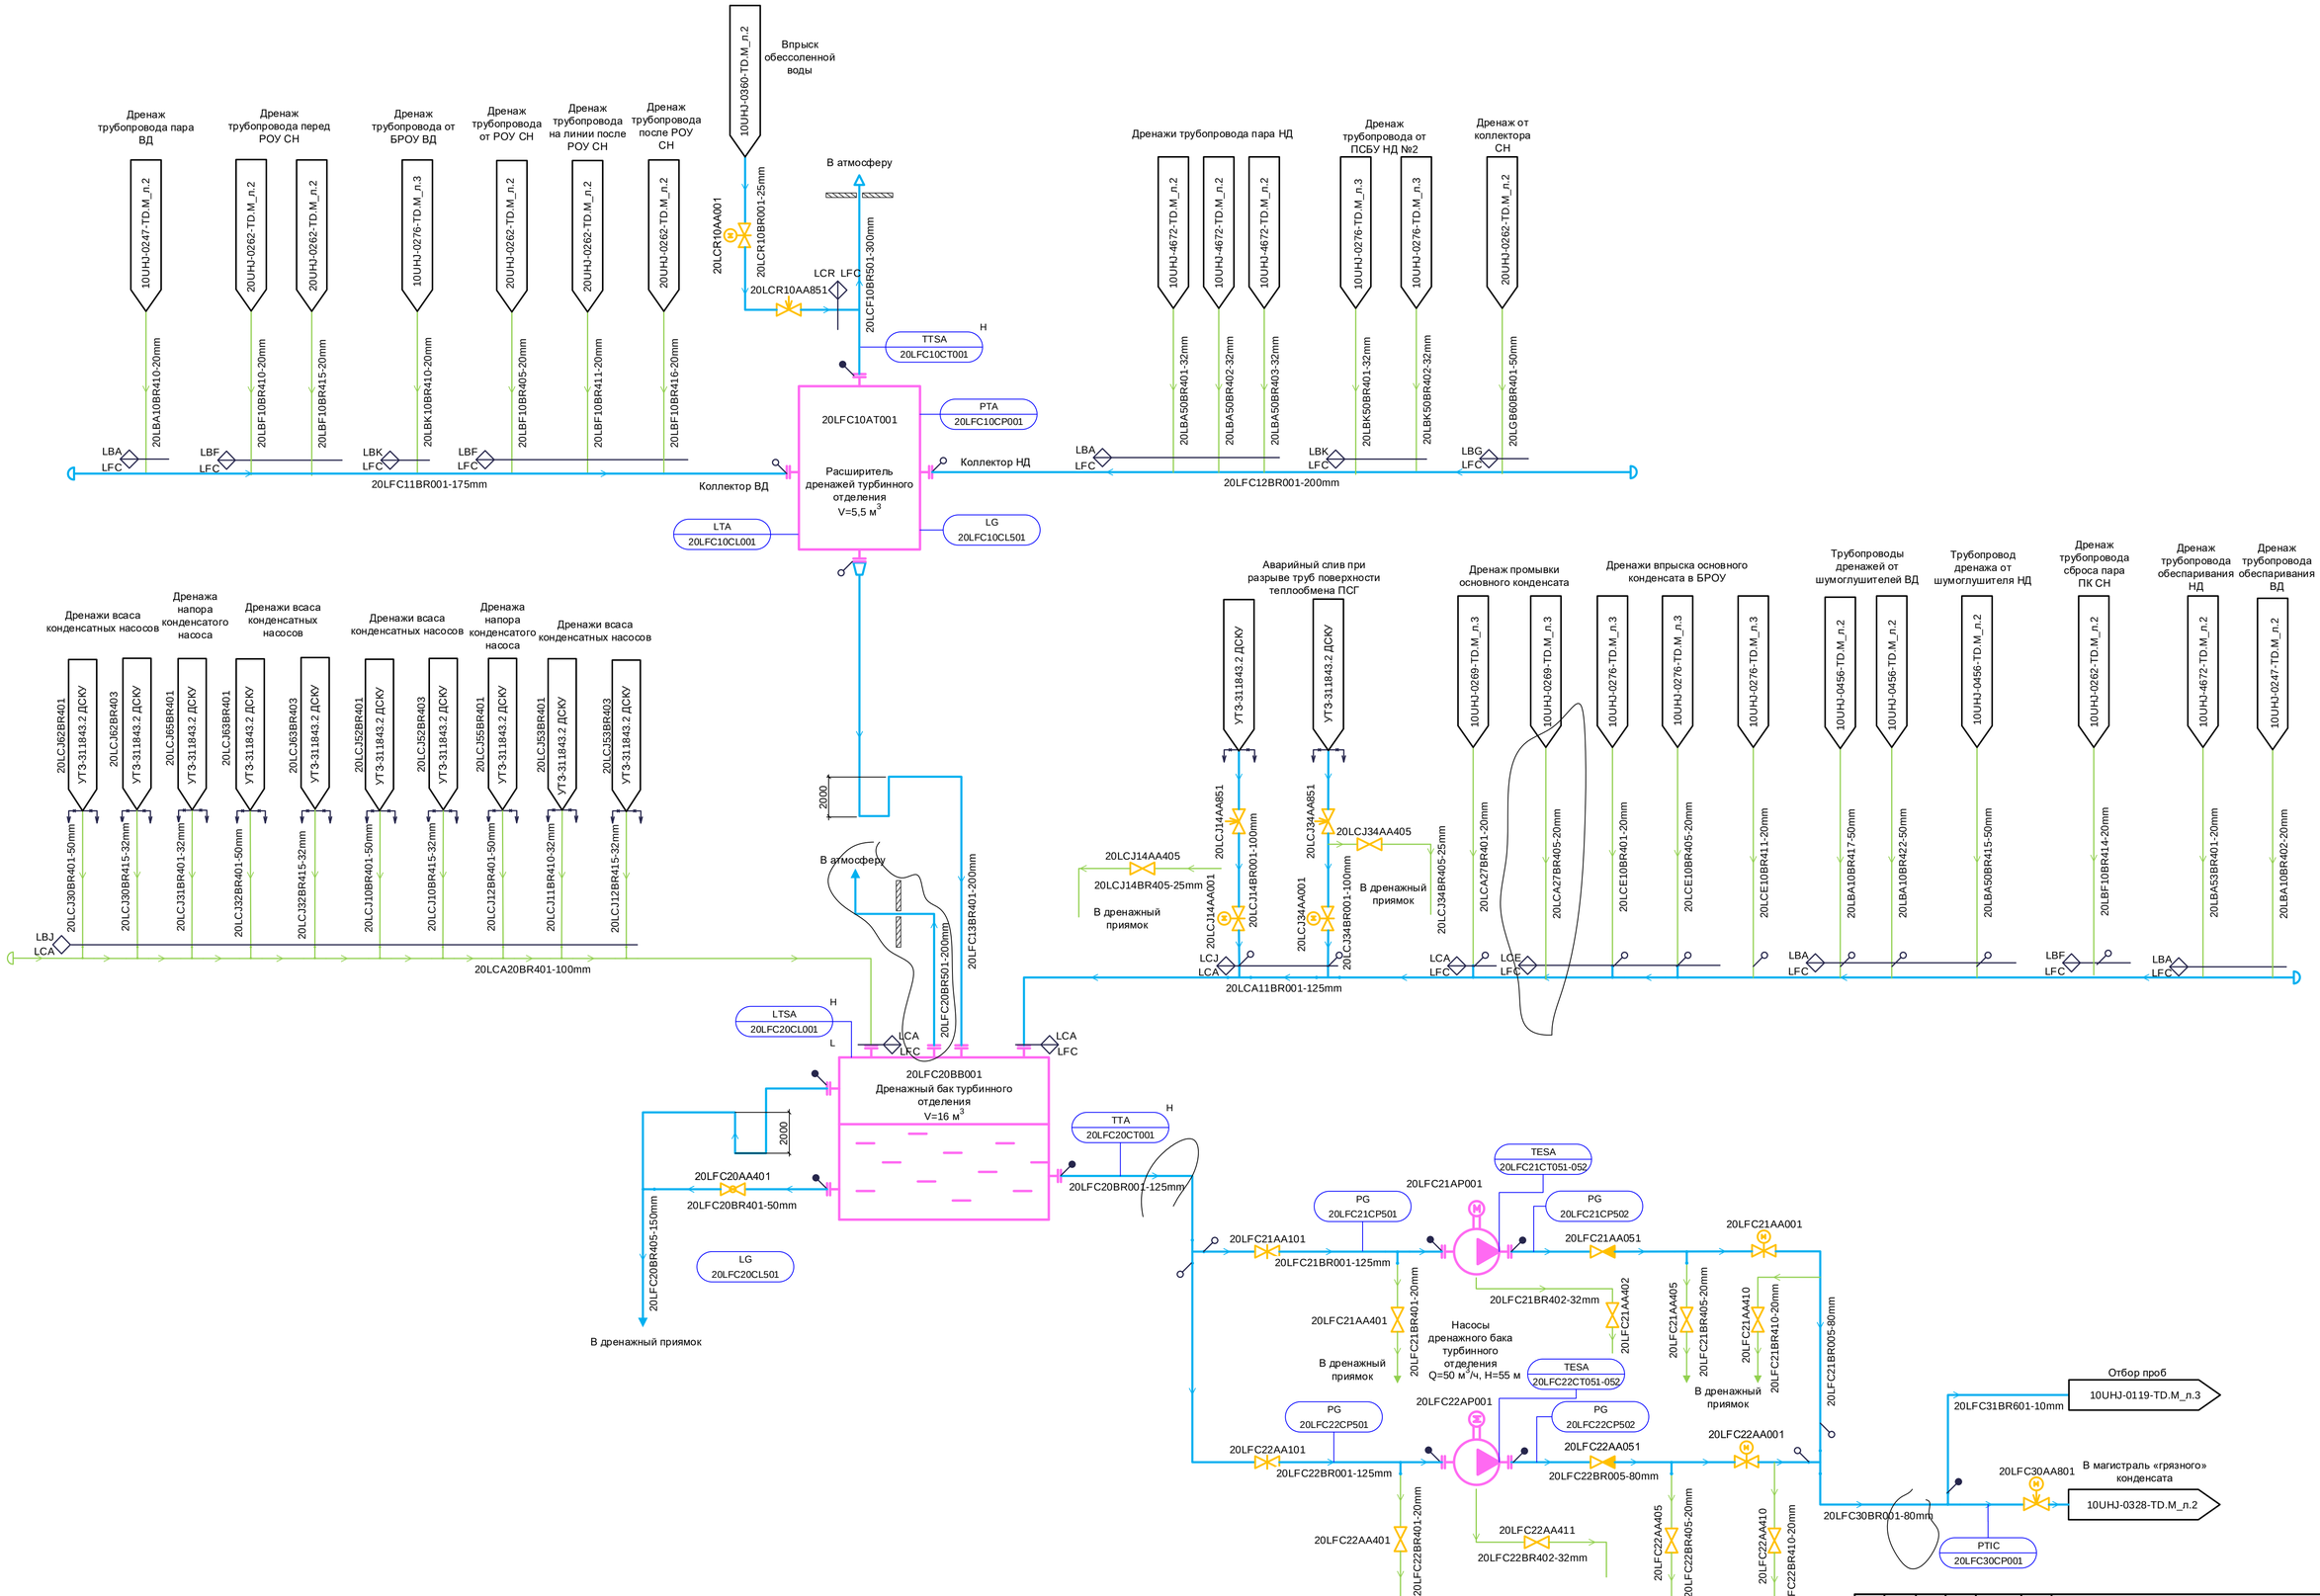

Изм.	Кол.уч	Лист	№ док.	Подп.	Дата	144N70-10UHJ-0123-TD
						Строительство Артемовской ТЭЦ-2 с внеплощадной инфраструктурой
Разработал		Дроздов				Здание главного корпуса с баковым хозяйством. PI-диаграмма трубопроводов дренажей турбинного отделения.
Проверил		Демина				Стадия: Р; Лист: 3; Листов:
Н. контр.		Астраханцев				PI-диаграмма трубопроводов дренажей турбинного отделения. Система LFC.

АКЦИОНЕРНОЕ ОБЩЕСТВО ИНСТИТУТ ТЕПЛОЭЛЕКТРОПРОЕКТ г. МОСКВА

Согласовано

Взам. инв. №

Подпись и дата

Инв. № подл.

Формат А1