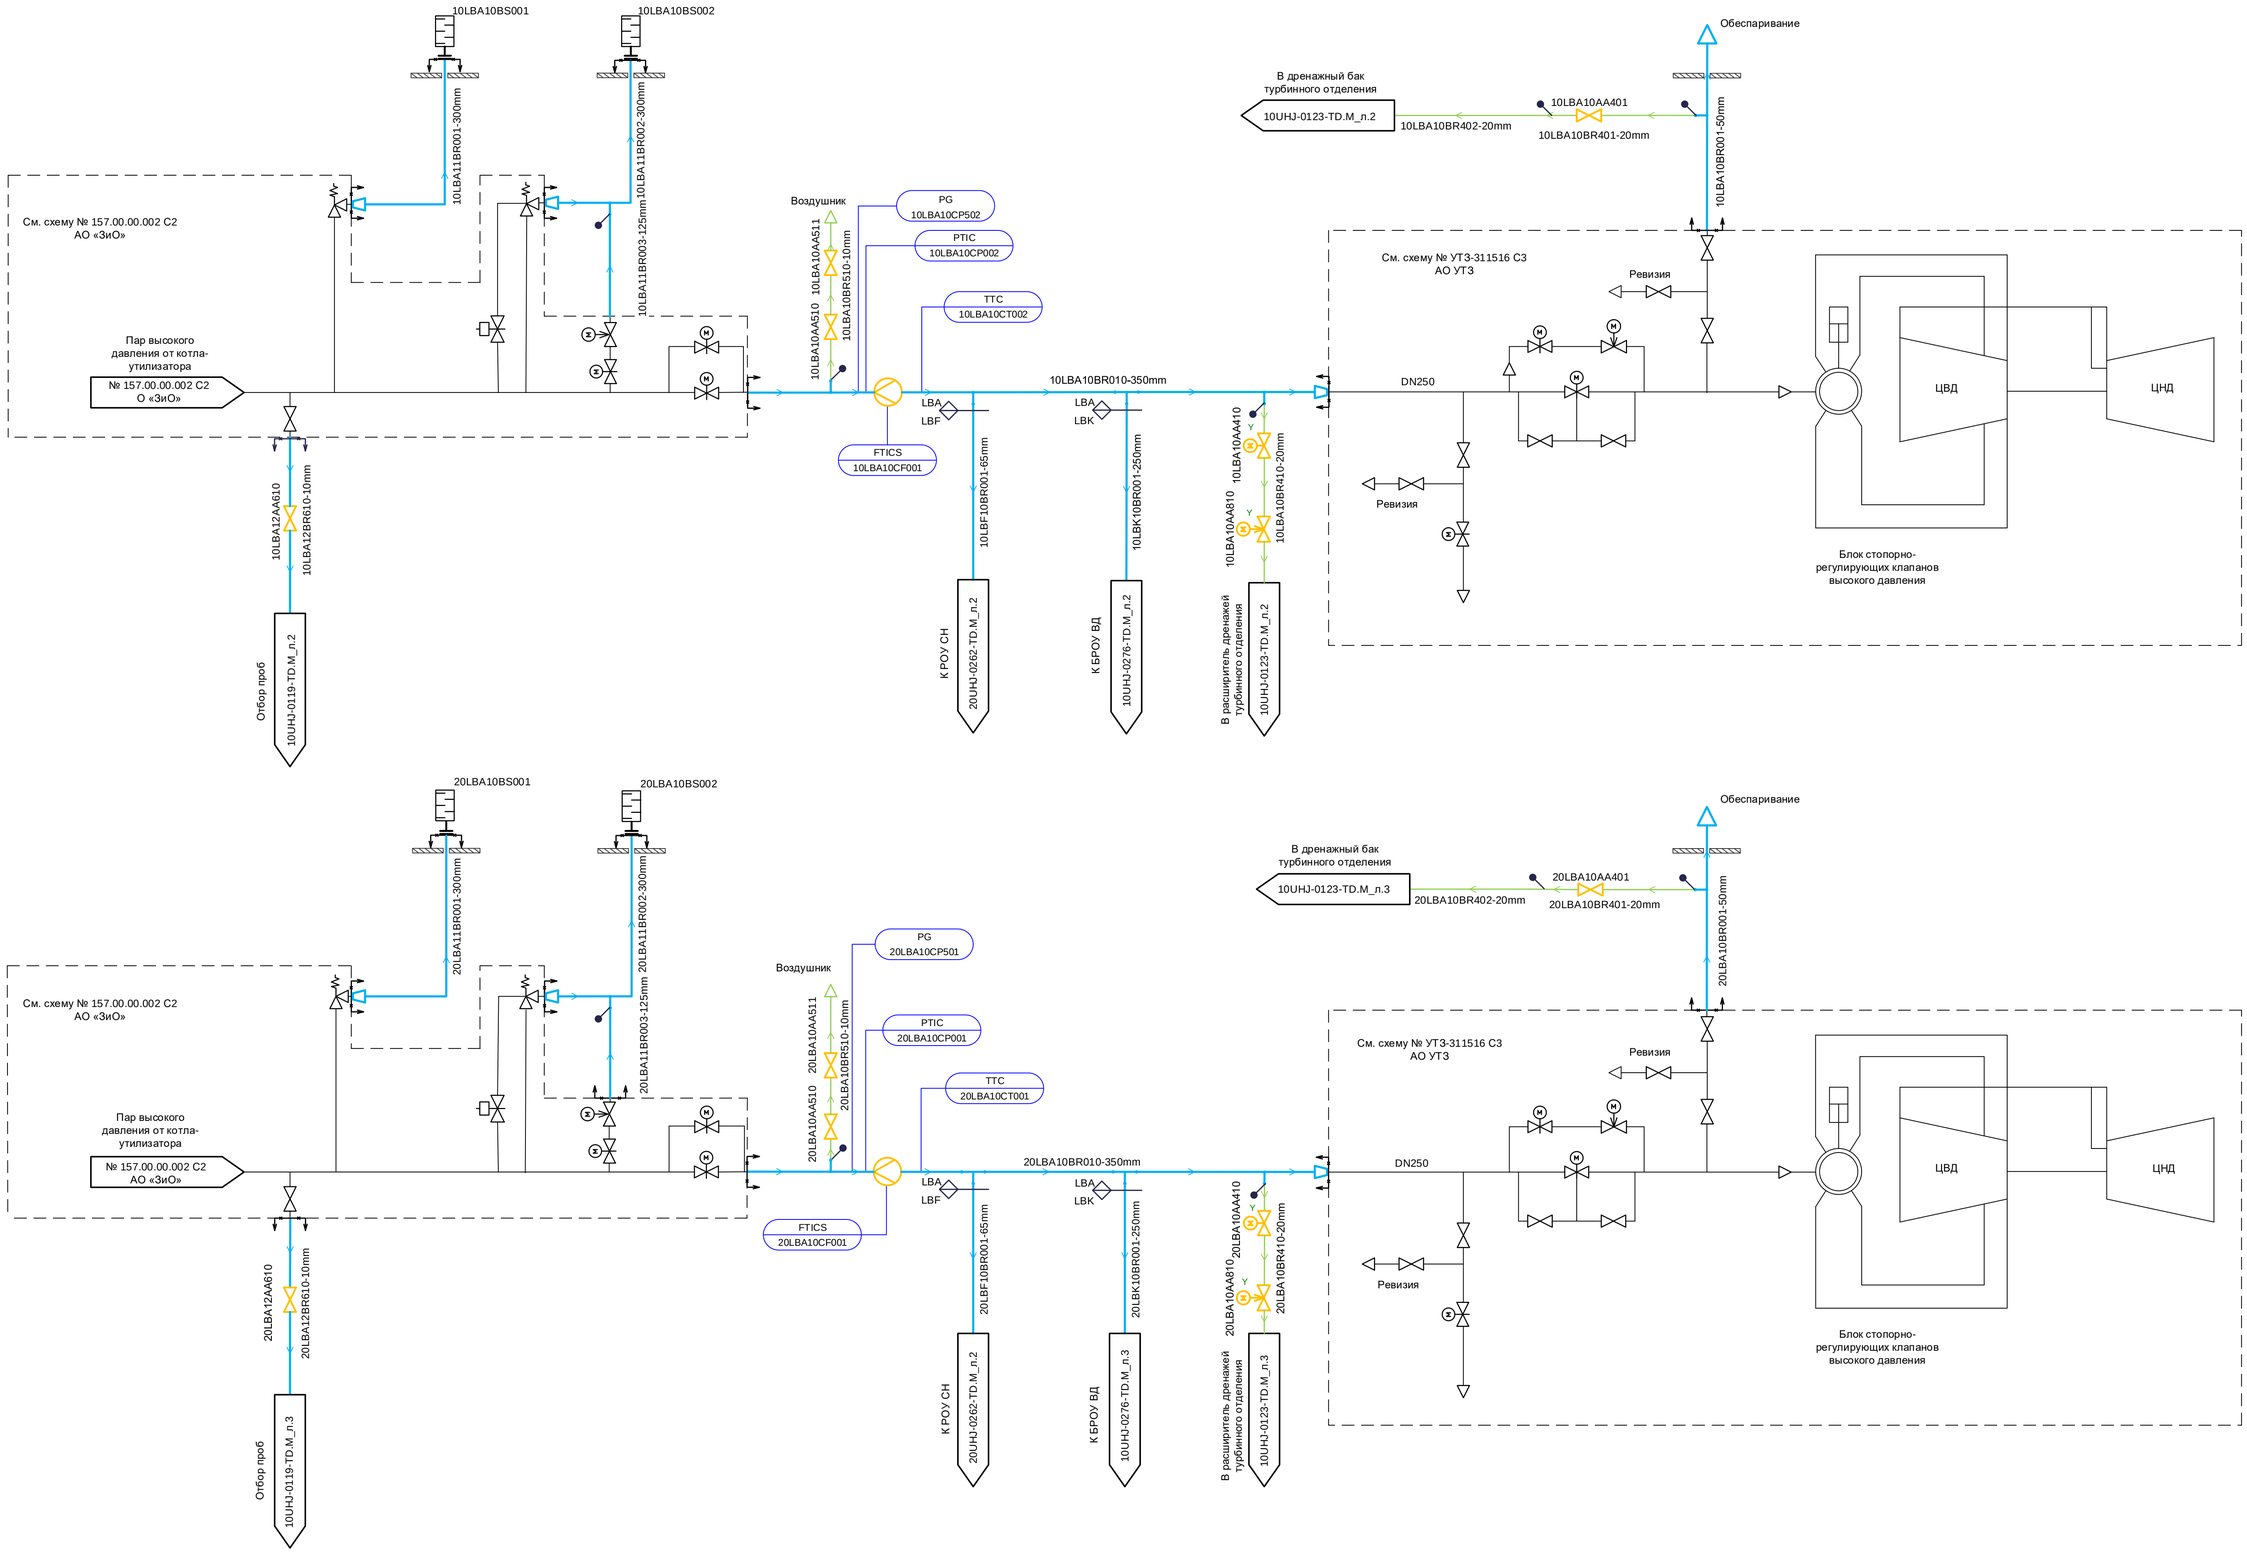

1	-	Зам.	5143-25		11.25	144N70-10UHJ-0247-TD.M
Изм.	Кол.уч	Лист	№ док.	Подп.	Дата	Артемовская ТЭЦ-2 с внеплощадочной инфраструктурой
Разработал		Дроздов				Здание главного корпуса с баковым хозяйством. PI-диаграмма трубопроводов пара высокого давления.
Проверил		Дёмина				Стадия: Р; Лист: 2; Листов:
Н. контр.		Черемушкина				PI-диаграмма трубопроводов пара высокого давления. Система LBA.

АКЦИОНЕРНОЕ ОБЩЕСТВО ИНСТИТУТ ТЕПЛОЭЛЕКТРОПРОЕКТ г. МОСКВА

Согласовано

ОАСУ

Взам. инв. №

Подпись и дата

Инв. № подл.

Формат А1