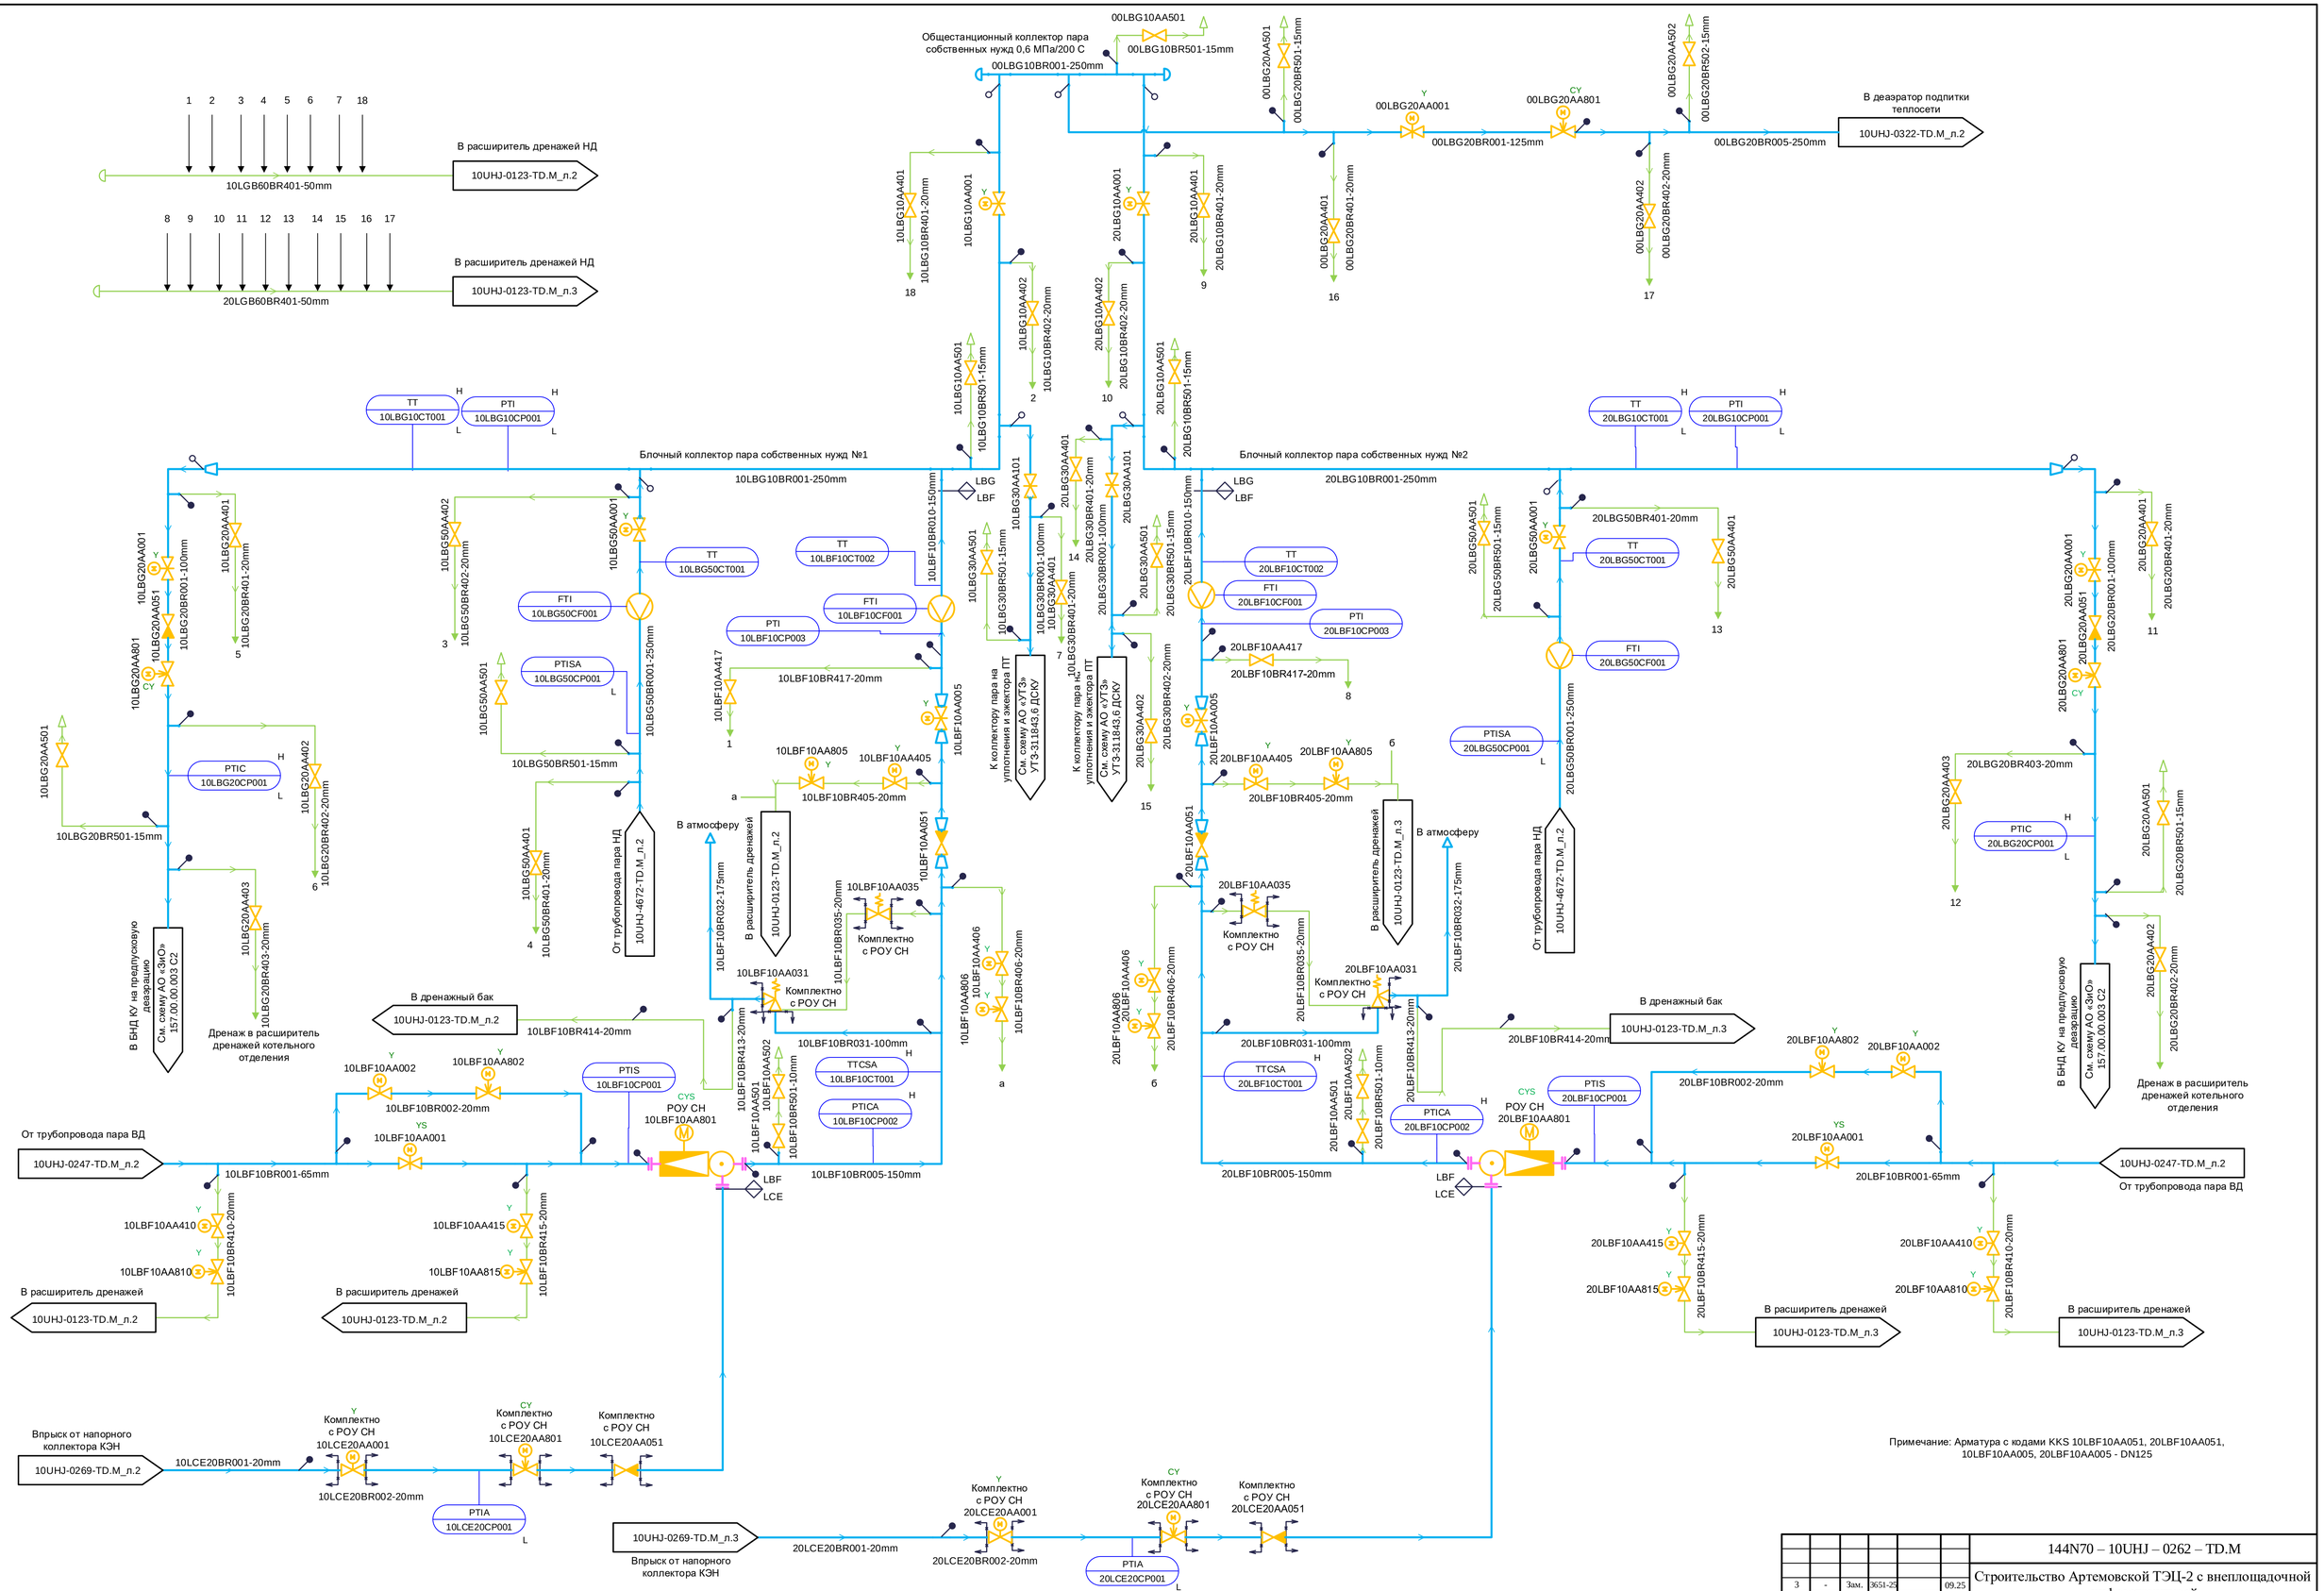


Примечание: Арматура с кодами KKS 10LBF10AA051, 20LBF10AA051, 10LBF10AA005, 20LBF10AA005 - DN125

| | | | | | | |
|---|---|---|---|---|---|---|
| 3 | - | Зам. | 3651-25 | | 09.25 | 144N70 – 10UHJ – 0262 – TD.M |
| Изм. | Кол.уч | Лист | № док. | Подп. | Дата | Строительство Артемовской ТЭЦ-2 с внеплощадочной инфраструктурой |
| Разработал | | Дёмина | | | | Здание главного корпуса с баковым хозяйством. P&I-диаграмма трубопроводов пара собственных нужд |
| Проверил | | Смирнова | | | | Стадия: Р; Лист: 2; Листов: |
| Н. контр. | | Черемушкина | | | | PI-диаграмма трубопроводов пара собственных нужд. Система LBG |

АКЦИОНЕРНОЕ ОБЩЕСТВО ИНСТИТУТ ТЕПЛОЭЛЕКТРОПРОЕКТ г. МОСКВА

Согласовано

ОАСУ

Взам. инв. №

Подпись и дата

Инв. № подл.

Формат А1