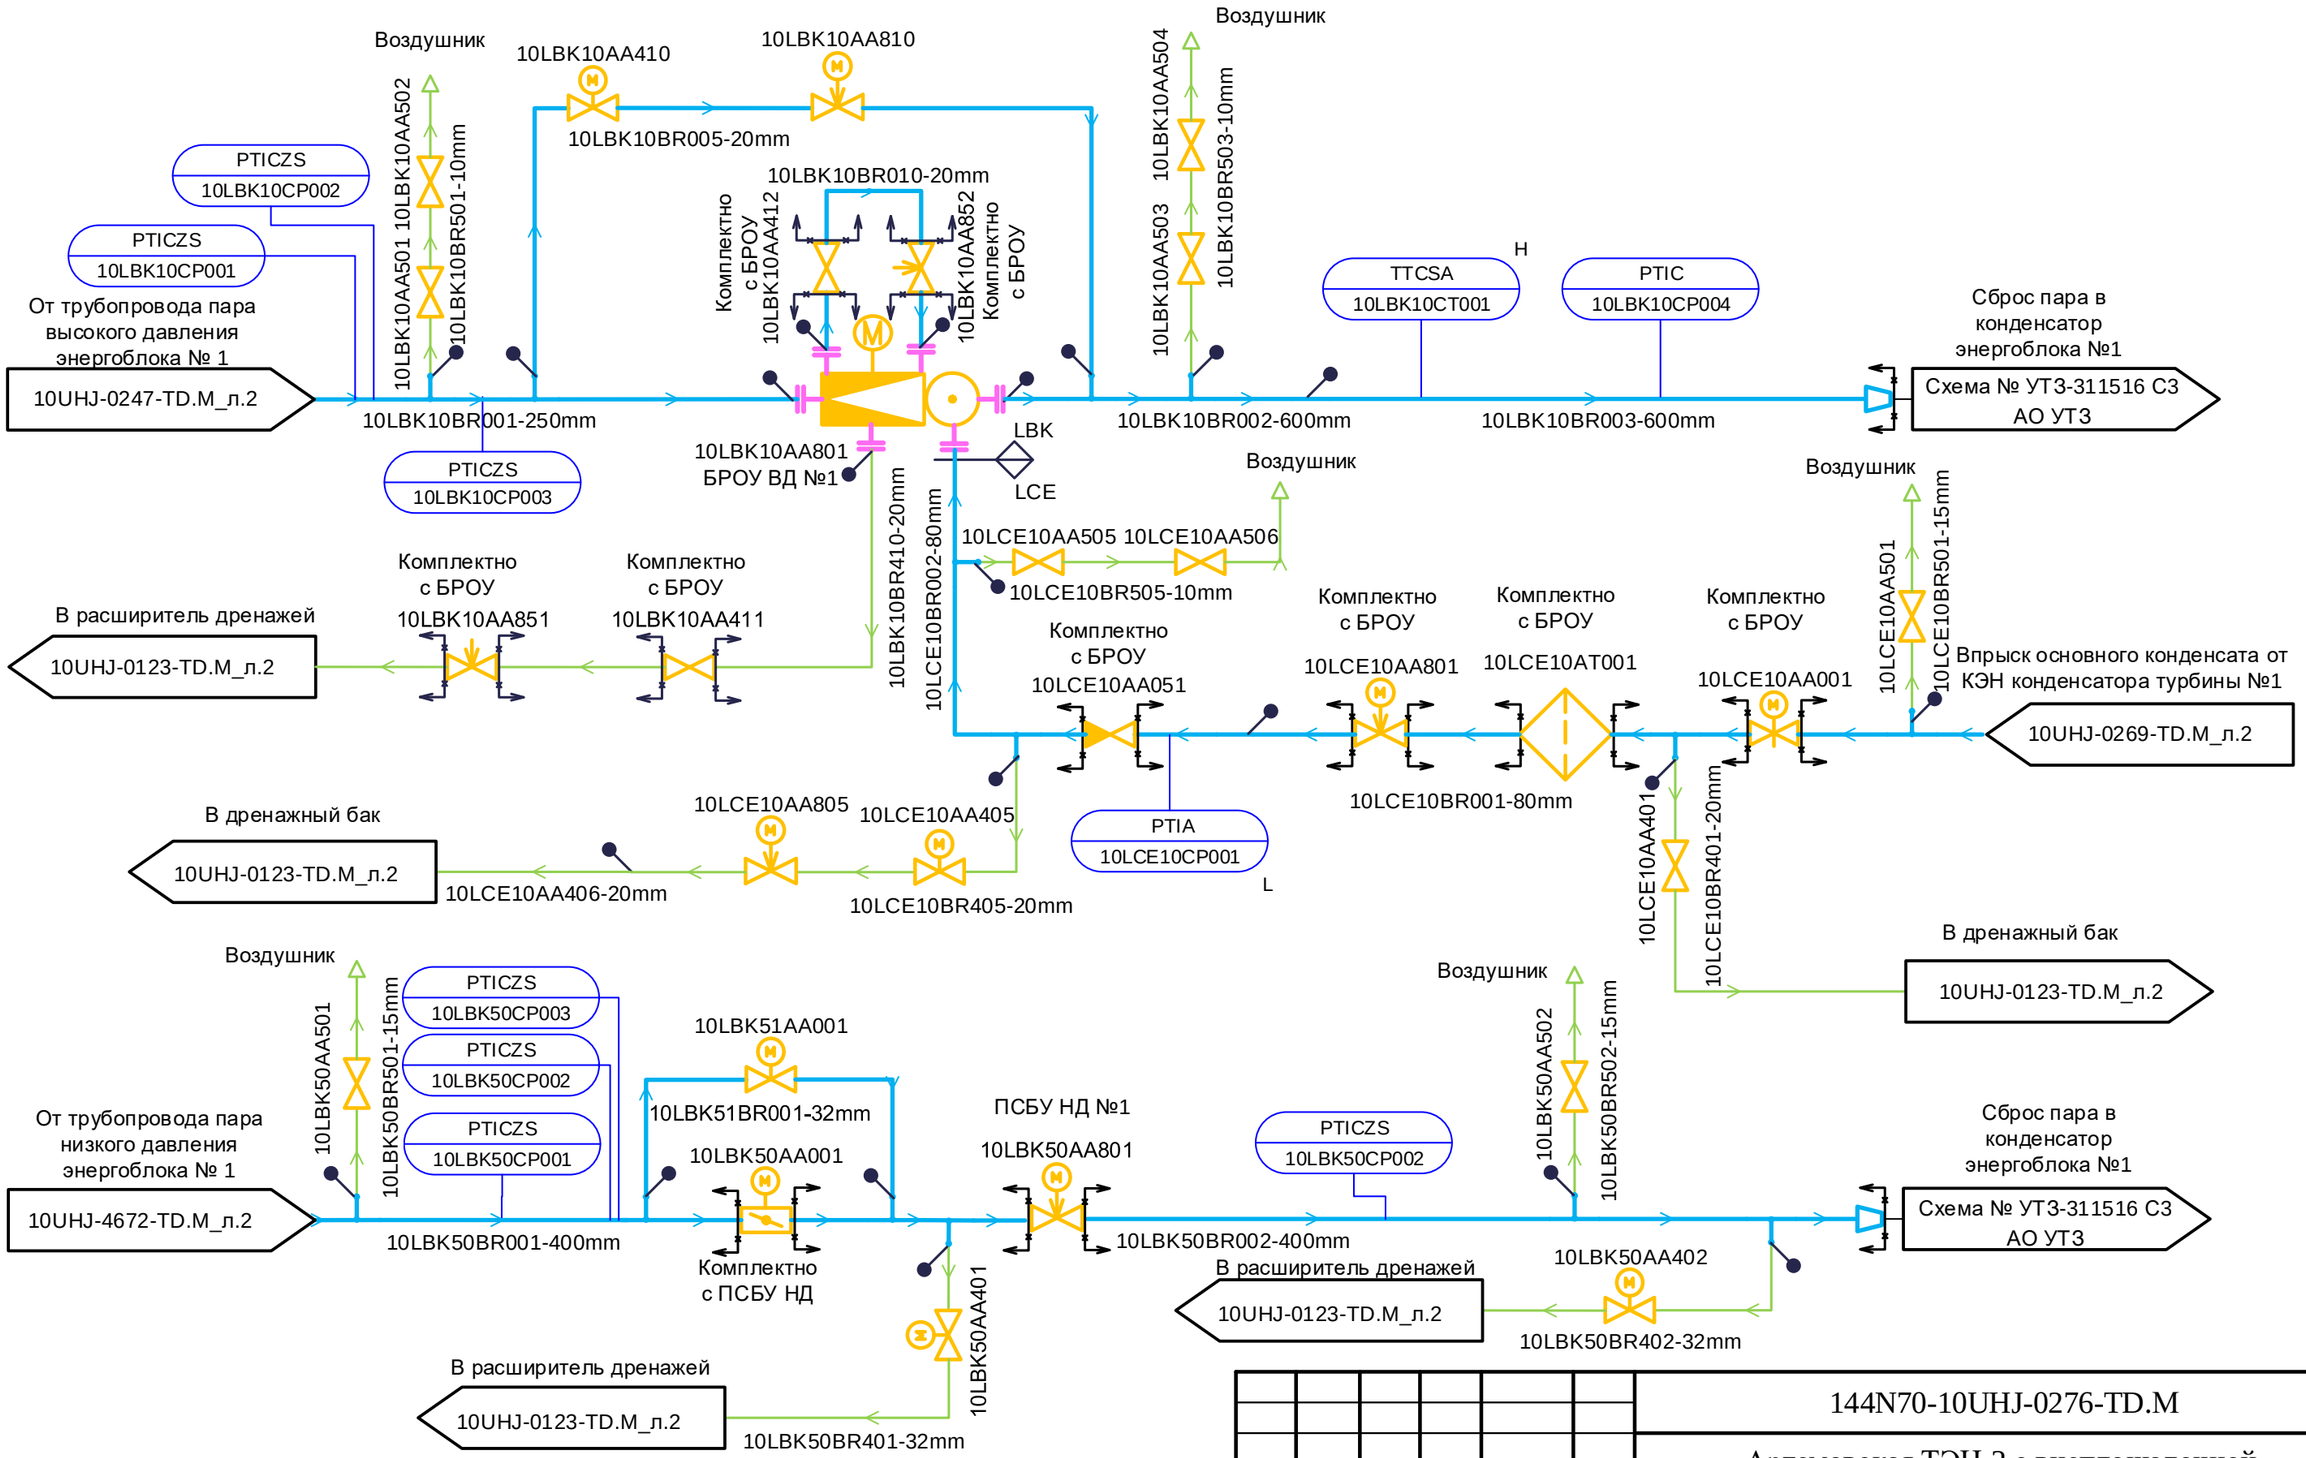


| | | | | | | |
|---|---|---|---|---|---|---|
| 1 | - | Зам. | 5143-25 | | 11.25 | 144N70-10UHJ-0276-TD.M |
| Изм. | Кол.уч | Лист | № док. | Подп. | Дата | Артемовская ТЭЦ-2 с внеплощадочной инфраструктурой |
| Разработал | | Дроздов | | | | Здание главного корпуса с баковым хозяйством. PI-диаграмма трубопроводов БРОУ. |
| Проверил | | Демина | | | | Стадия: Р; Лист: 2; Листов: |
| Н. контр. | | Черемушкина | | | | PI-диаграмма трубопроводов БРОУ. Система LBK, LCE |

АКЦИОНЕРНОЕ ОБЩЕСТВО ИНСТИТУТ ТЕПЛОЭЛЕКТРОПРОЕКТ г. МОСКВА

Согласовано

ОАСУ

Взам. инв. №

Подпись и дата

Инв. № подл.

Формат А3