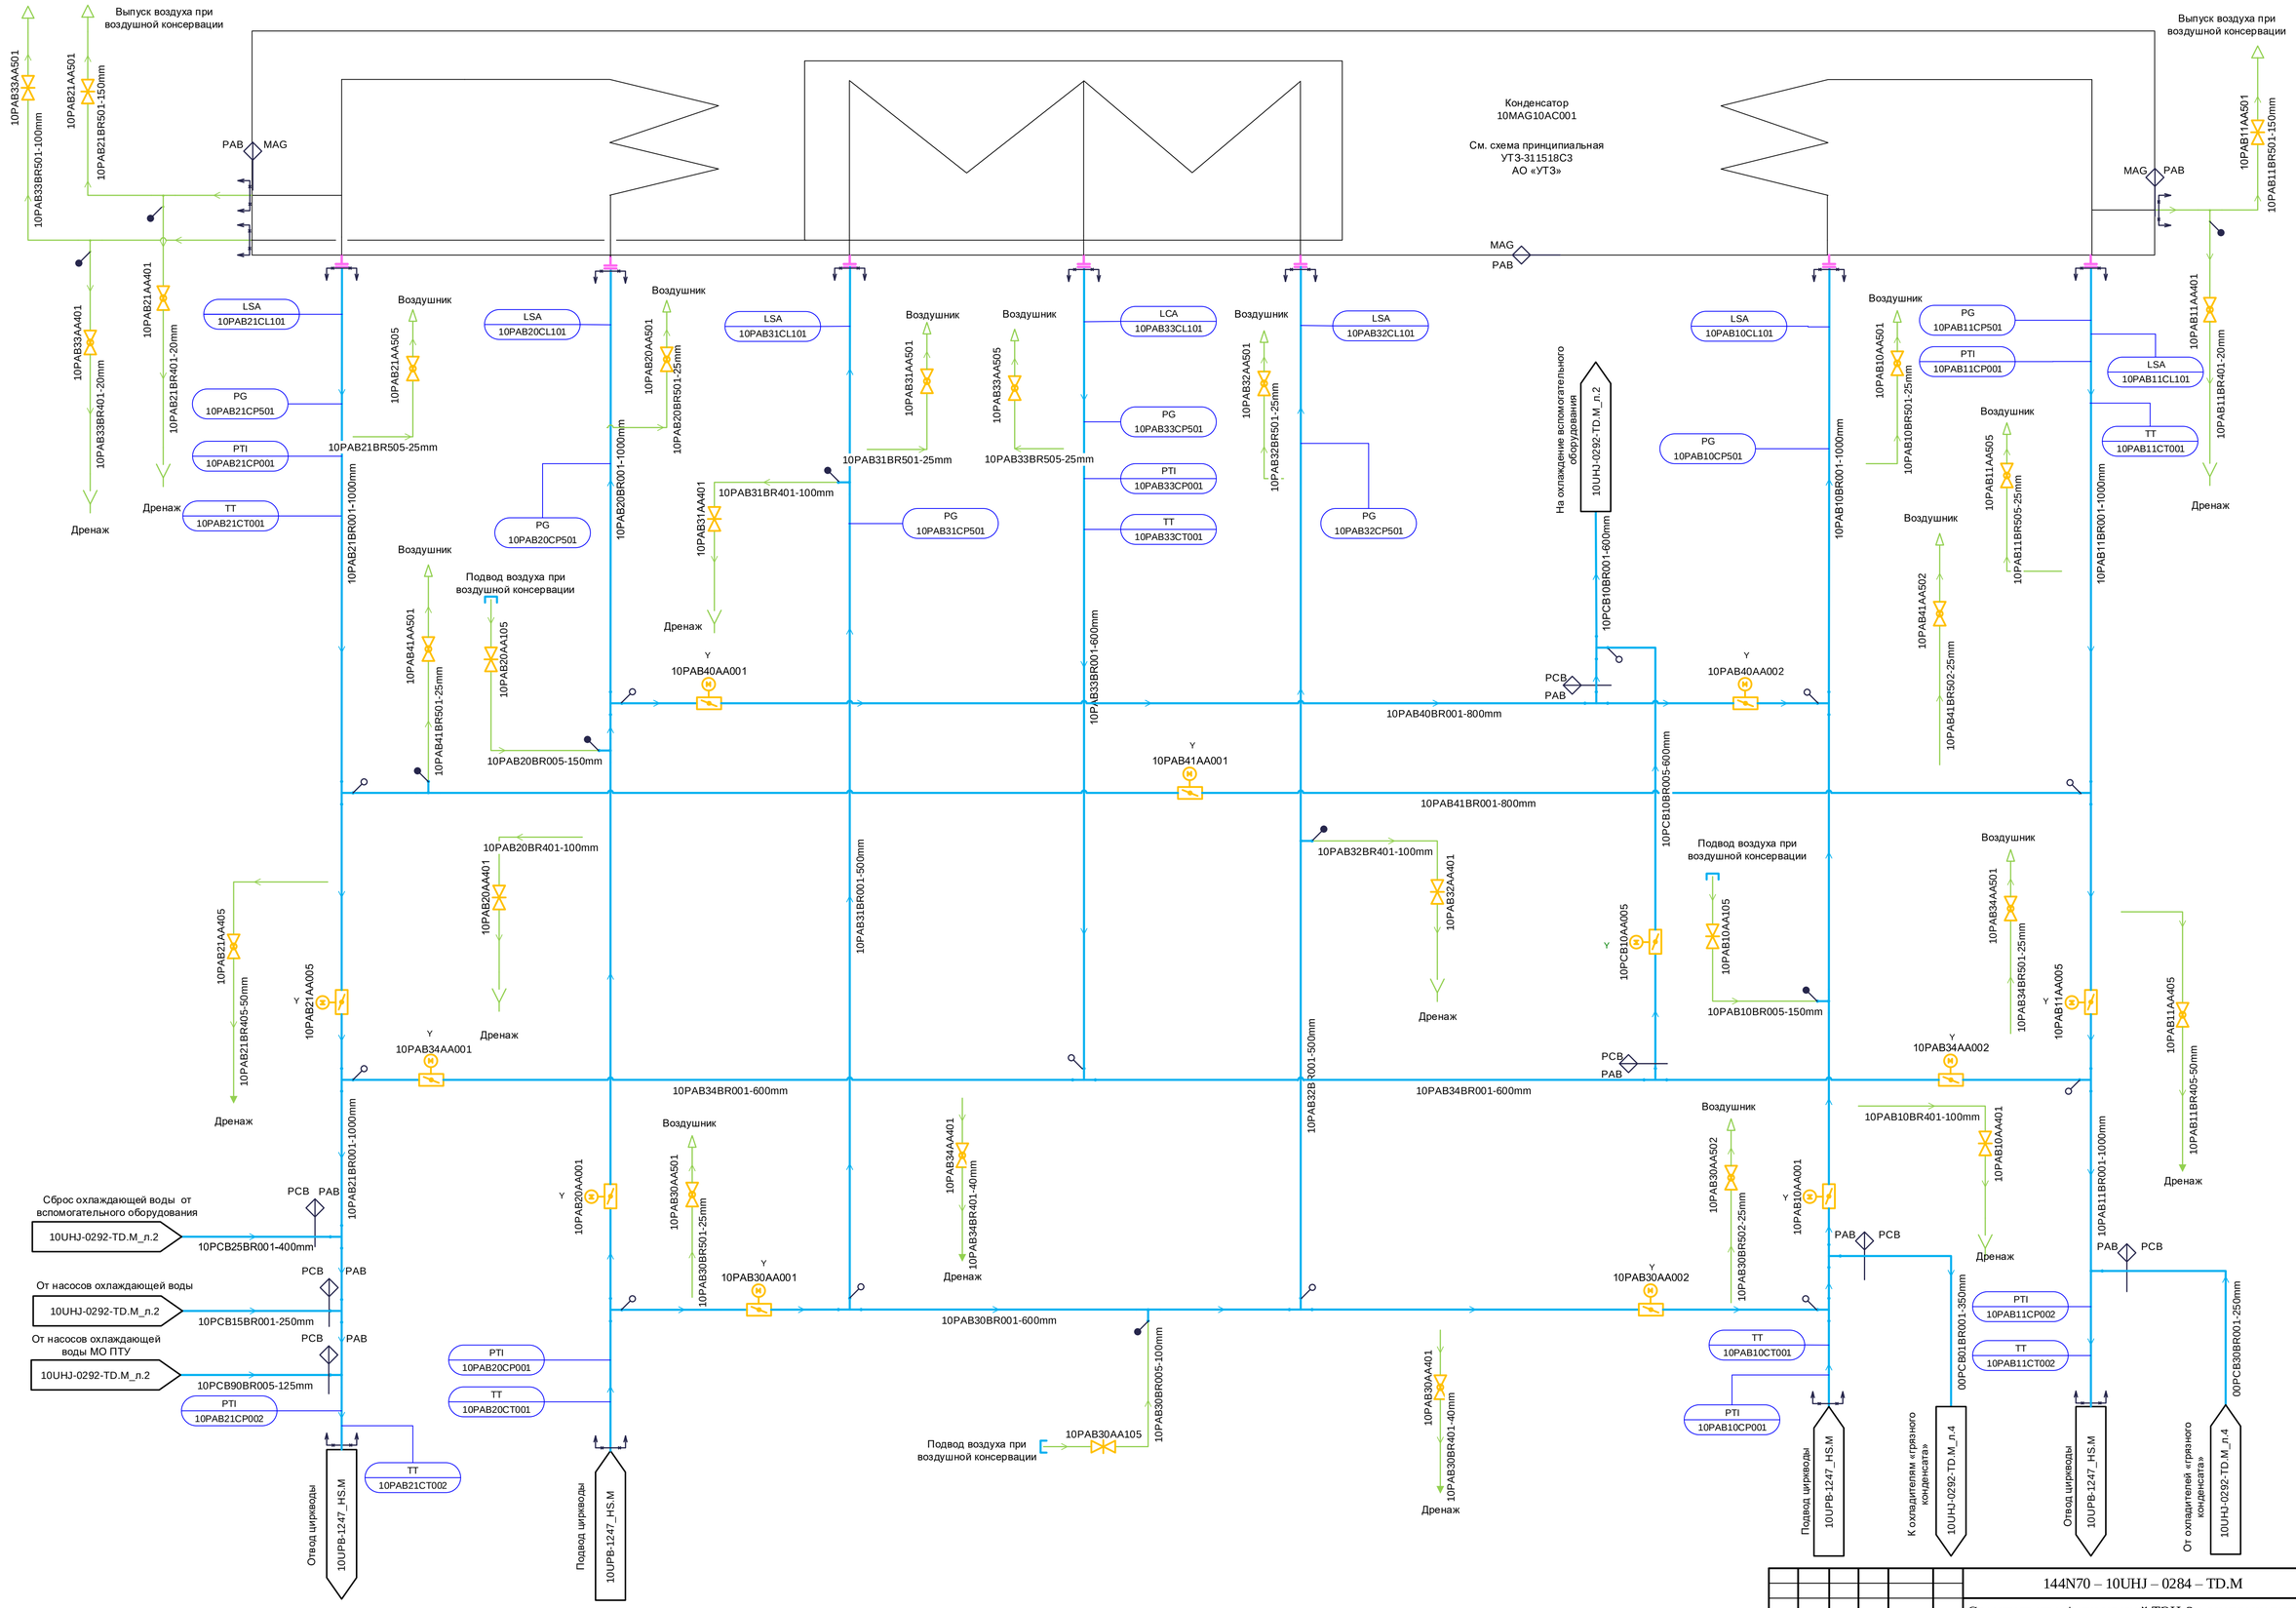

Изм.	Кол.уч	Лист	№ док.	Подп.	Дата	144N70 – 10UHJ – 0284 – TD.M
						Строительство Артемовской ТЭЦ-2 с внеплощадочной инфраструктурой
Разработал		Дёмина				Здание главного корпуса с баковым хозяйством. P&I-диаграмма трубопроводов циркуляционной охлаждающей воды
Проверил		Смирнова				
Н. контр.		Астраханцев				PI-Диаграмма трубопроводов циркуляционной охлаждающей воды. Система PAB

Стадия	Лист	Листов
Р	2	

АКЦИОНЕРНОЕ ОБЩЕСТВО ИНСТИТУТ ТЕПЛОЭЛЕКТРОПРОЕКТ г. МОСКВА

Согласовано

ОАСУ

Взам. инв. №

Подпись и дата

Инв. № подл.

Формат А1