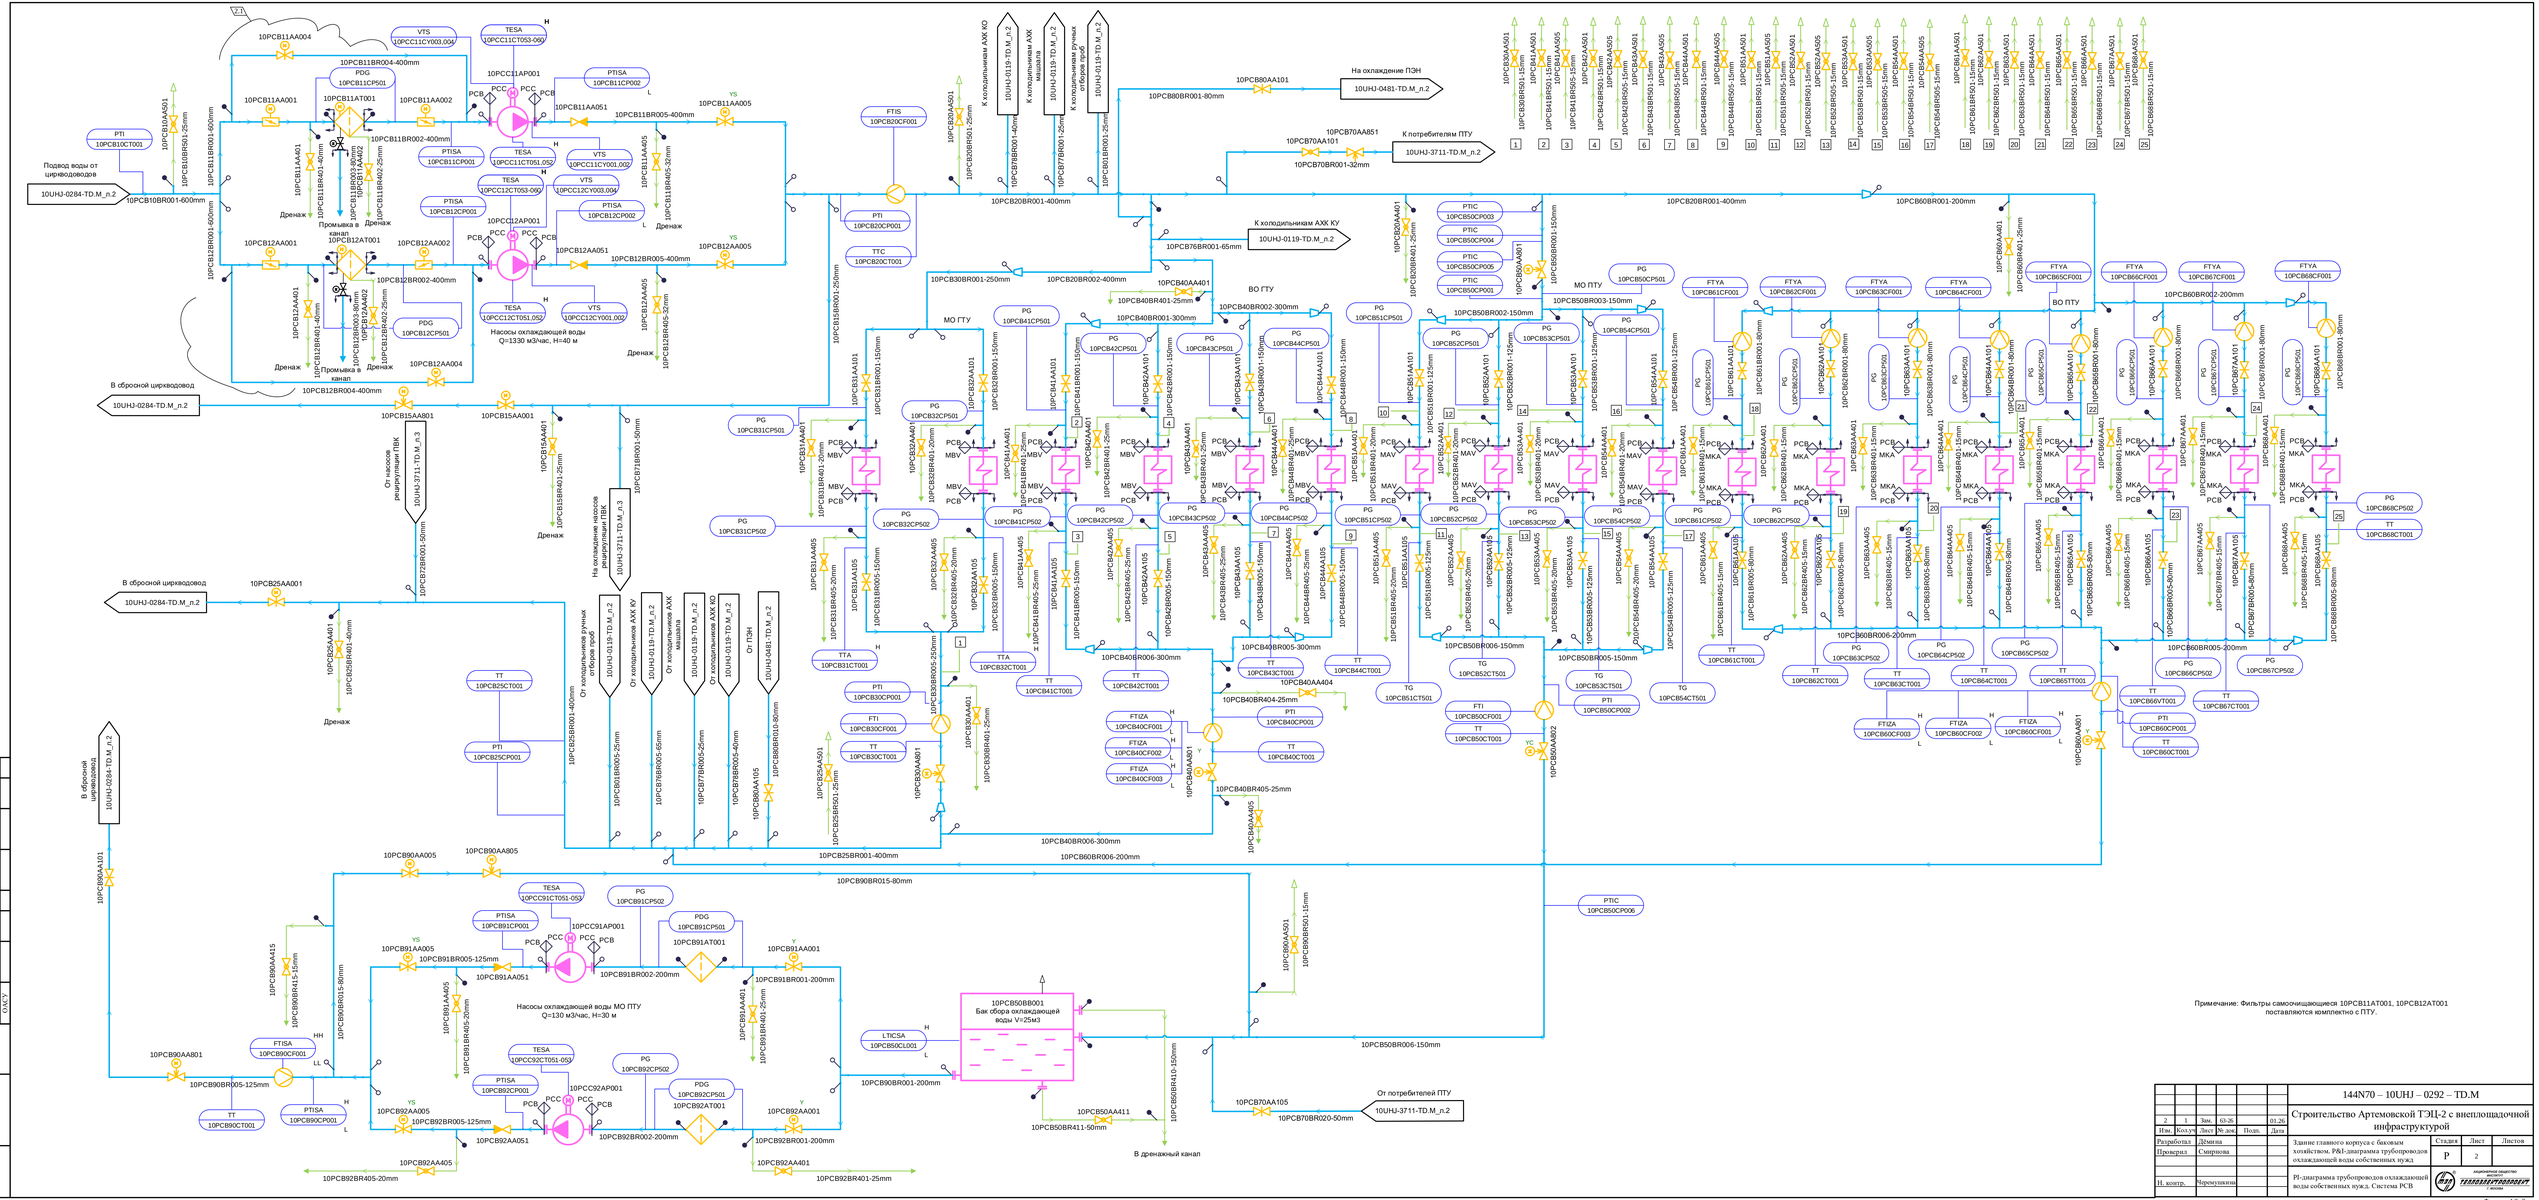
Подвод воды от циркводоводов
10UHJ-0284-TD.M_n.2
В сбросной циркводовод
10UHJ-0284-TD.M_n.2
Насосы охлаждающей воды Q=1330 м3/час, H=40 м
Насосы охлаждающей воды МО ПТУ Q=130 м3/час, H=30 м
10PCB50BB001 Бак сбора охлаждающей воды V=25м3
К потребителям ПТУ
10UHJ-3711-TD.M_n.2
На охлаждение ПЭН
10UHJ-0481-TD.M_n.2
К колодильникам АХК КУ
10UHJ-0119-TD.M_n.2
МО ПТУ
ВО ПТУ
МО ГТУ
ВО ГТУ
В дренажный канал
Примечание: Фильтры самоочищающиеся 10PCB11AT001, 10PCB12AT001 поставляются комплектно с ПТУ.
144N70 – 10UHJ – 0292 – TD.M
Строительство Артемовской ТЭЦ-2 с внеплощадочной инфраструктурой
Здание главного корпуса с боковым хозяйством, РФ-диаграмма трубопроводов охлаждающей воды собственных нужд
РФ-диаграмма трубопроводов охлаждающей воды собственных нужд. Система PCB
Разработал Демина
Проверил Смирнова
Н. контр. Черемушкина
Стадия Р
Лист 2
Листов
Согласовано
ОАХУ
Взам. инв. №
Подпись и дата
Инв. № подл.
Формат А2х3