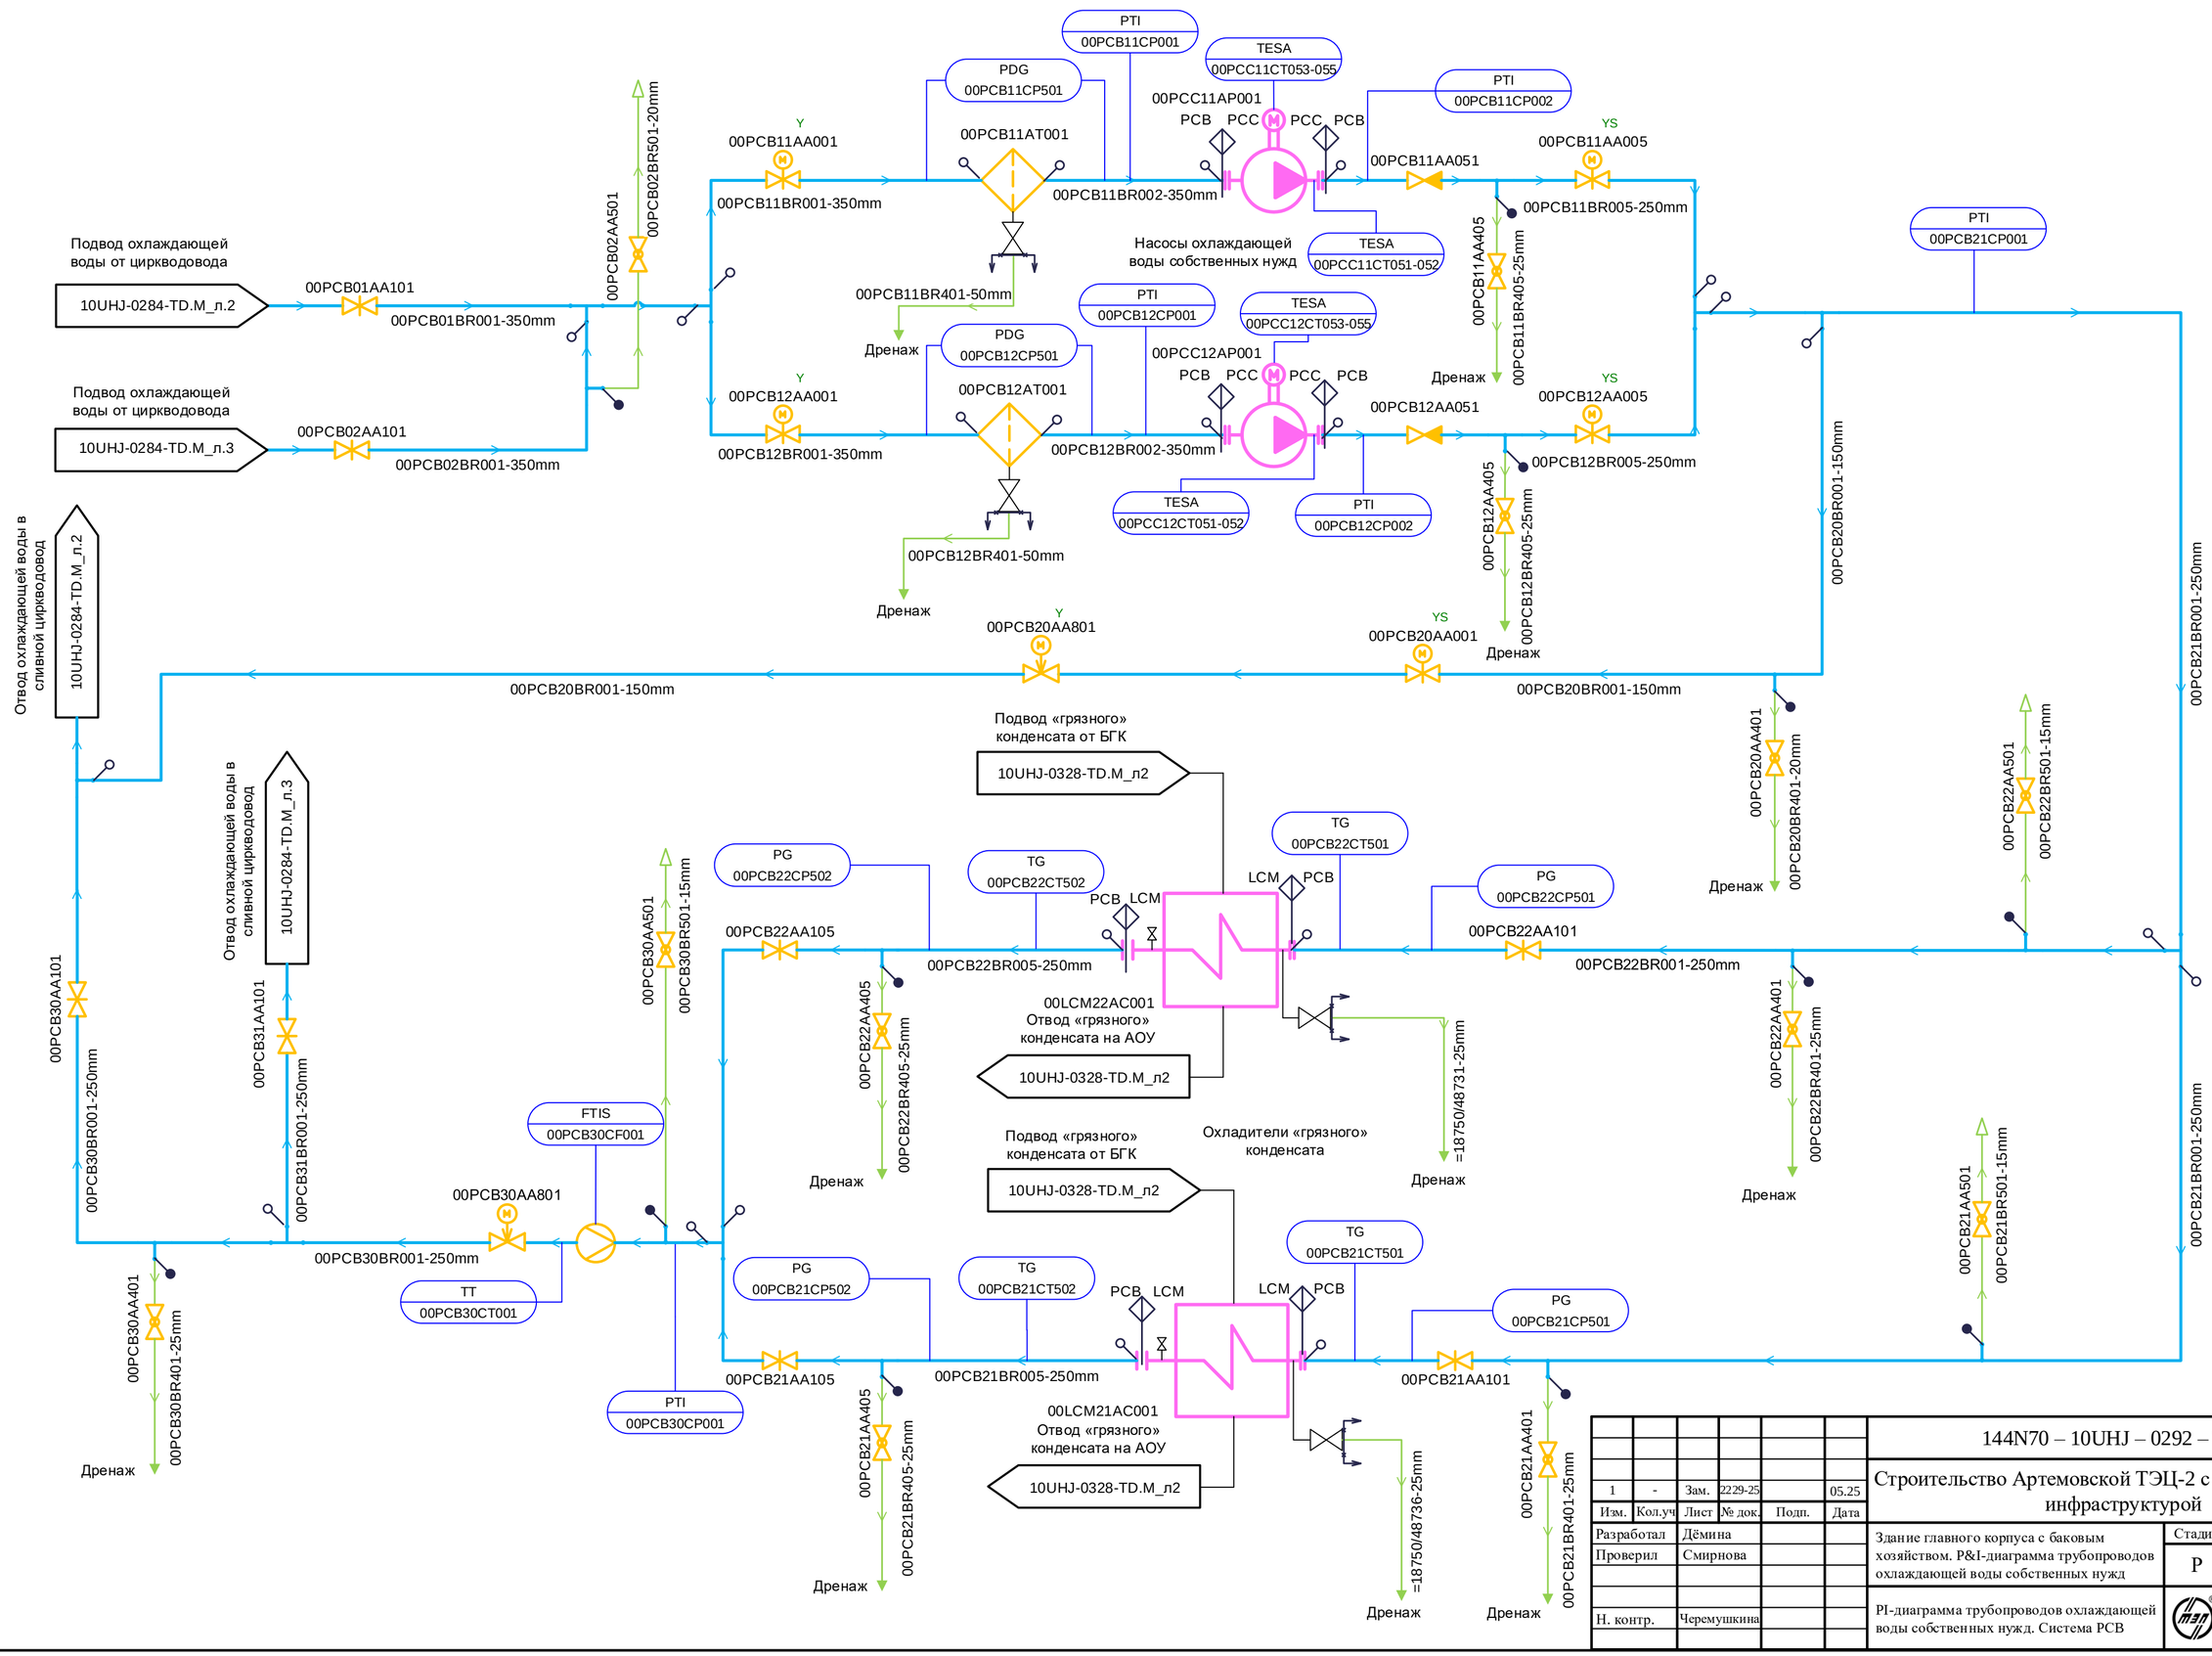

1	-	Зам.	2229-25		05.25	
Изм.	Кол.уч	Лист	№ док.	Подп.	Дата	
Разработал		Дёмина				
Проверил		Смирнова				
Н. контр.		Черемушкина				

144N70 – 10UHJ – 0292 – TD.M

Строительство Артемовской ТЭЦ-2 с внеплощадочной инфраструктурой

Здание главного корпуса с баковым хозяйством. P&I-диаграмма трубопроводов охлаждающей воды собственных нужд

Стадия	Лист	Листов
Р	4	

PI-диаграмма трубопроводов охлаждающей воды собственных нужд. Система PCB

АКЦИОНЕРНОЕ ОБЩЕСТВО ИНСТИТУТ ТЕПЛОЭЛЕКТРОПРОЕКТ Г. МОСКВА

Согласовано

ОАСУ

Взам. инв. №

Подпись и дата

Инв. № подл.

Формат А2