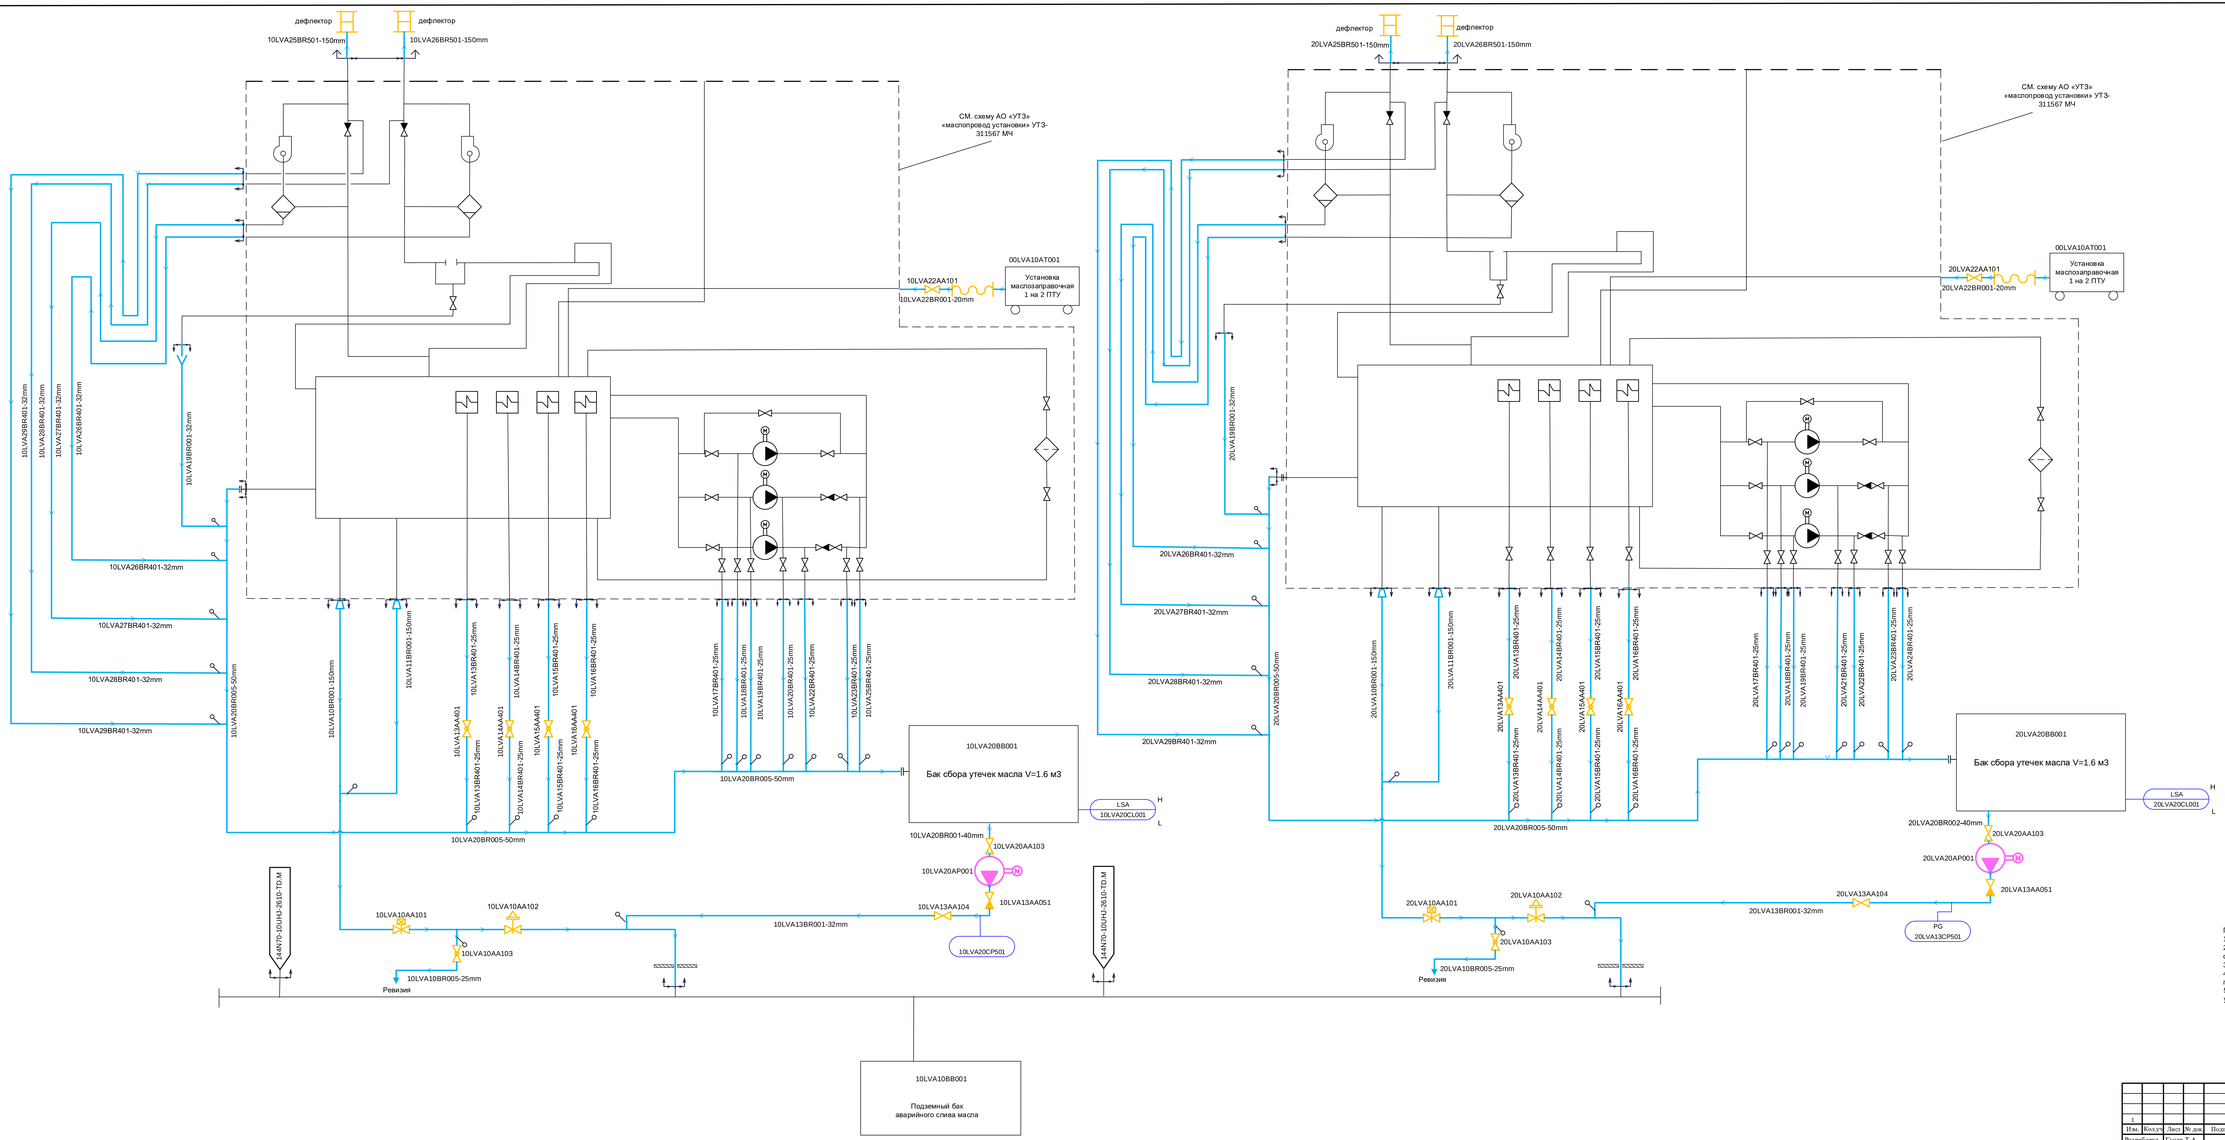

Примечание:
1.Управление насосами 10LVA20AP001 и 20LVA20AP001 по месту.
2.При снижении уровня в баках 10LVA20BB001, 20LVA20BB001 сбора утечек масла до Мп1 значения отключения насосов.
3.Сигнализация высокого уровня в баках сбора утечек масла.
4.Задвижки 10LVA10AA102 , 20LVA10AA102 оснащены колонковым приводом.
5.Задвижка 10LVA10AA101,20LVA10AA101 оснащена замковым устройством.

							144N70-10UHJ-0301-TD.M		
1							Строительство Артемовской ТЭЦ-2 с внеплощадочной инфраструктурой		
Изм.	Кол.уч	Лист	№ док.	Подп.	Дата				
Разработал		Гуссев Т.А.					Главный корпус.РТ-Диаграмма трубопроводов маслосистемы.	Стадия	Лист	Листов
Т.контр.		Смирнова						Р	2	
Н. контр.		Черемушкина					РТ-Диаграмма трубопроводов маслосистемы ПТ. Система LVA.	АКЦИОНЕРНОЕ ОБЩЕСТВО ТЕХЭНЕРГОПРОМФИН	

Согласовано

Взам. инв. №

Подпись и дата

Инв. № подл.

Формат А2х3