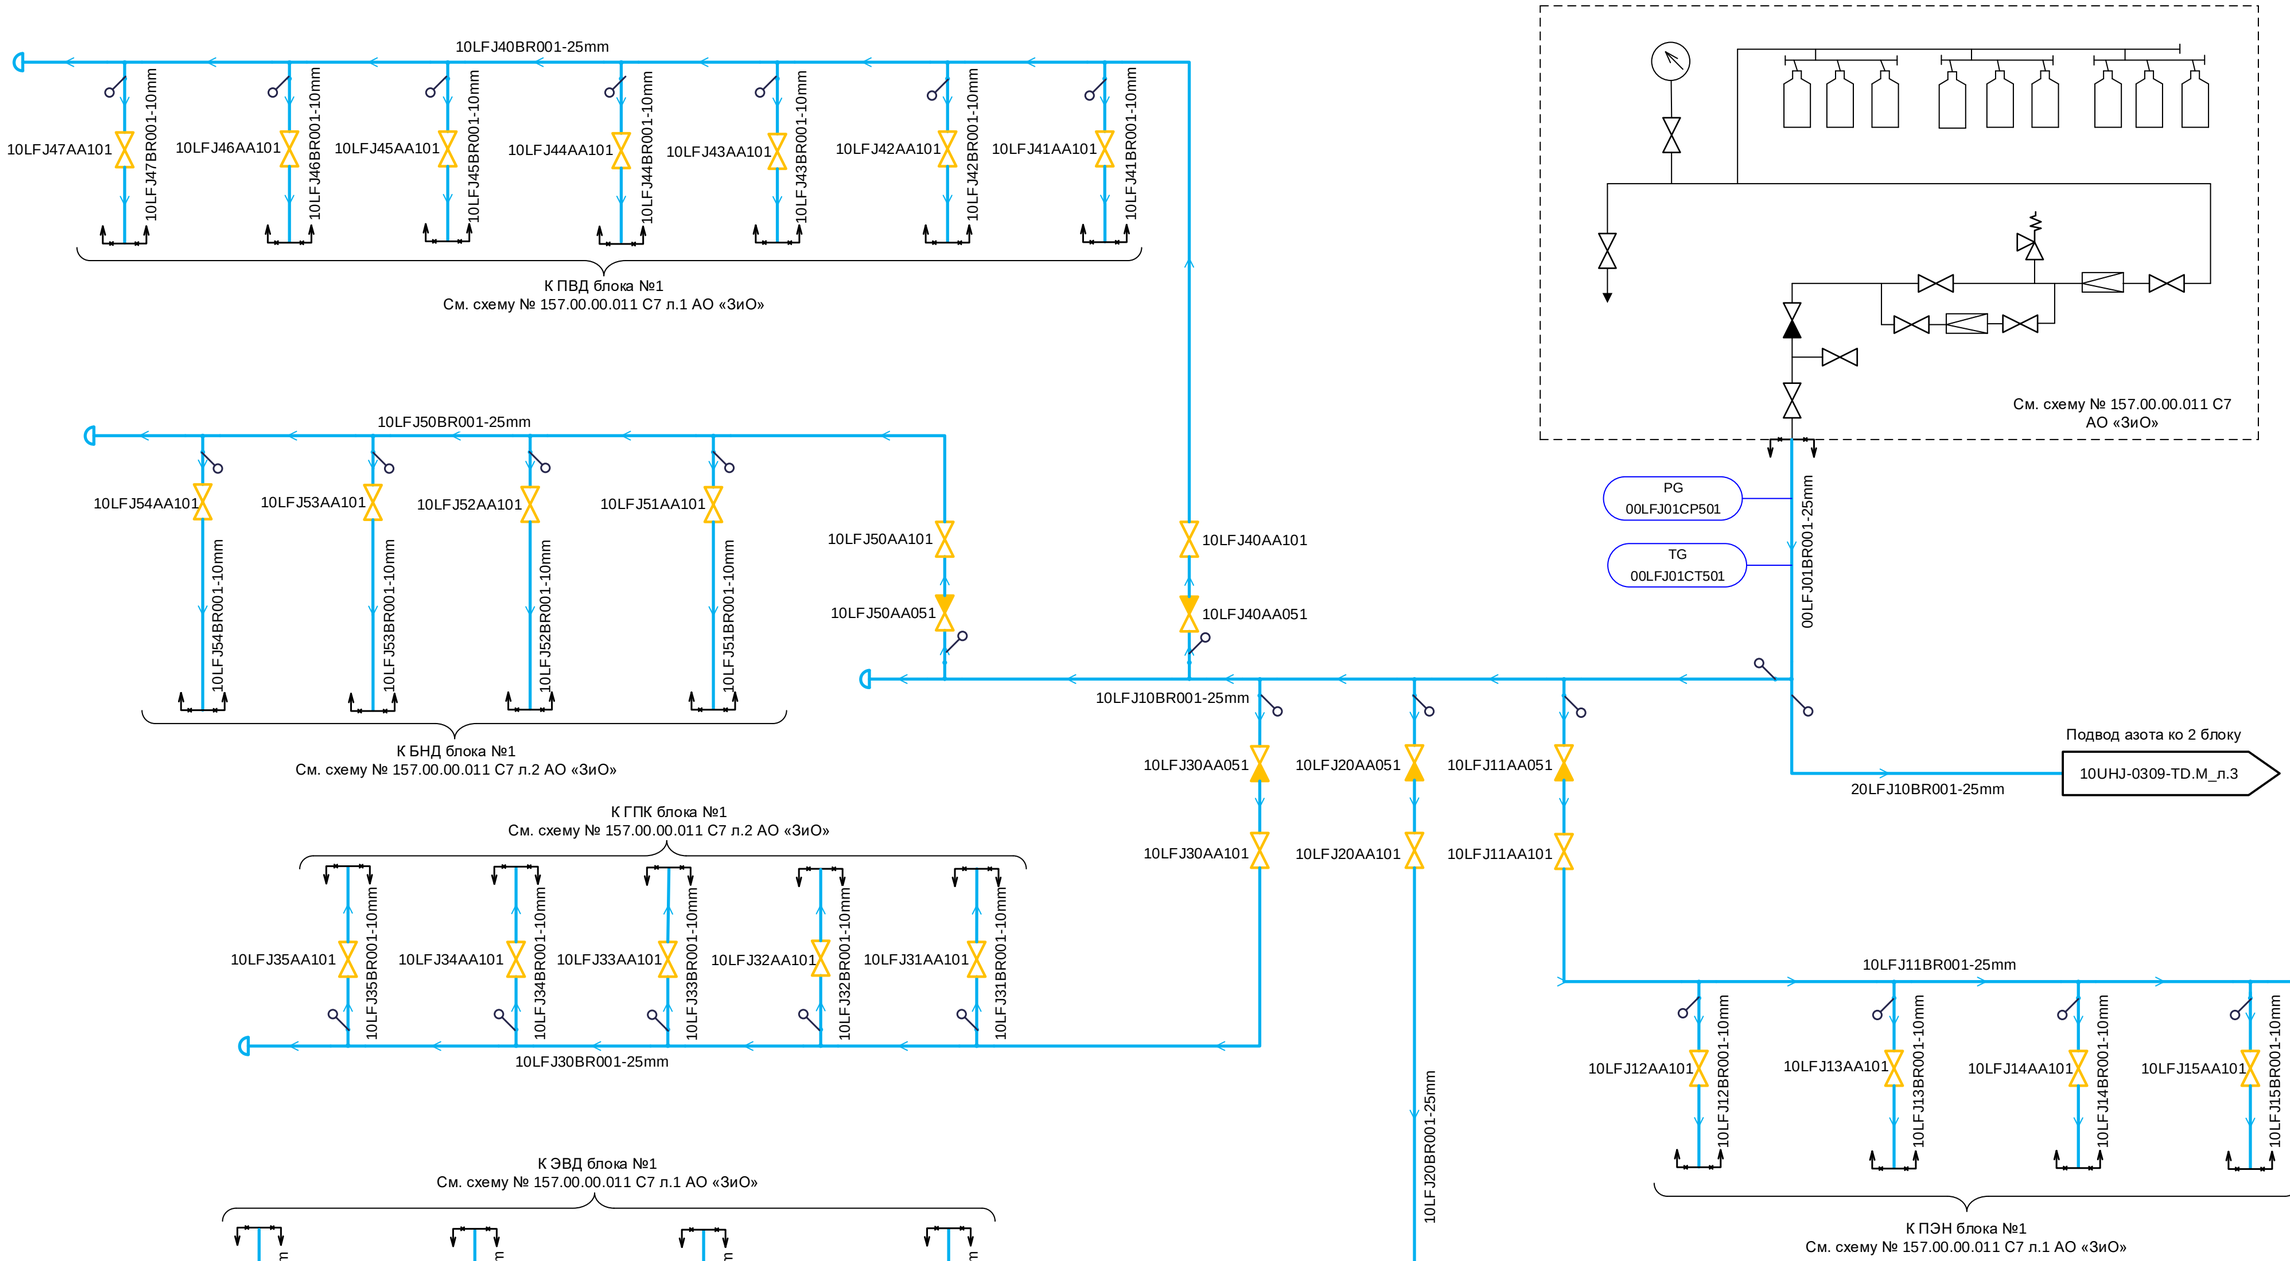

						144N70-10UHJ-0309-TD.M		
						Артемовская ТЭЦ-2 с внеплощадочной инфраструктурой		
Изм.	Кол.уч	Лист	№ док.	Подп.	Дата			
Разработал		Дроздов				Здание главного корпуса с баковым хозяйством. PI-диаграмма трубопроводов азотной консервации.	Стадия	Лист	Листов
Проверил		Демина					Р	2	
Н. контр.		Астраханцев				PI-диаграмма трубопроводов азотной консервации. Система LFJ.	АКЦИОНЕРНОЕ ОБЩЕСТВО ИНСТИТУТ ТЕПЛОЭЛЕКТРОПРОЕКТ Г. МОСКВА		

Согласовано

ОЛСУ

Взам. инв. №

Подпись и дата

Инв. № подл.

Формат А2