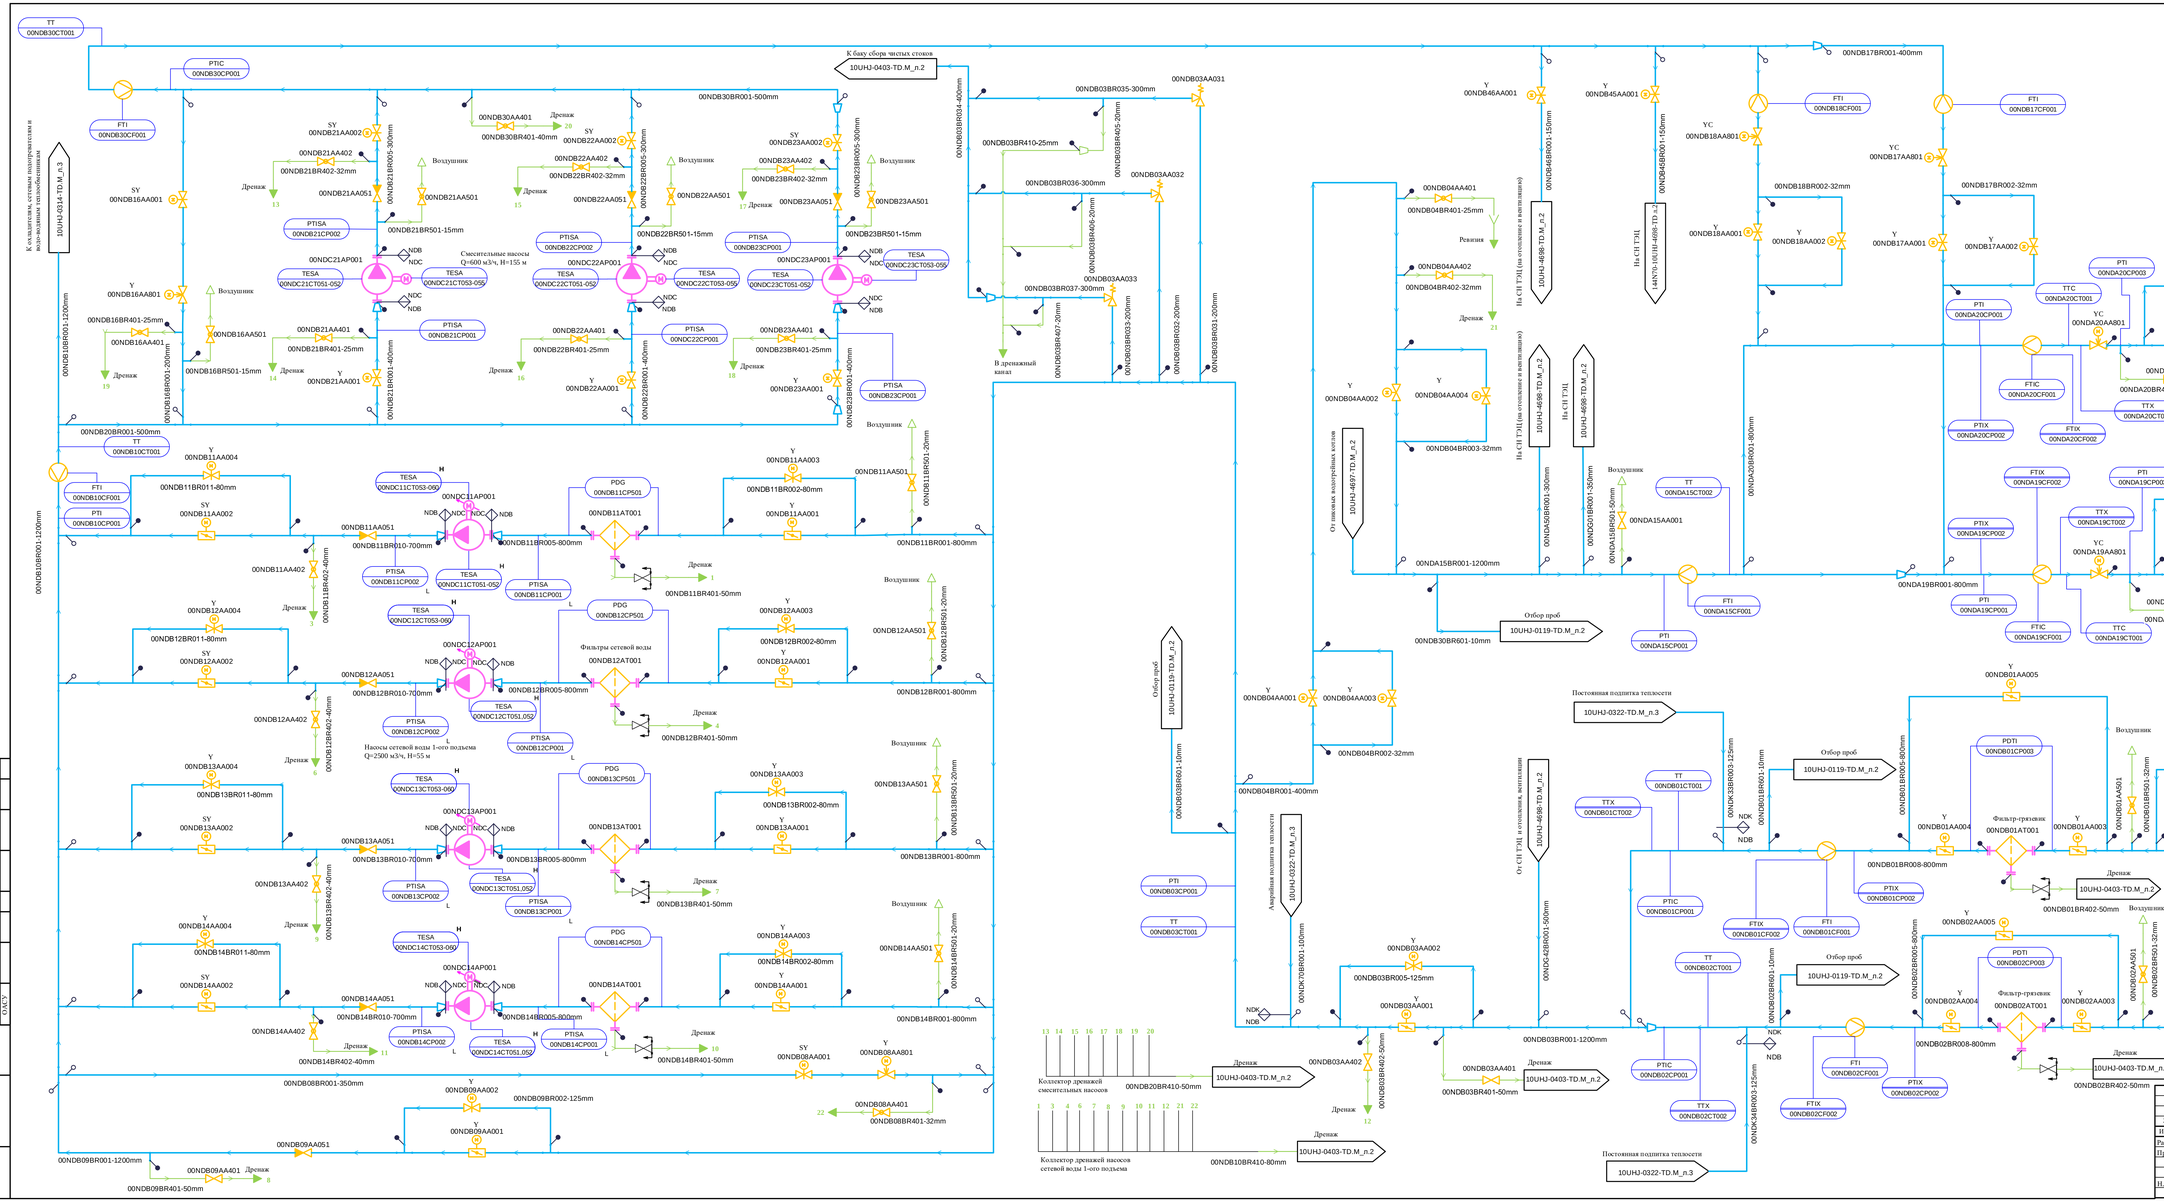
К баку сбора чистых стоков
10UHJ-0403-TD.M_n.2
К охладителям сетевых подогревателей и на подпитку теплофикации
10UHJ-0314-TD.M_n.3
Смесительные насосы Q=600 м3/ч, H=155 м
Насосы сетевой воды 1-ого подъема Q=2500 м3/ч, H=55 м
Фильтры сетевой воды
Коллектор дренажей смесительных насосов
Коллектор дренажей насосов сетевой воды 1-ого подъема
В дренажный канал
Отбор проб
10UHJ-0119-TD.M_n.2
Аварийная подпитка теплосети
10UHJ-0322-TD.M_n.3
Постоянная подпитка теплосети
10UHJ-0322-TD.M_n.3
От пиковых водогрейных котлов
10UHJ-4697-TD.M_n.2
На СП ТЭЦ (на отопление и вентиляцию)
10UHJ-4698-TD.M_n.2
Главный корпус
Эстакада
Прямая сетевая вода к пос. Заводской, ФГУП «Дальневосточное» УПТФ, пос. Артемовский и с. Суражевка
144N70-10UTZ-2854-TD.M
Прямая сетевая вода к г.Артем
Обратная сетевая вода от г.Артем
Обратная сетевая вода от пос. Заводской, ФГУП «Дальневосточное» УПТФ, пос. Артемовский и с. Суражевка
144N70-10UHJ-0314-TD.M
Строительство Артемовской ТЭЦ-2 с внеплощадной инфраструктурой
Здание главного корпуса с баковым хозяйством. PI-диаграмма трубопроводов сетевой воды
PI-Диаграмма трубопроводов сетевой воды. Система NDA, NDB, NDC
Разработал Салишева
Проверил Дёмина
Н. контр. Чернушкина
Стадия Р
Лист 2
Листов
Согласовано
ОАХУ
Инв. № подл.
Подпись и дата
Взам. инв. №
Формат А2х3