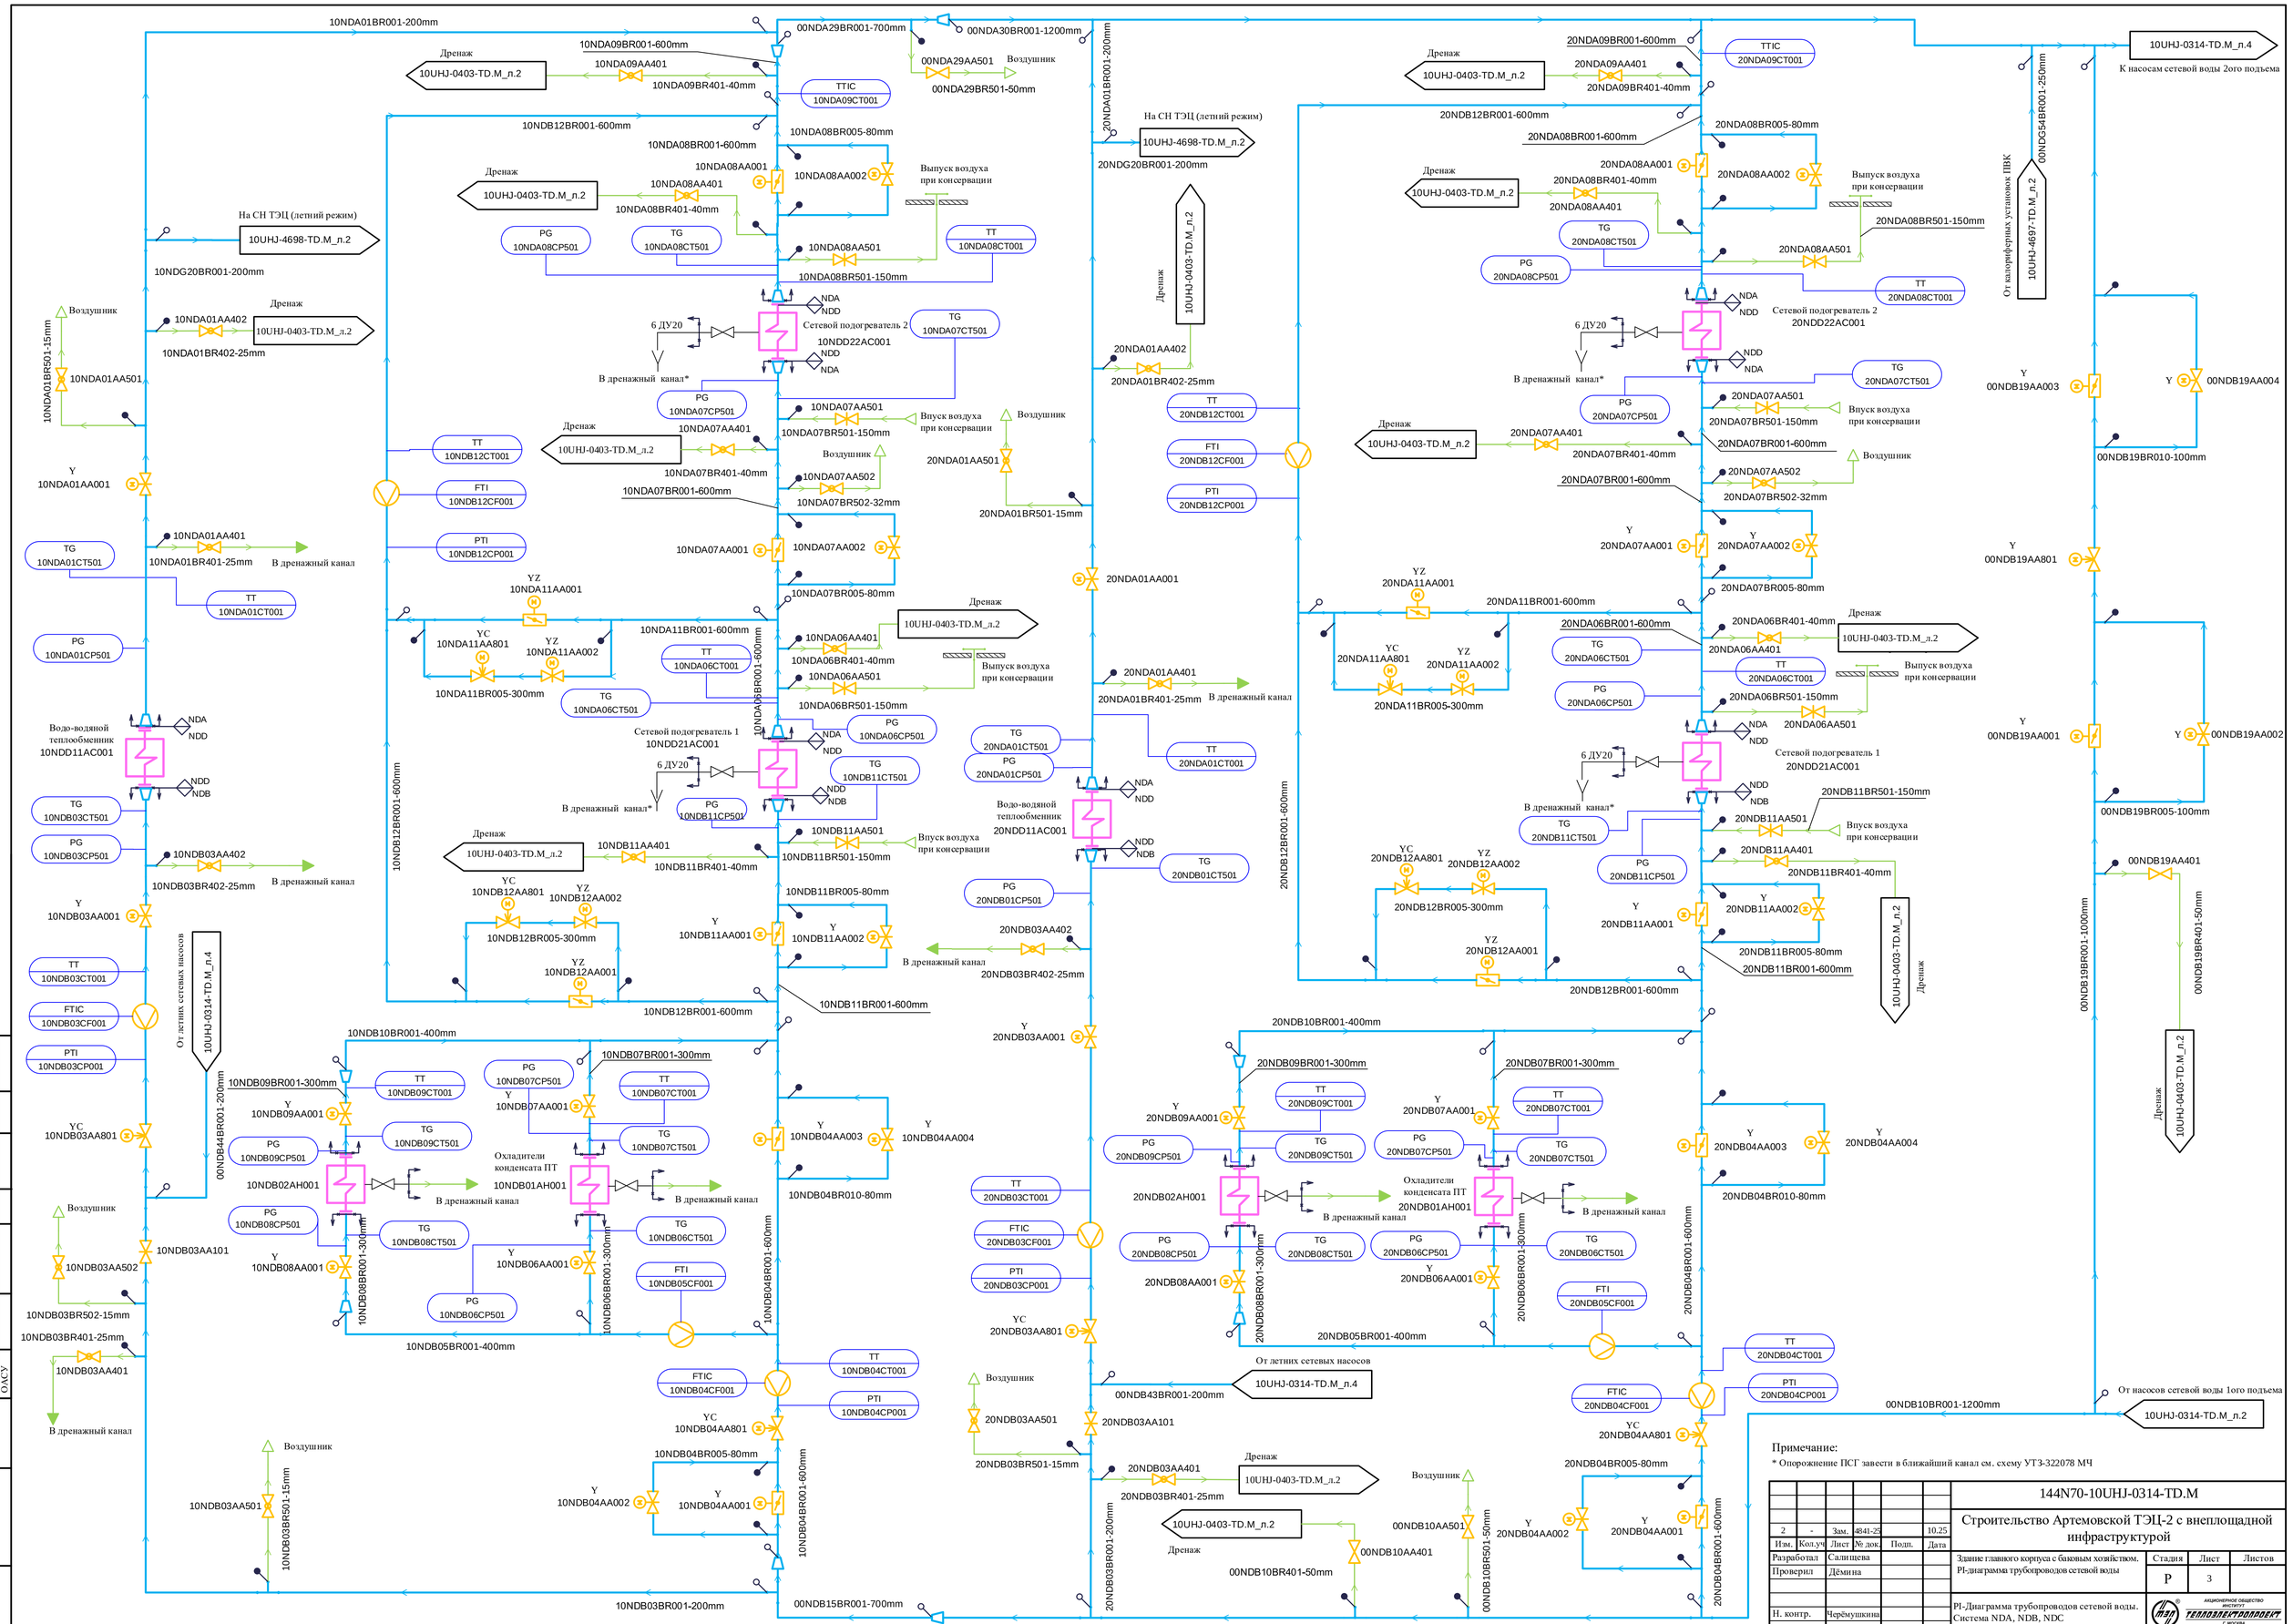

Примечание:

* Опорожнение ПСГ завести в ближайший канал см. схему УТЗ-322078 МЧ

2	-	Зам.	4841-25		10.25	
Изм.	Кол.уч	Лист	№ док.	Подп.	Дата	
Разработал		Салищева				
Проверил		Дёмина				
Н. контр.		Черёмушкина				

144N70-10UHJ-0314-TD.M

Строительство Артемовской ТЭЦ-2 с внеплощадной инфраструктурой

Здание главного корпуса с базовым хозяйством. PI-диаграмма трубопроводов сетевой воды

PI-Диаграмма трубопроводов сетевой воды. Система NDA, NDB, NDC

Стадия	Лист	Листов
Р	3	

АКЦИОНЕРНОЕ ОБЩЕСТВО ИНСТИТУТ ТЕПЛОЭЛЕКТРОПРОЕКТ г. МОСКВА

Согласовано

ОАСУ

Взам. инв. №

Подпись и дата

Инв. № подл.

Формат А1