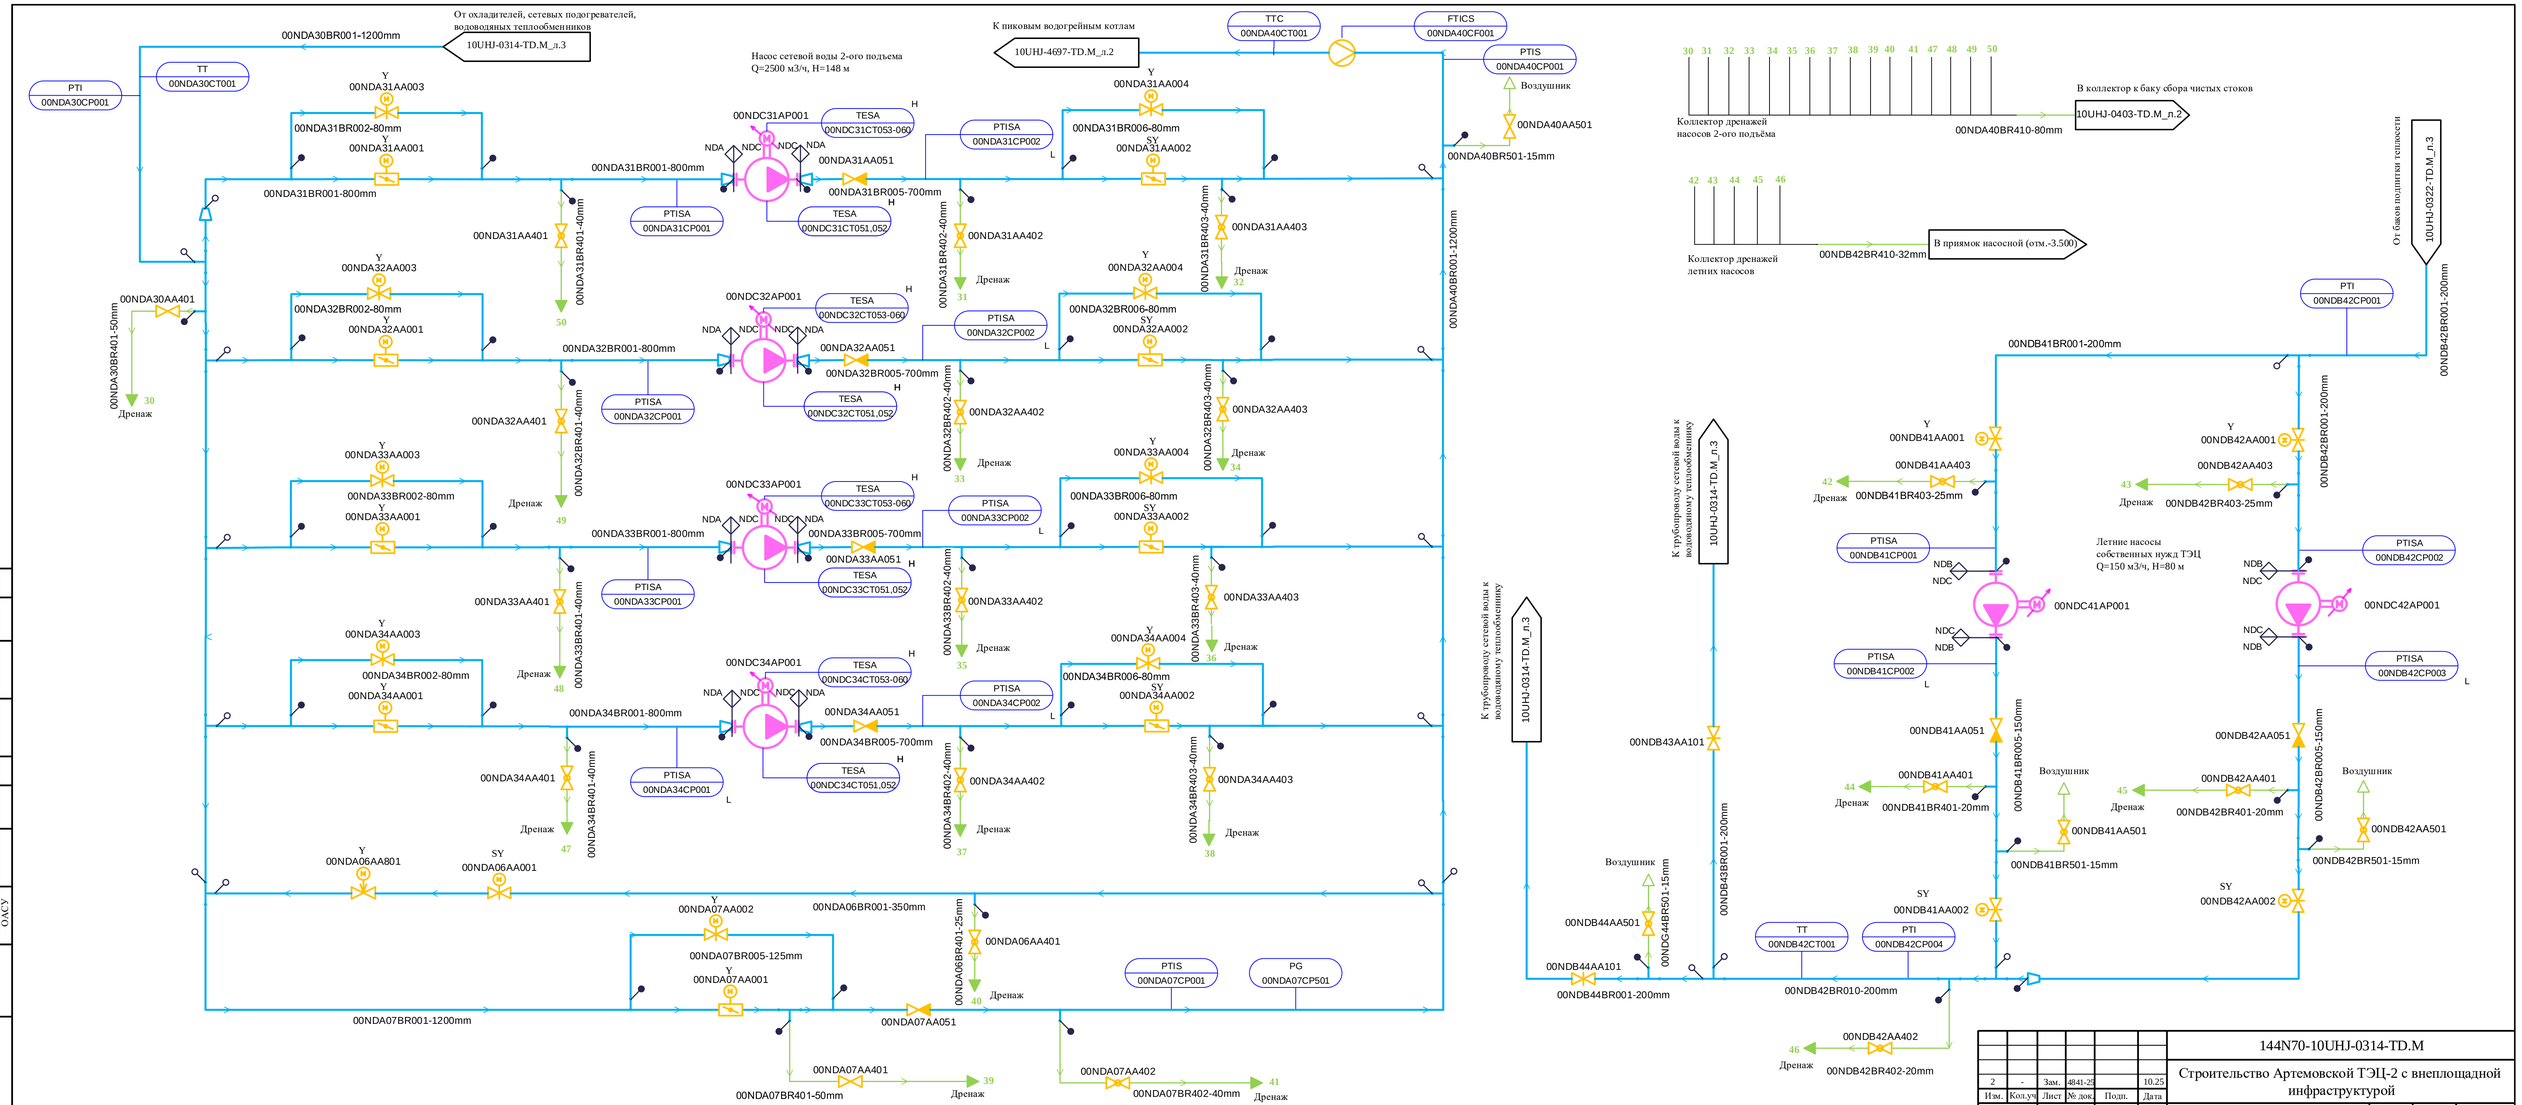

2	-	Зам.	4841-25		10.25	144N70-10UHJ-0314-TD.M	
Изм.	Кол.уч	Лист	№ док.	Подп.	Дата	Строительство Артемовской ТЭЦ-2 с внеплощадной инфраструктурой	
Разработал	Салищева					Здание главного корпуса с базовым хозяйством. PI-диаграмма трубопроводов сетевой воды	Стадия: Р; Лист: 4; Листов:
Проверил	Дёмина						
Н. контр.	Черёмушкина					PI-Диаграмма трубопроводов сетевой воды. Система NDA, NDB, NDC	АКЦИОНЕРНОЕ ОБЩЕСТВО ИНСТИТУТ ТЕПЛОЭЛЕКТРОПРОЕКТ Г. МОСКВА

Согласовано

ОАСУ

Взам. инв. №

Подпись и дата

Инв. № подл.

Формат А3х3