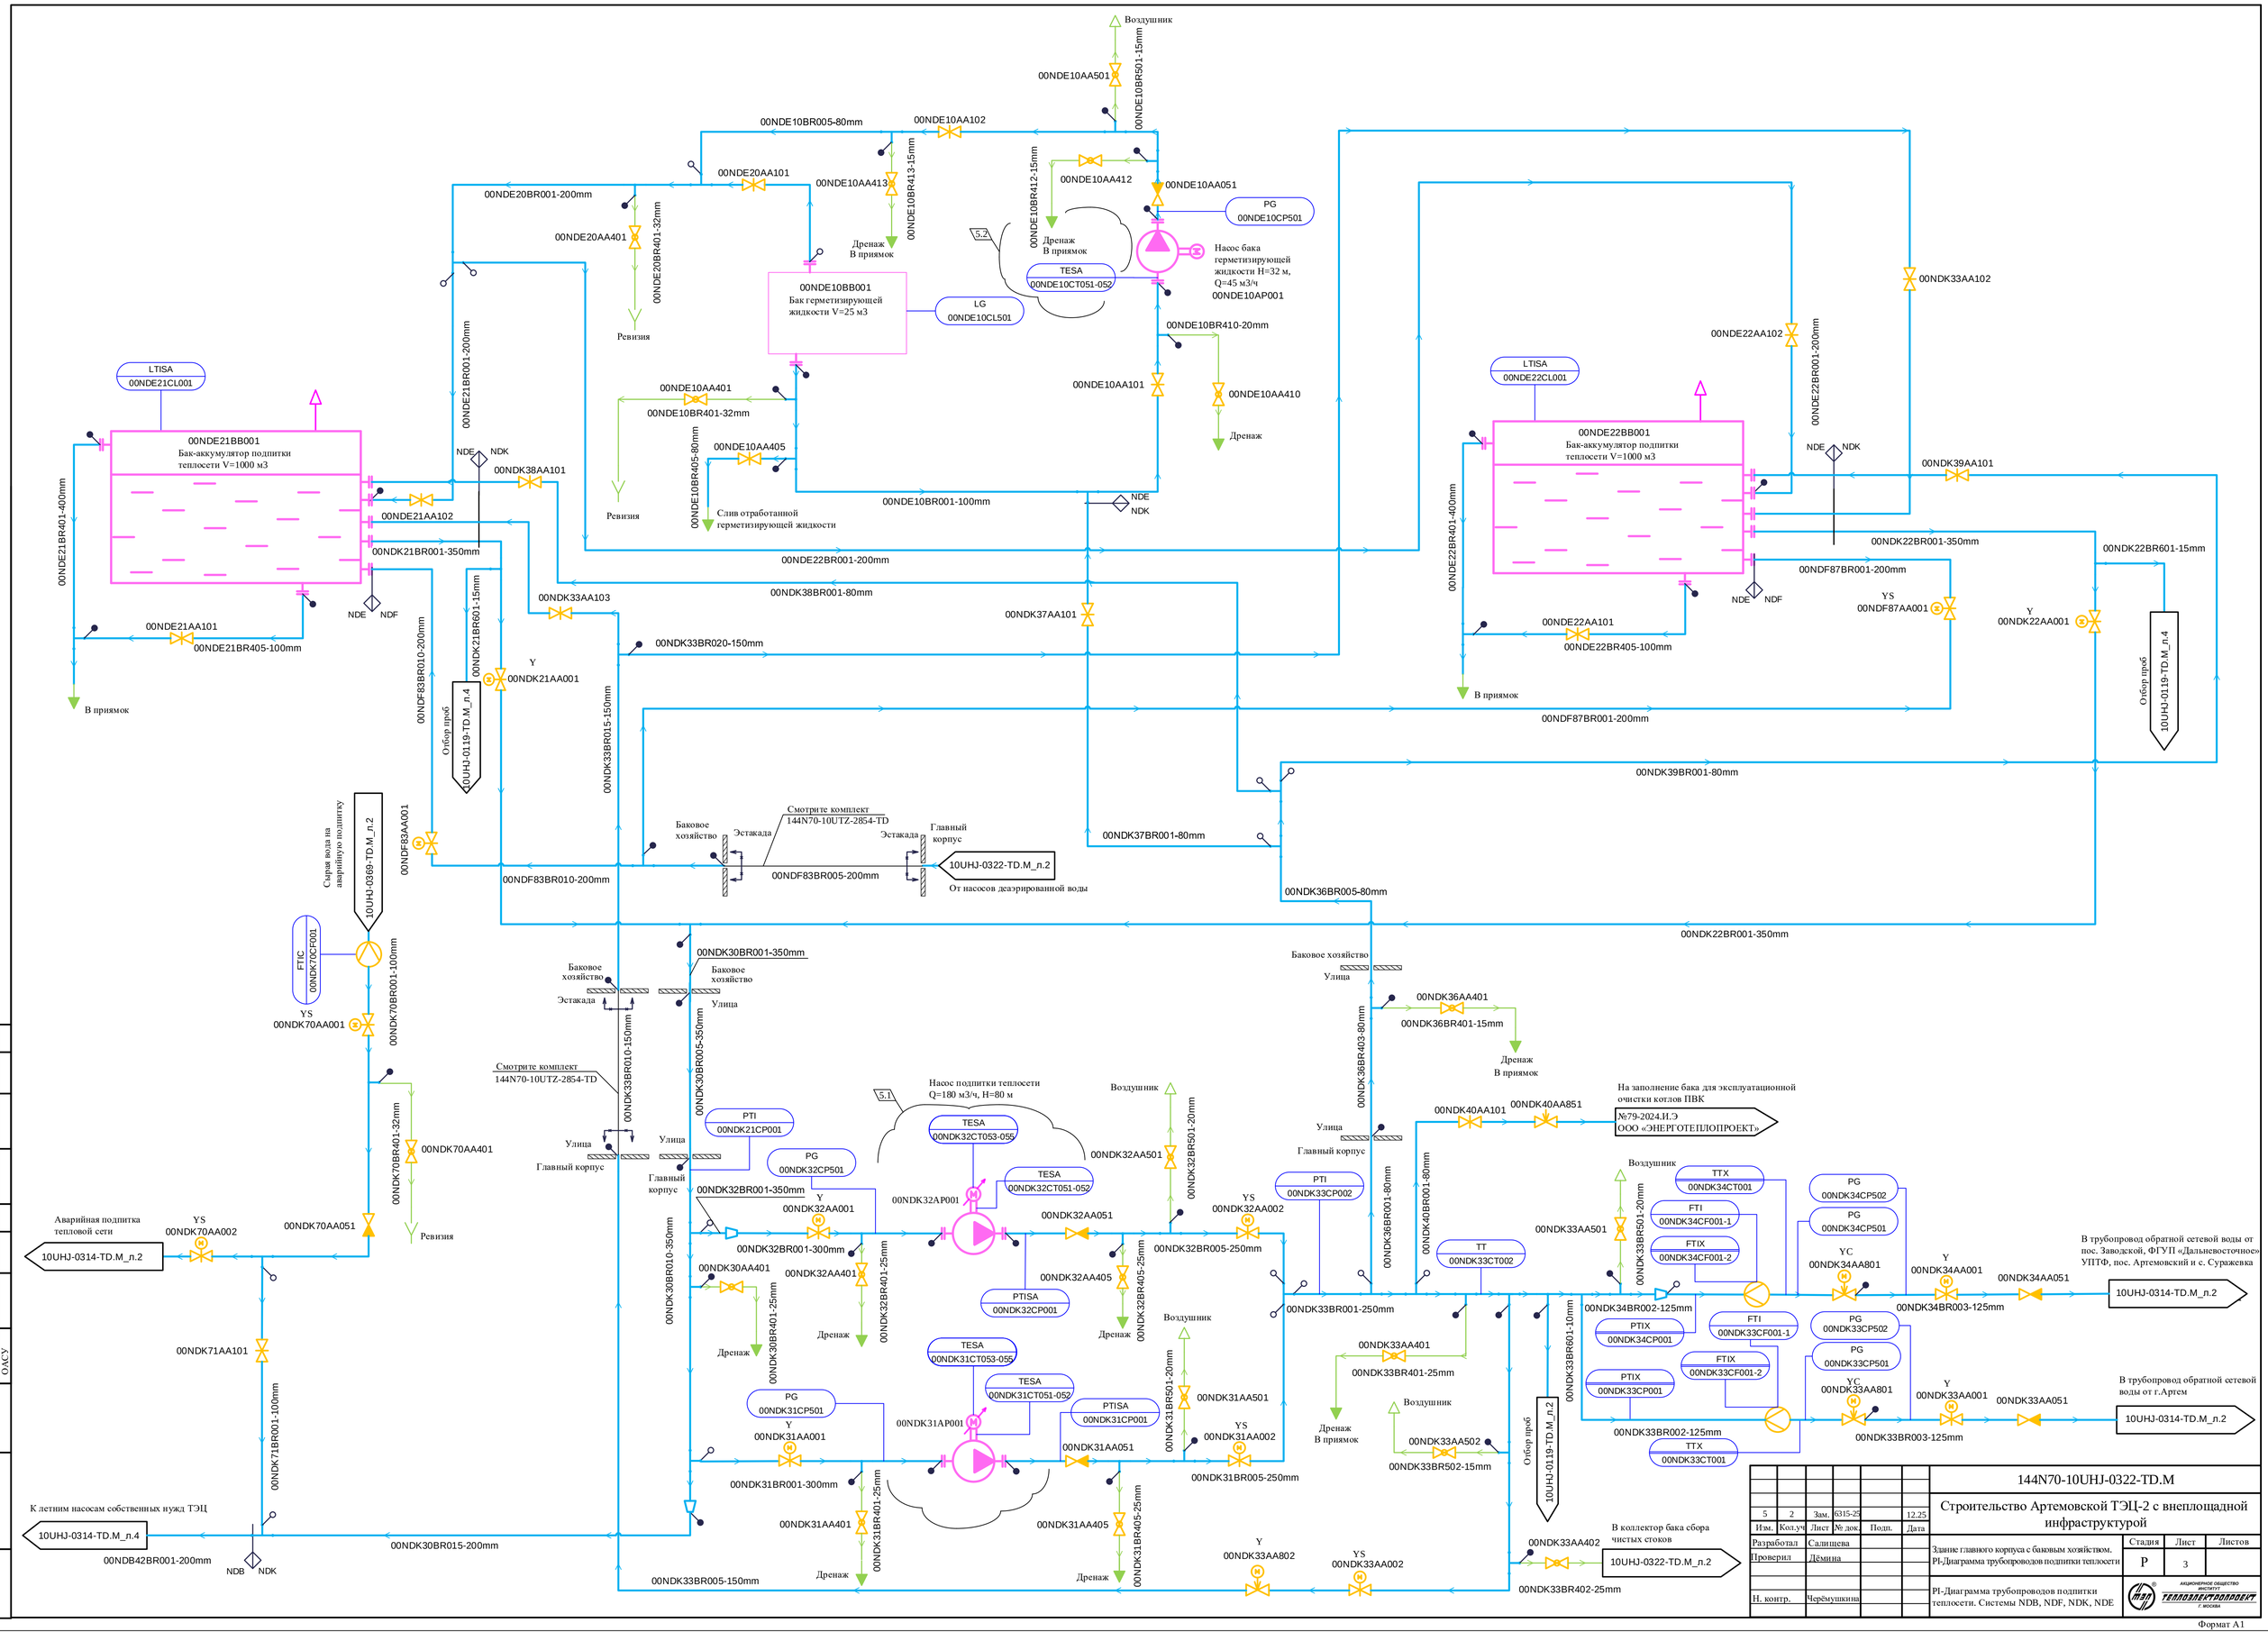

5	2	Зам.	6315-25			12.25
Изм.	Кол.уч	Лист	№ док.	Подп.		Дата
Разработал		Салищева				
Проверил		Дёмина				
Н. контр.		Черёмушкина				

144N70-10UHJ-0322-TD.M

Строительство Артемовской ТЭЦ-2 с внеплощадной инфраструктурой

Здание главного корпуса с баковым хозяйством. PI-Диаграмма трубопроводов подпитки теплосети

Стадия	Лист	Листов
Р	3	

PI-Диаграмма трубопроводов подпитки теплосети. Системы NDB, NDF, NDK, NDE

АКЦИОНЕРНОЕ ОБЩЕСТВО ИНСТИТУТ ТЕПЛОЭЛЕКТРОПРОЕКТ г. МОСКВА

Согласовано

ОАСУ

Взам. инв. №

Подпись и дата

Инв. № подл.

Формат А1