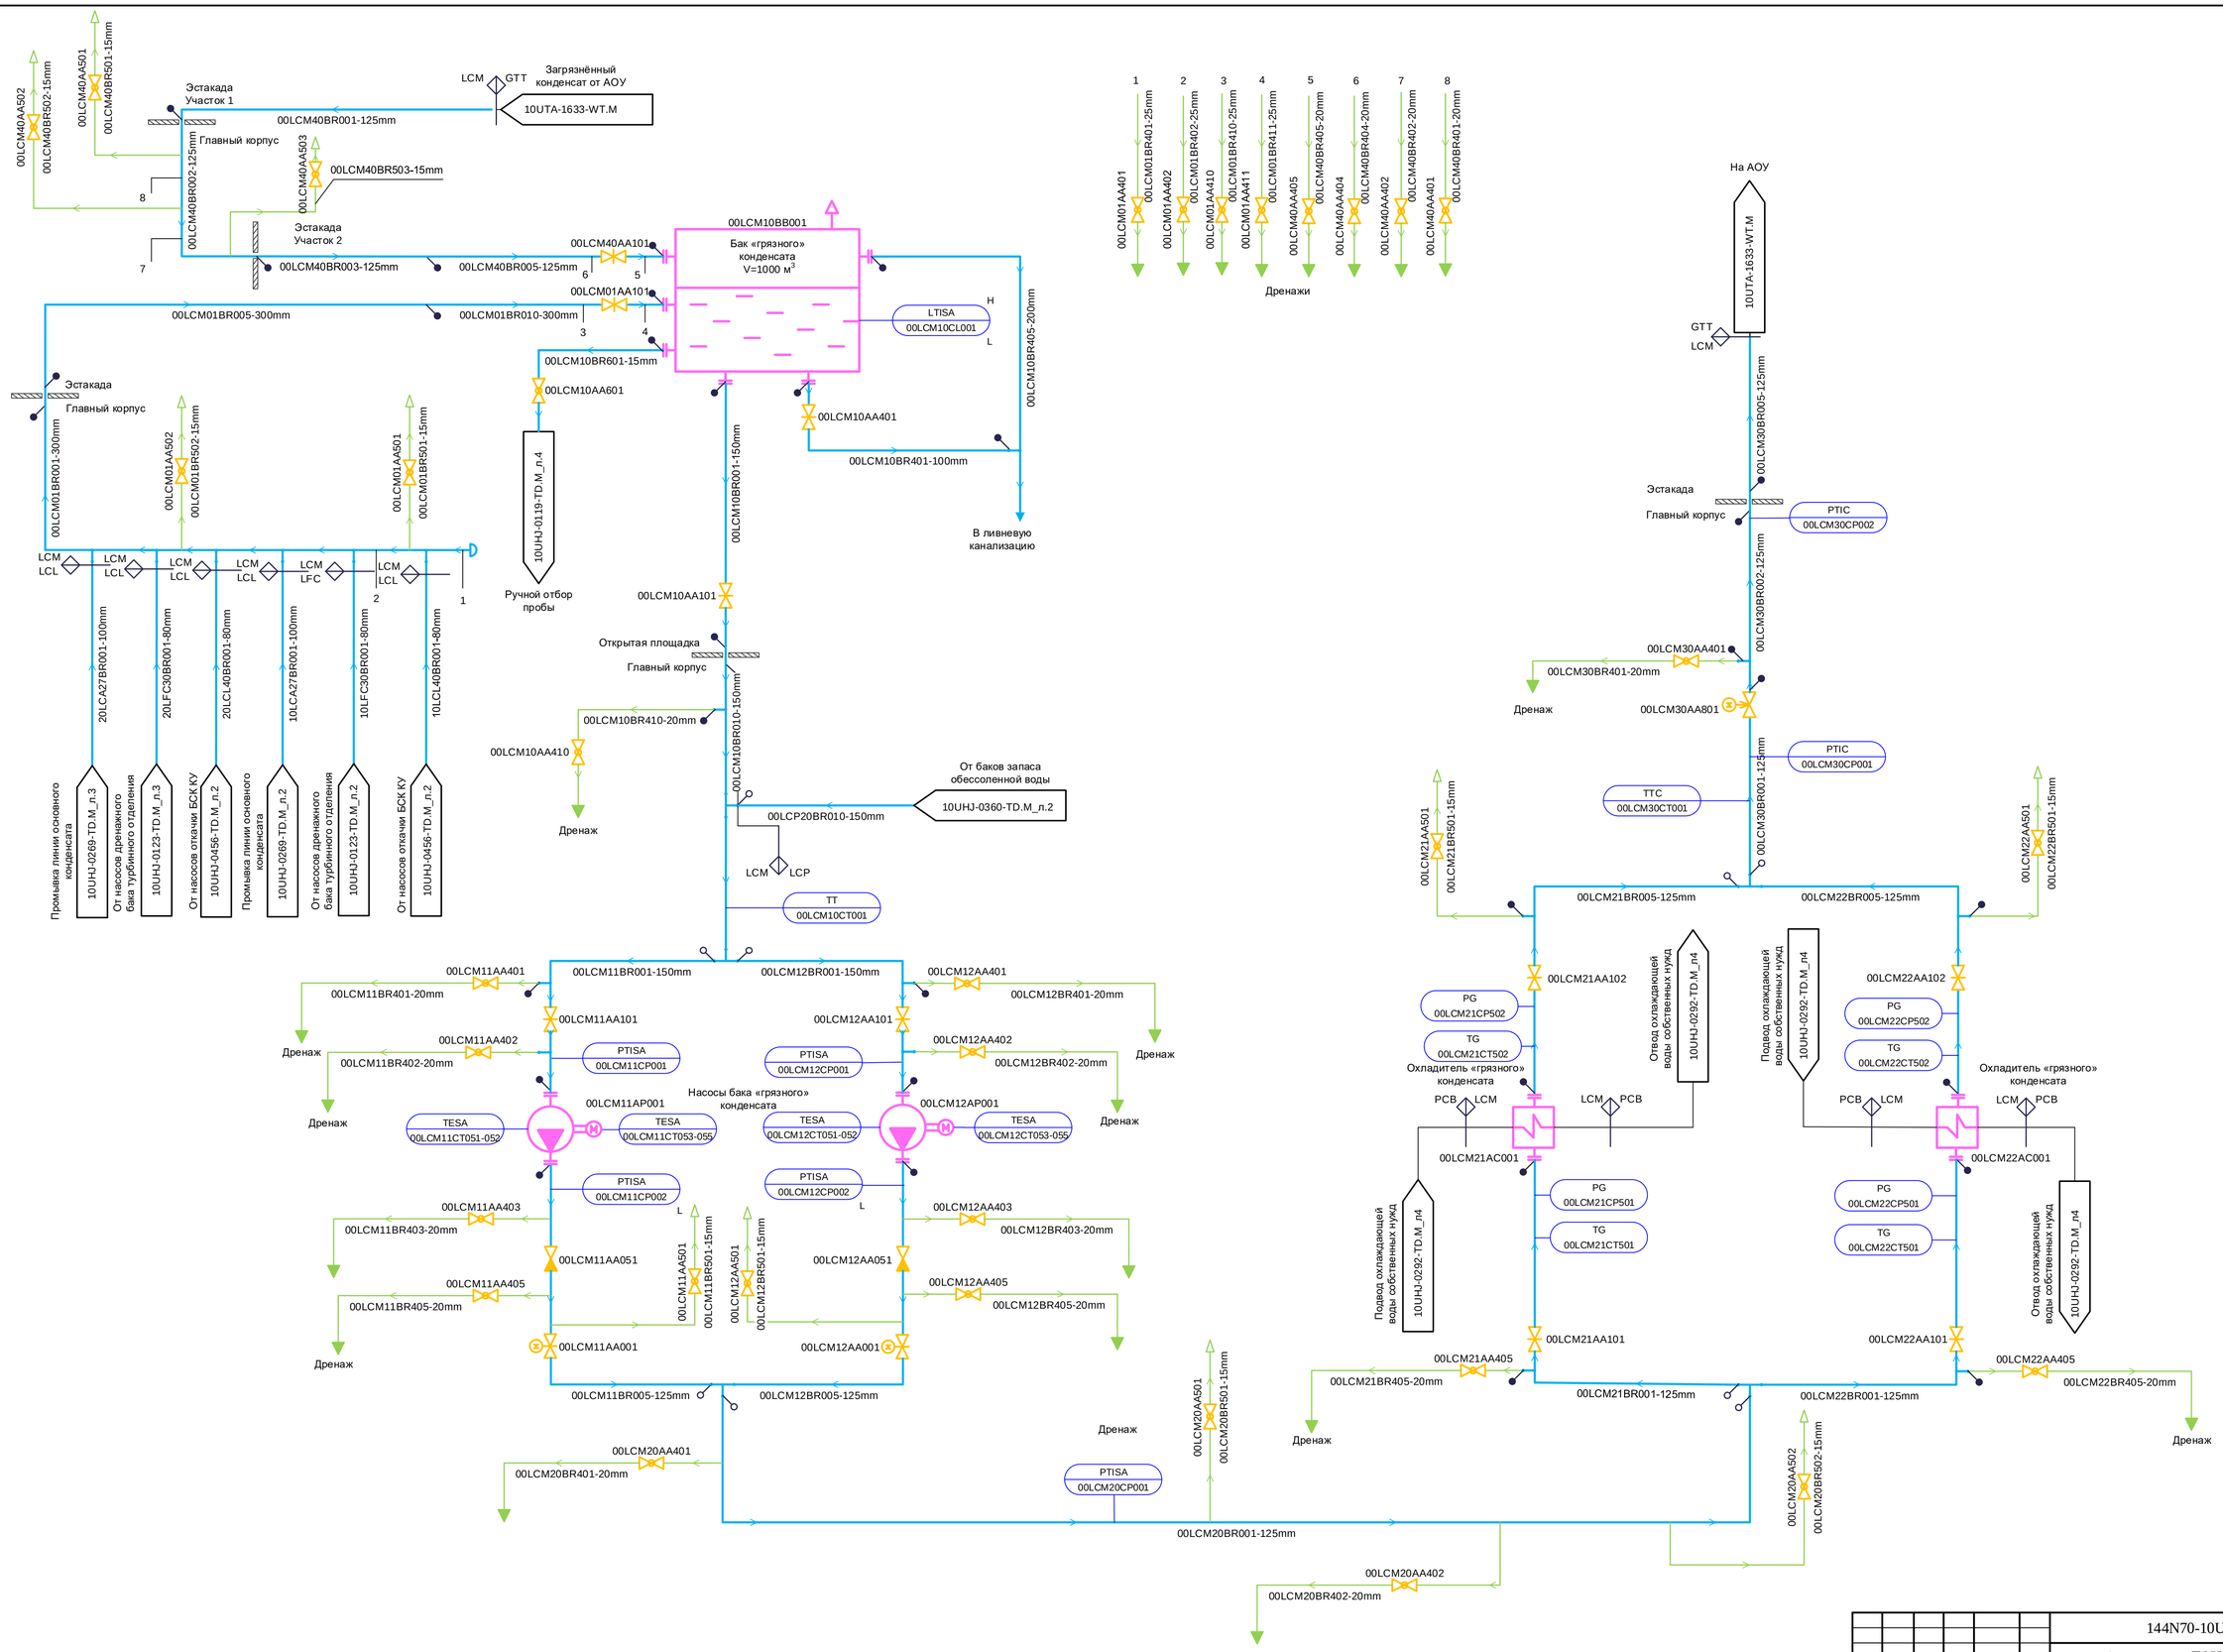

Изм.	Кол.уч	Лист	№ док.	Подп.	Дата	144N70-10UHJ-0328-TD.M
						Артемовская ТЭЦ-2 с внеплощадочной инфраструктурой
Разработал		Дроздов				Здание главного корпуса с баковым хозяйством. PI-диаграмма трубопроводов грязного конденсата.
Проверил		Дёмина				
Н. контр.		Астраханцев				PI-диаграмма трубопроводов грязного конденсата. Система LCM.

Стадия	Лист	Листов
Р	2	

АКЦИОНЕРНОЕ ОБЩЕСТВО ИНСТИТУТ ТЕПЛОЭЛЕКТРОПРОЕКТ Г. МОСКВА

Согласовано

Взам. инв. №

Подпись и дата

Инв. № подл.

Формат А1