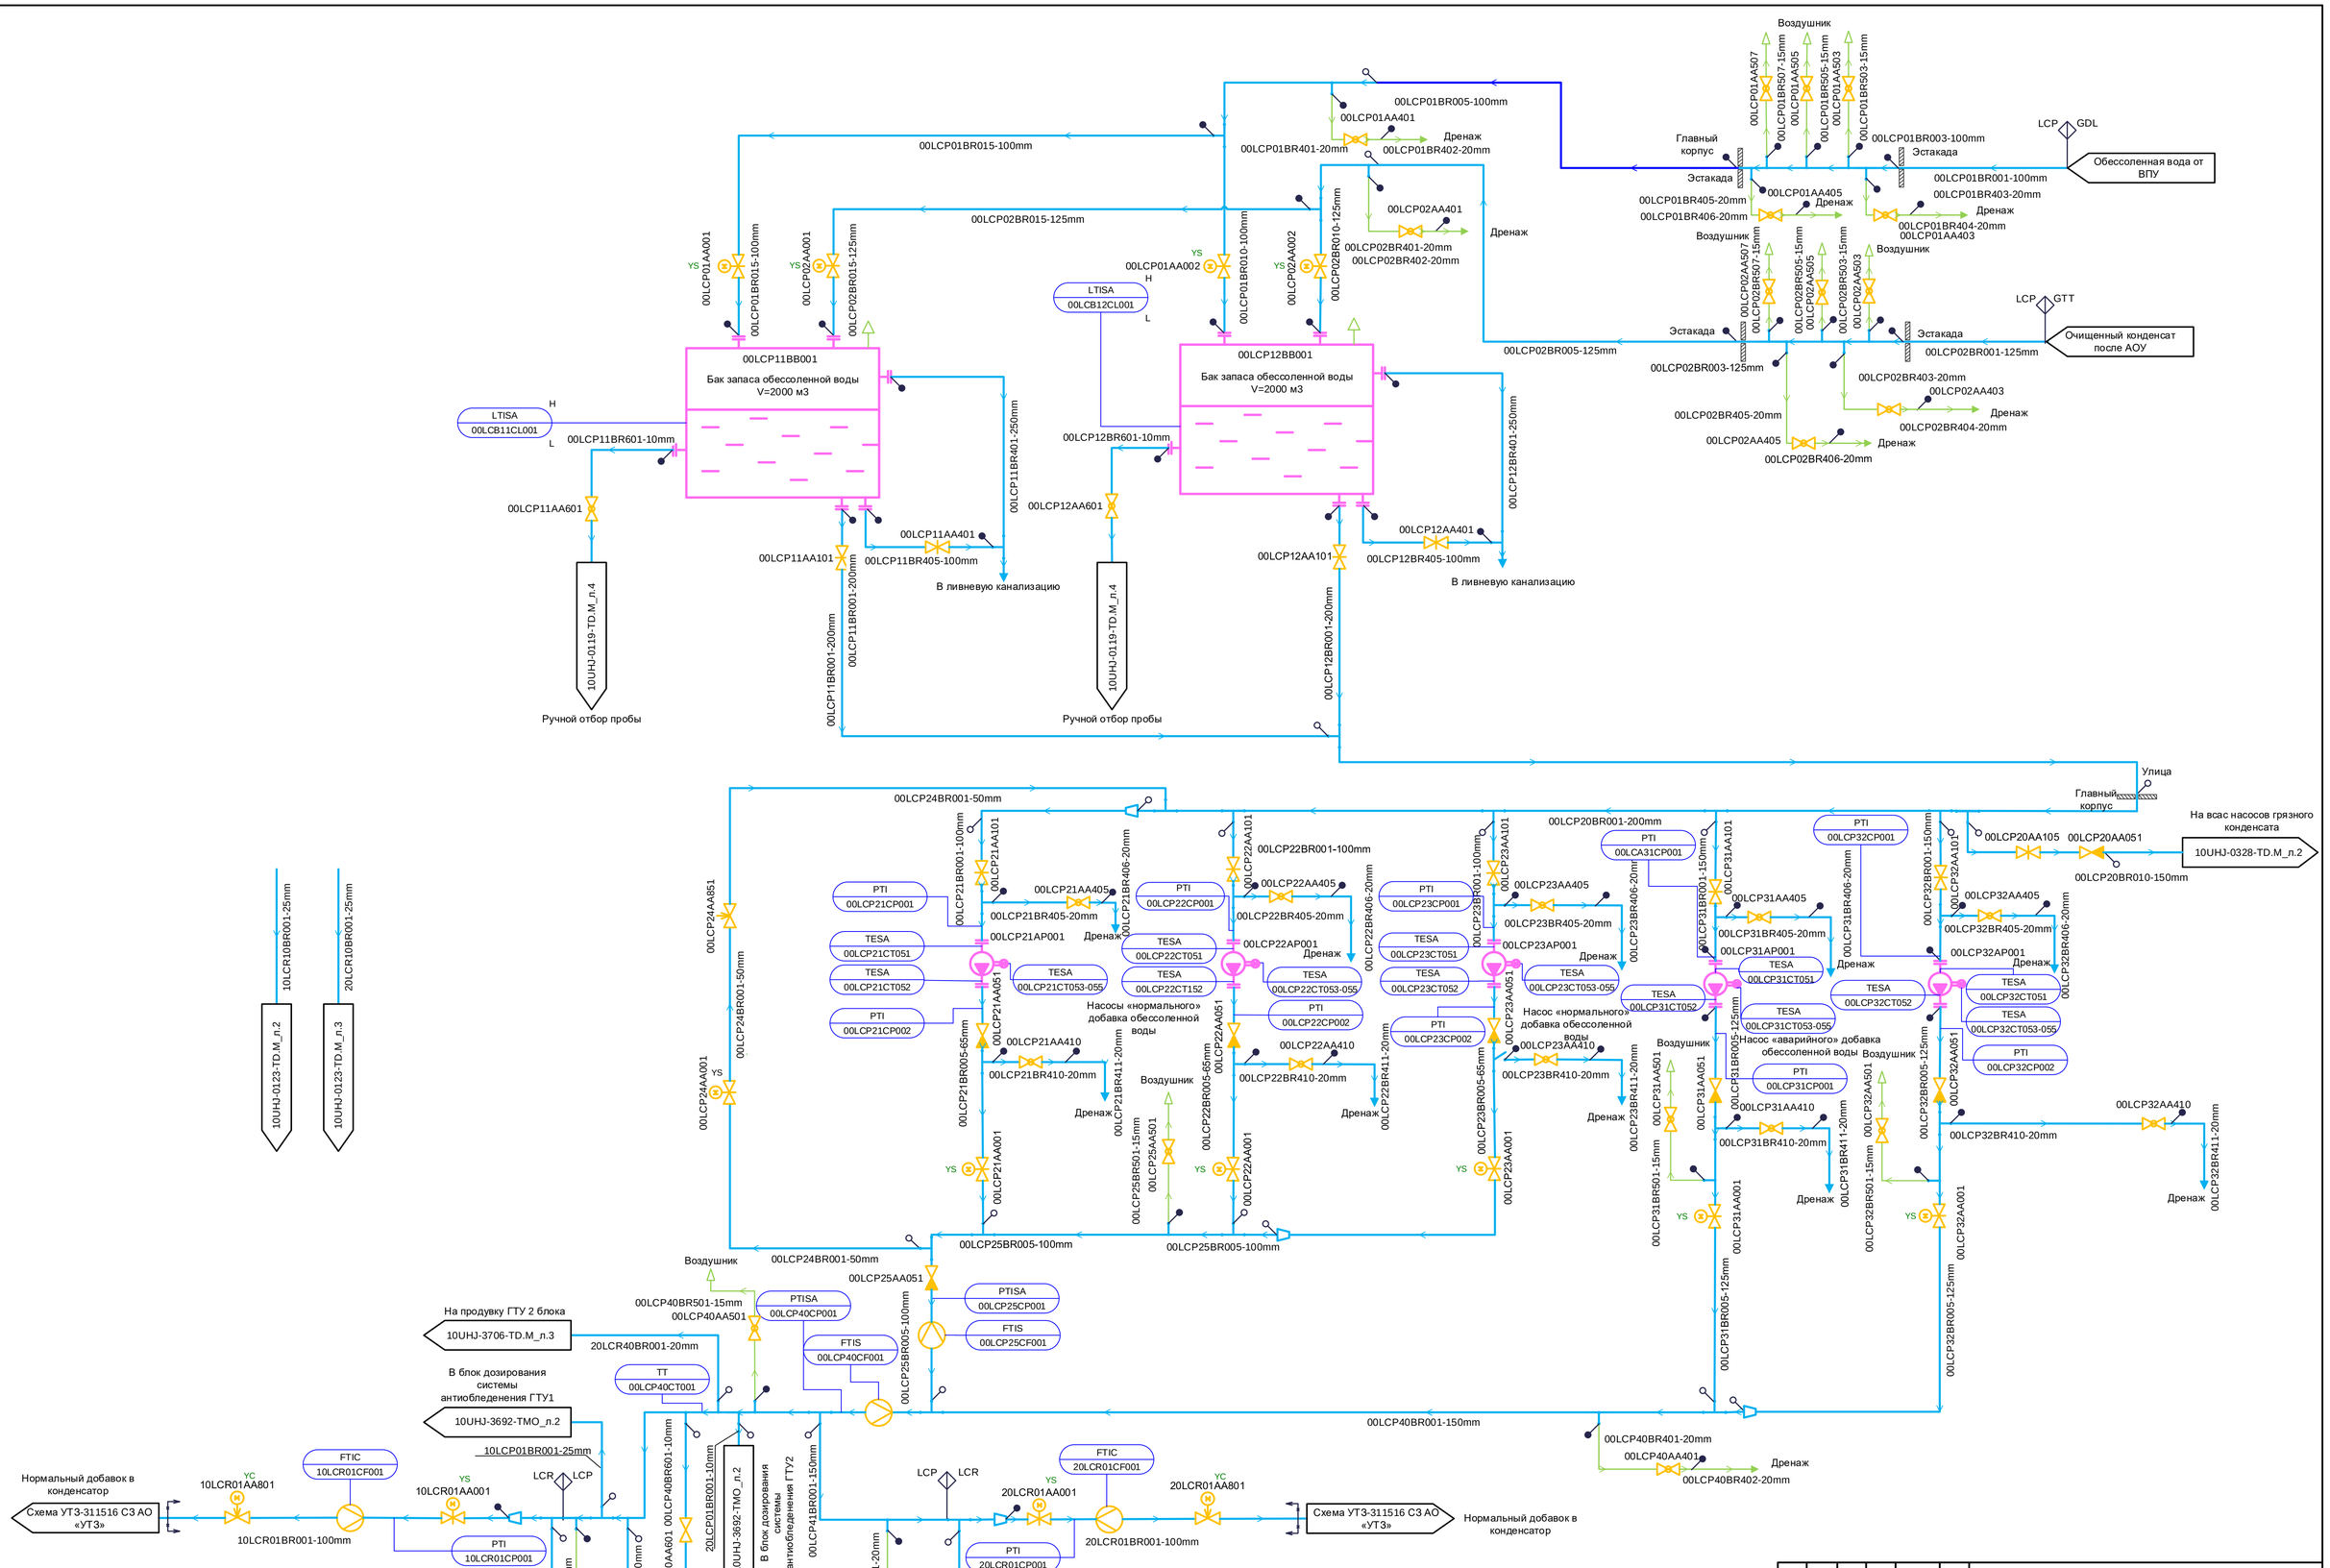
00LCP11BB001
Бак запаса обессоленной воды
V=2000 м3
00LCP12BB001
Бак запаса обессоленной воды
V=2000 м3
LTISA
00LCB11CL001
LTISA
00LCB12CL001
00LCP01BR015-100mm
00LCP02BR015-125mm
00LCP01BR005-100mm
00LCP01AA401
00LCP01BR401-20mm
00LCP01BR402-20mm
00LCP02AA401
00LCP02BR401-20mm
00LCP02BR402-20mm
Дренаж
Воздушник
Главный корпус
Эстакада
00LCP01BR003-100mm
00LCP01BR001-100mm
00LCP01BR403-20mm
00LCP01BR404-20mm
00LCP01AA403
00LCP01AA405
00LCP01BR405-20mm
00LCP01BR406-20mm
LCP GDL
Обессоленная вода от ВПУ
00LCP02BR005-125mm
00LCP02BR003-125mm
00LCP02BR001-125mm
00LCP02BR403-20mm
00LCP02AA403
00LCP02BR404-20mm
00LCP02AA405
00LCP02BR405-20mm
00LCP02BR406-20mm
LCP GTT
Очищенный конденсат после АОУ
00LCP11BR601-10mm
00LCP12BR601-10mm
00LCP11AA601
00LCP12AA601
00LCP11AA101
00LCP12AA101
00LCP11AA401
00LCP12AA401
00LCP11BR405-100mm
00LCP12BR405-100mm
00LCP11BR401-250mm
00LCP12BR401-250mm
В ливневую канализацию
00LCP11BR001-200mm
00LCP12BR001-200mm
10UHJ-0119-TD.M_л.4
Ручной отбор пробы
Улица
00LCP24BR001-50mm
00LCP20BR001-200mm
На всас насосов грязного конденсата
10UHJ-0328-TD.M_л.2
00LCP20AA105
00LCP20AA051
00LCP20BR010-150mm
10LCR10BR001-25mm
20LCR10BR001-25mm
10UHJ-0123-TD.M_л.2
10UHJ-0123-TD.M_л.3
00LCP24AA851
00LCP24BR001-50mm
00LCP24AA001
00LCP21CP001
00LCP21BR001-100mm
00LCP21AA101
00LCP21AA405
00LCP21BR405-20mm
00LCP21BR406-20mm
00LCP21AP001
00LCP21CT051
00LCP21CT052
00LCP21CT053-055
00LCP21CP002
00LCP21AA051
00LCP21BR005-65mm
00LCP21AA410
00LCP21BR410-20mm
00LCP21BR411-20mm
00LCP21AA001
00LCP22BR001-100mm
00LCP22CP001
00LCP22AA405
00LCP22BR405-20mm
00LCP22BR406-20mm
00LCP22AP001
00LCP22CT051
00LCP22CT152
00LCP22CT053-055
00LCP22CP002
00LCP22AA051
00LCP22BR005-65mm
00LCP22AA410
00LCP22BR410-20mm
00LCP22BR411-20mm
00LCP22AA001
00LCP23CP001
00LCP23BR001-100mm
00LCP23AA101
00LCP23AA405
00LCP23BR405-20mm
00LCP23BR406-20mm
00LCP23AP001
00LCP23CT051
00LCP23CT052
00LCP23CT053-055
00LCP23CP002
00LCP23AA051
00LCP23BR005-65mm
00LCP23AA410
00LCP23BR410-20mm
00LCP23BR411-20mm
00LCP23AA001
00LCP31CP001
00LCP31BR001-150mm
00LCP31AA101
00LCP31AA405
00LCP31BR405-20mm
00LCP31BR406-20mm
00LCP31AP001
00LCP31CT051
00LCP31CT052
00LCP31CT053-055
00LCP31AA051
00LCP31BR005-125mm
00LCP31AA410
00LCP31BR410-20mm
00LCP31BR411-20mm
00LCP31AA001
00LCP32CP001
00LCP32BR001-150mm
00LCP32AA101
00LCP32AA405
00LCP32BR405-20mm
00LCP32BR406-20mm
00LCP32AP001
00LCP32CT051
00LCP32CT052
00LCP32CT053-055
00LCP32CP002
00LCP32AA051
00LCP32BR005-125mm
00LCP32AA410
00LCP32BR410-20mm
00LCP32BR411-20mm
00LCP32AA001
00LCP25BR005-100mm
00LCP25AA051
00LCP25CP001
00LCP25CF001
00LCP25BR501-15mm
00LCP25AA501
00LCP40BR501-15mm
00LCP40AA501
00LCP40CP001
00LCP40CF001
00LCP40BR001-150mm
00LCP40BR401-20mm
00LCP40AA401
00LCP40BR402-20mm
00LCP31BR501-15mm
00LCP31AA501
00LCP32AA501
00LCP32BR501-15mm
На продувку ГТУ 2 блока
10UHJ-3706-TD.M_л.3
20LCR40BR001-20mm
В блок дозирования системы антиобледенения ГТУ1
10UHJ-3692-TMO_л.2
10LCP01BR001-25mm
00LCP01BR001-10mm
00LCP40AA601
00LCP40BR601-10mm
10LCR40BR001-20mm
00LCP40BR405-20mm
00LCP40AA405
00LCP40BR406-20mm
00LCP41BR001-150mm
00LCP41BR401-20mm
00LCP41AA401
00LCP41BR402-20mm
10UHJ-3692-TMO_л.2
В блок дозирования системы антиобледенения ГТУ2
Отбор пробы
10UHJ-0119-TD.M_л.2
На продувку ГТУ 1 блока
10UHJ-3706-TD.M_л.2
Нормальный добавок в конденсатор
Схема УТЗ-311516 С3 АО «УТЗ»
10LCR01AA801
10LCR01BR001-100mm
10LCR01AA001
10LCR01CF001
10LCR01CP001
Аварийный добавок в расширитель конденсатора
10LCR02AA801
10LCR02BR001-125mm
10LCR02AA001
10LCR02CF001
10LCR02CP001
20LCR01AA001
20LCR01AA801
20LCR01BR001-100mm
20LCR01CF001
20LCR01CP001
20LCR02AA001
20LCR02AA801
20LCR02BR001-125mm
20LCR02CF001
20LCR02CP001
Схема УТЗ-311516 С3 АО «УТЗ»
Нормальный добавок в конденсатор
Аварийный добавок в расширитель конденсатора
Насосы «нормального» добавка обессоленной воды
Насос «нормального» добавка обессоленной воды
Насос «аварийного» добавка обессоленной воды
144N70-10UHJ-0360-TD.M
Строительство Артемовской ТЭЦ-2 с внеплощадочной инфраструктурой.
Изм. Кол.уч Лист № док. Подп. Дата
Разработал Гусев.Т
Проверил Демина
Гл.спец. Смирнова
Н. контр. Черемушкина
Главный корпус.
PI-Диаграмма трубопроводов обессоленной воды.
Стадия Лист Листов
Р 2
PI-Диаграмма трубопроводов обессоленной воды. Система LCR.
АКЦИОНЕРНОЕ ОБЩЕСТВО ИНСТИТУТ ТЕПЛОЭЛЕКТРОПРОЕКТ Г. МОСКВА
Согласовано
Взам. инв. №
Подпись и дата
Инв. № подл.
Формат А1