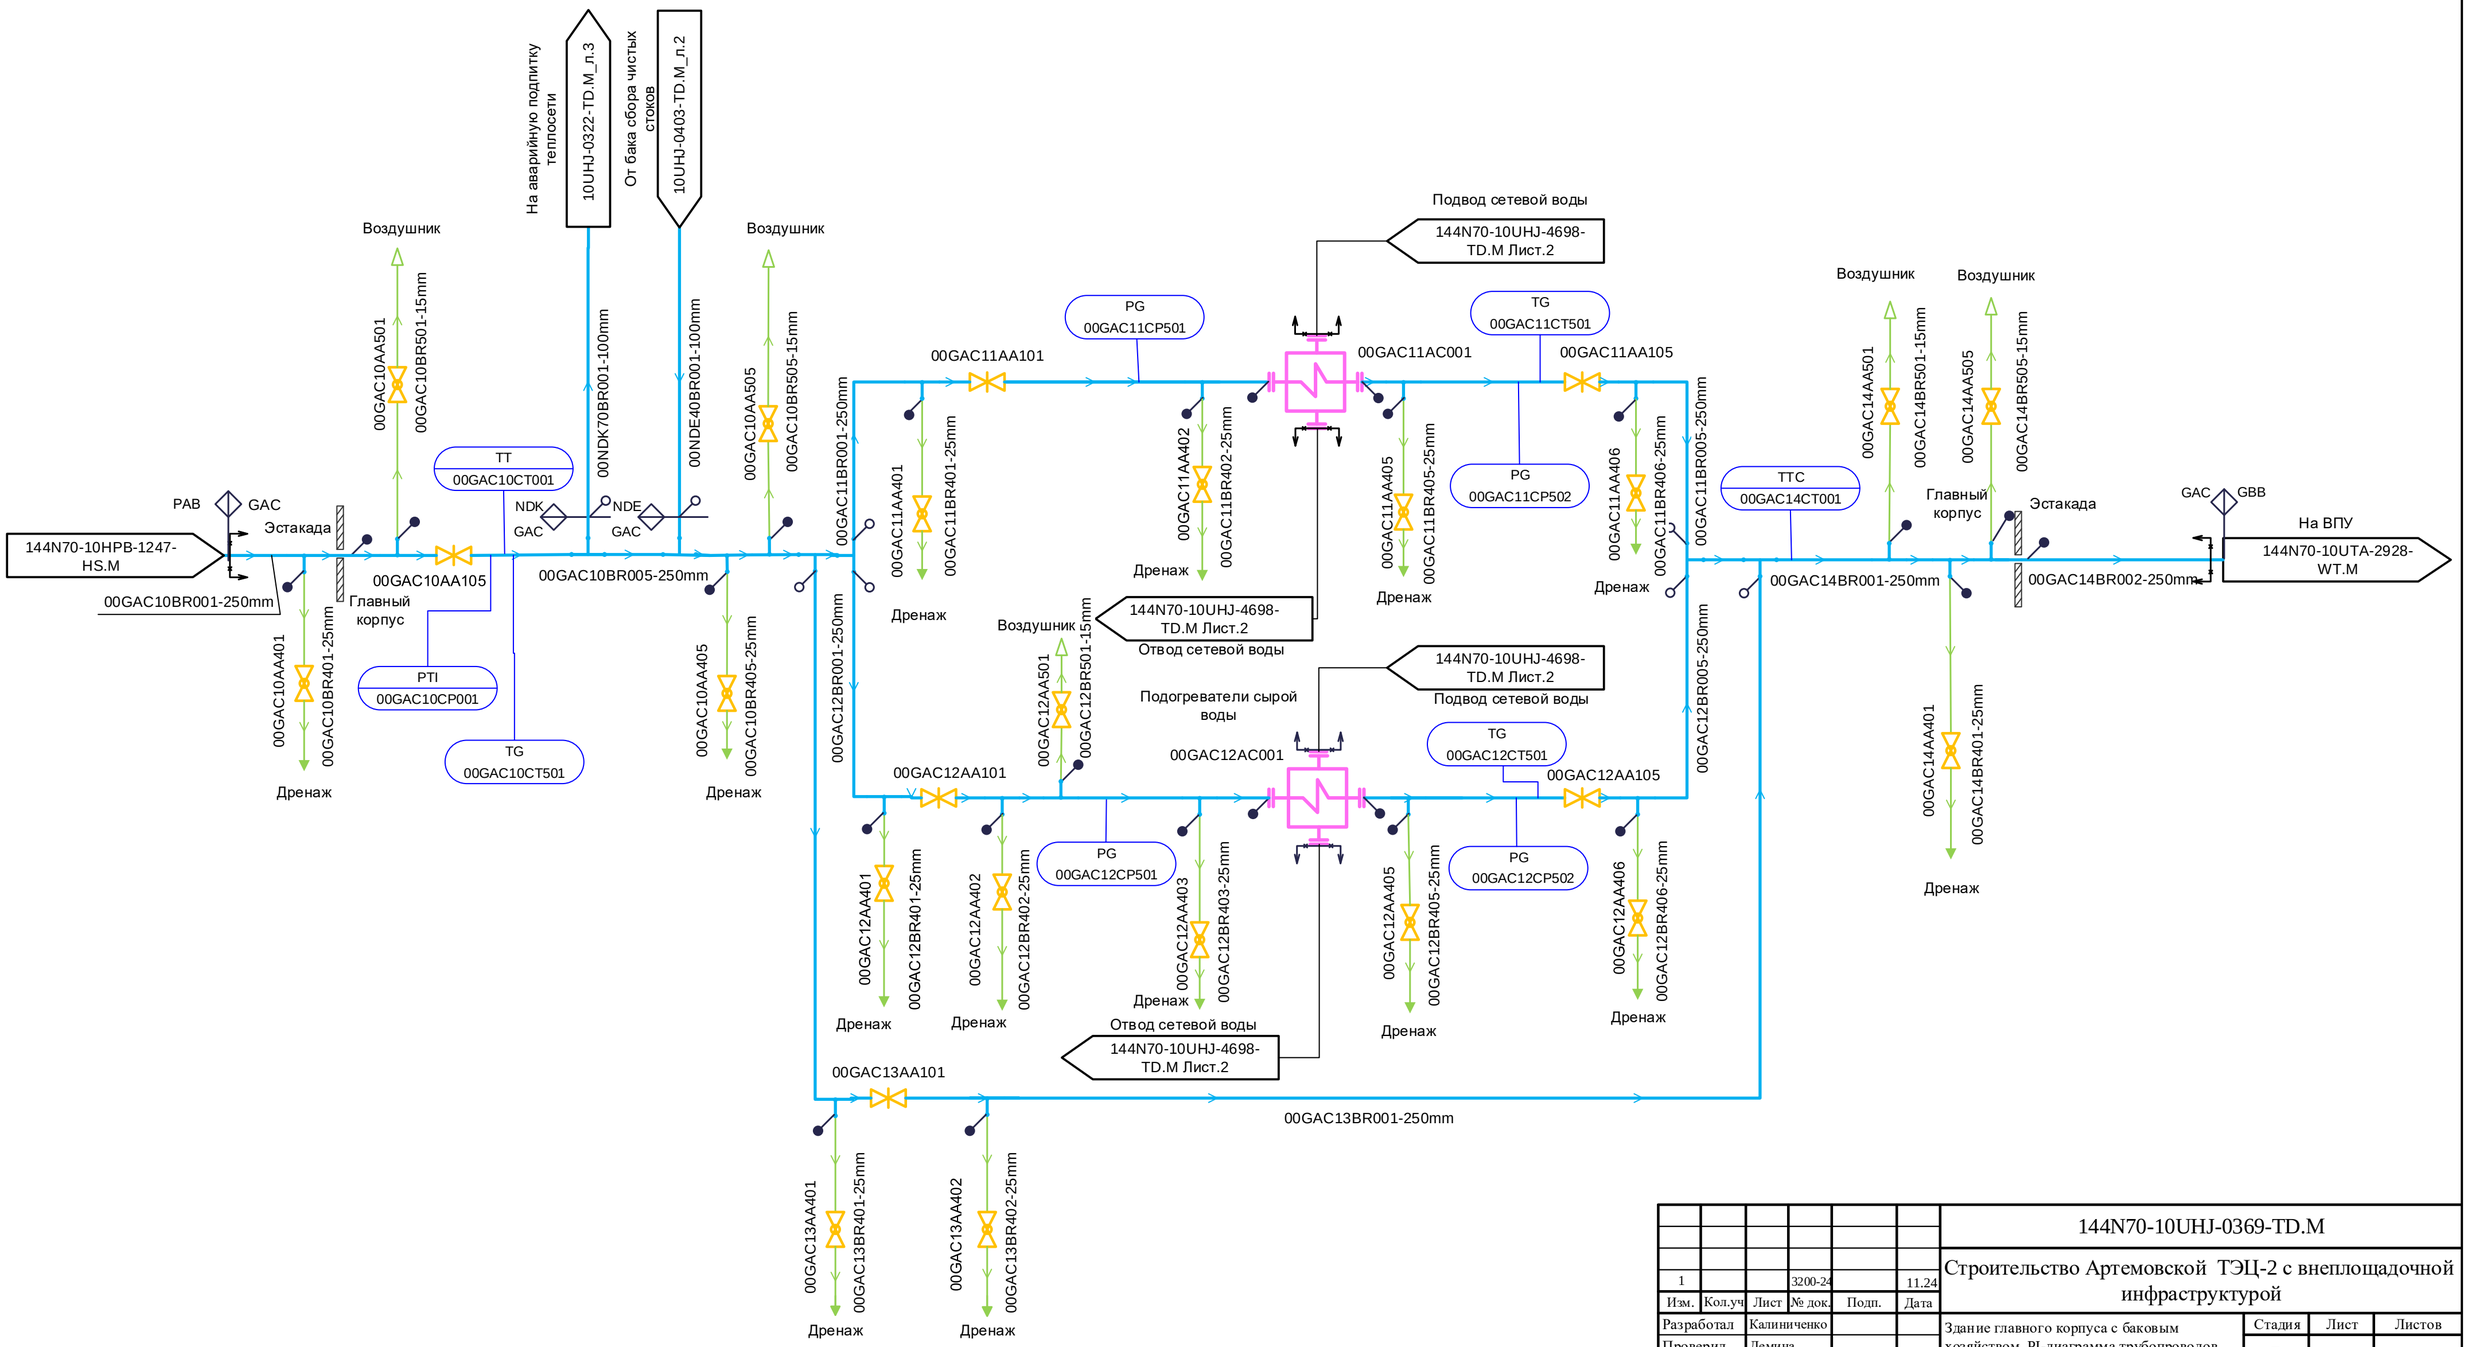

1			3200-24		11.24	
Изм.	Кол.уч	Лист	№ док.	Подп.	Дата	
Разработал		Калиниченко				
Проверил		Демина				
Глав.спец		Смирнова				
Н. контр.		Черемушкина				

144N70-10UHJ-0369-TD.M

Строительство Артемовской ТЭЦ-2 с внеплощадочной инфраструктурой

Здание главного корпуса с баковым хозяйством. PI-диаграмма трубопроводов сырой воды.

Стадия	Лист	Листов
Р	2	

PI-Диаграмма трубопроводов сырой воды. Система GAC.

АКЦИОНЕРНОЕ ОБЩЕСТВО ИНСТИТУТ ТЕПЛОЭЛЕКТРОПРОЕКТ Г. МОСКВА

Согласовано

ОАСУ Соболева

Взам. инв. №

Подпись и дата

Инв. № подл.

Формат А2